


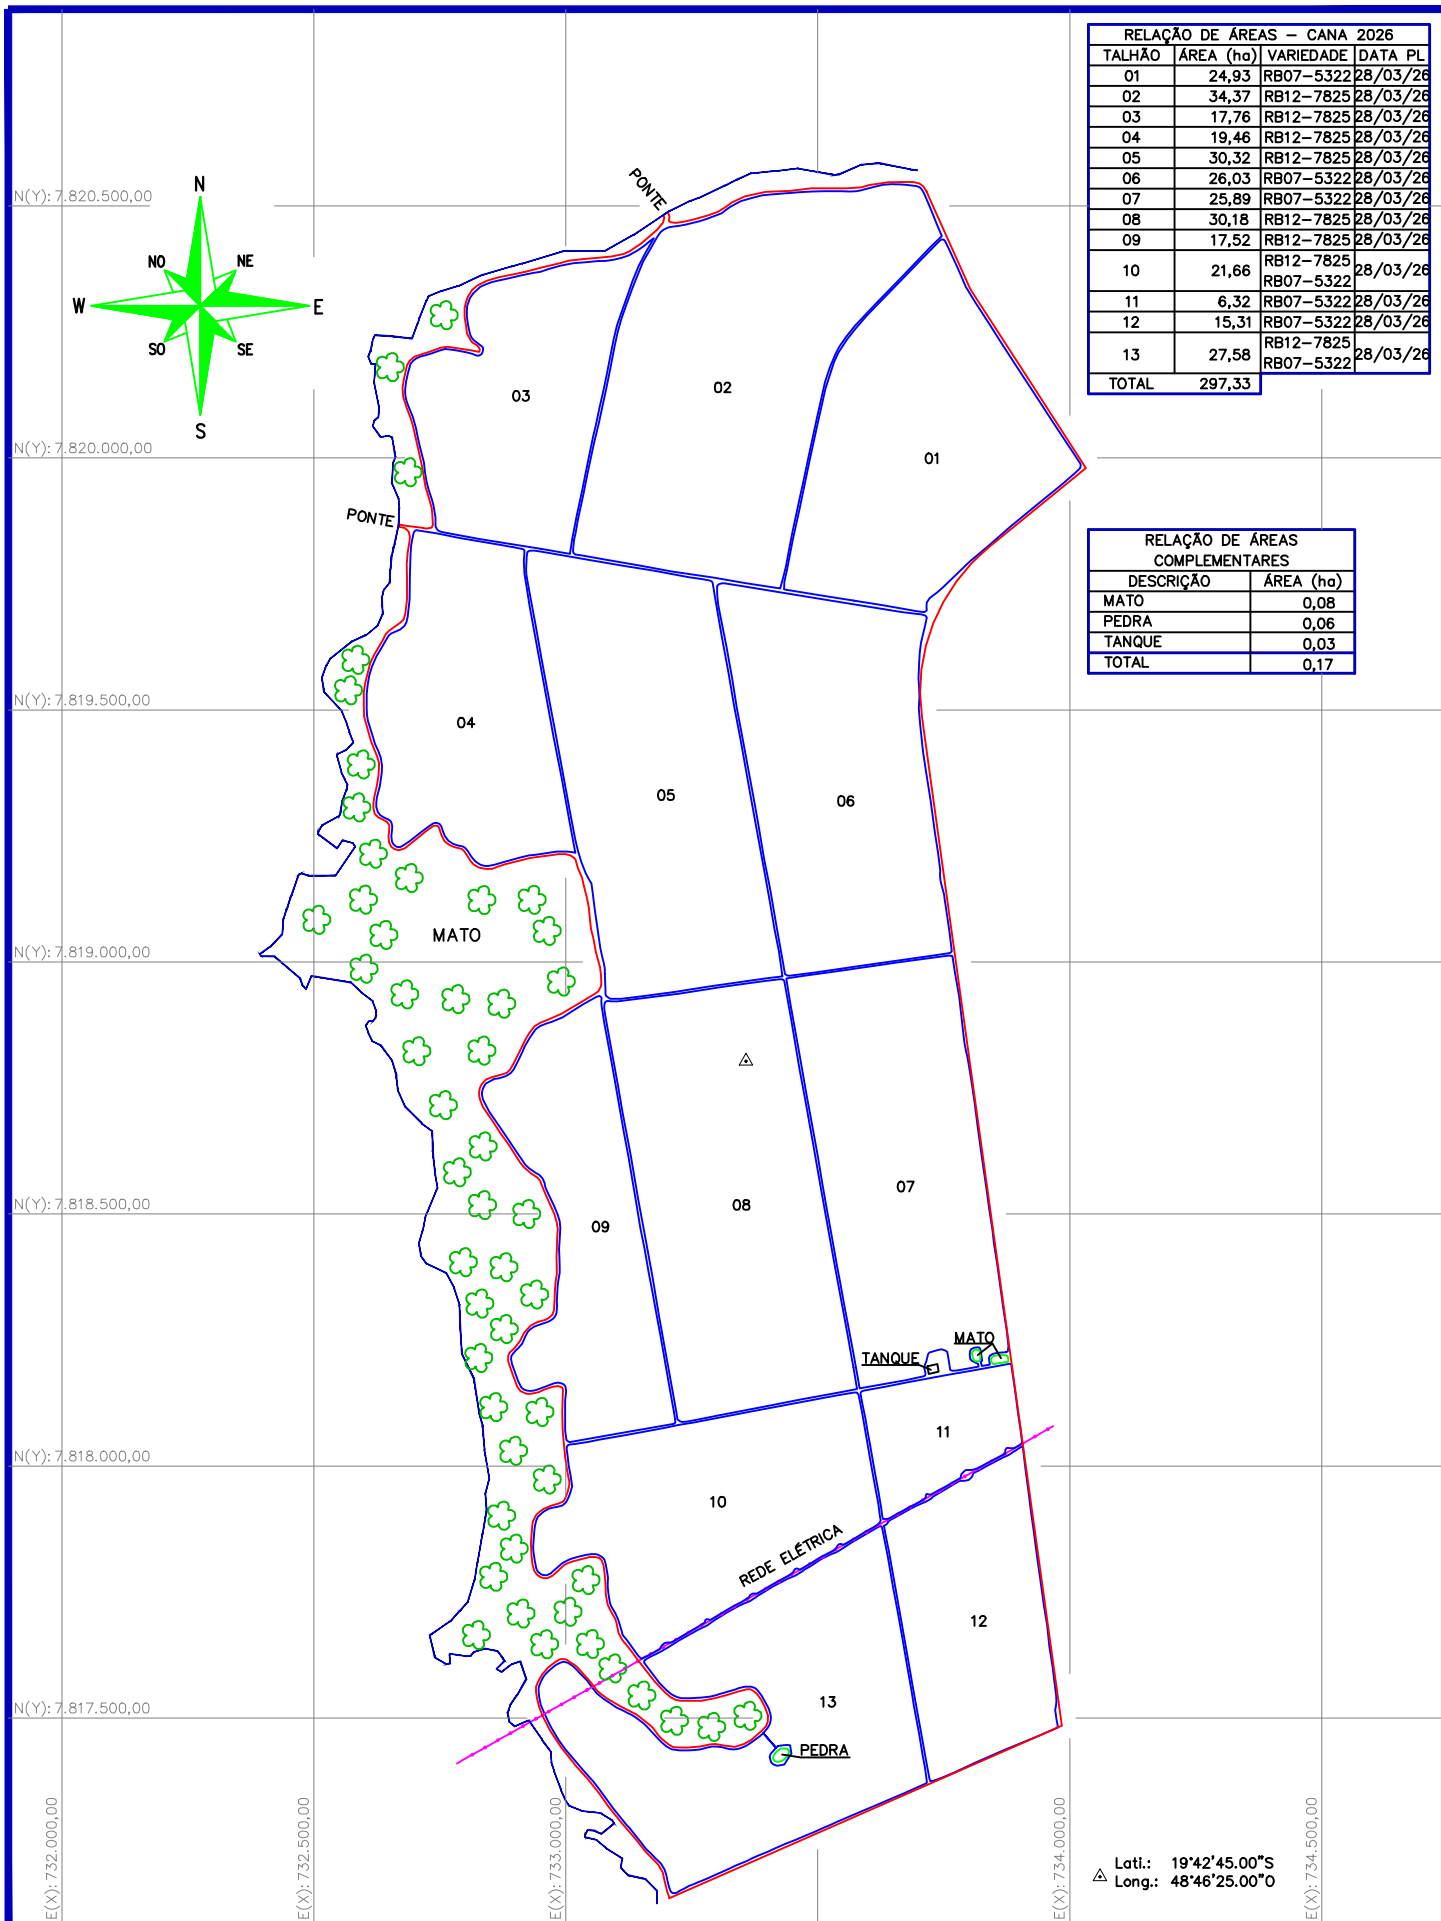

RELAÇÃO DE ÁREAS – CANA 2026			
TALHÃO	ÁREA (ha)	VARIETADE	DATA PL
01	24,93	RB07-5322	28/03/26
02	34,37	RB12-7825	28/03/26
03	17,76	RB12-7825	28/03/26
04	19,46	RB12-7825	28/03/26
05	30,32	RB12-7825	28/03/26
06	26,03	RB07-5322	28/03/26
07	25,89	RB07-5322	28/03/26
08	30,18	RB12-7825	28/03/26
09	17,52	RB12-7825	28/03/26
10	21,66	RB12-7825	28/03/26
11	6,32	RB07-5322	28/03/26
12	15,31	RB07-5322	28/03/26
13	27,58	RB12-7825	28/03/26
TOTAL		297,33	

RELAÇÃO DE ÁREAS COMPLEMENTARES	
DESCRIÇÃO	ÁREA (ha)
MATO	0,08
PEDRA	0,06
TANQUE	0,03
TOTAL	0,17

 LEVANTAMENTO TOPOGRÁFICO	PROPRIEDADE: 005 – FAZENDA OURO VERDE / DAS ALMAS	QUADRO DE ÁREAS (ha)	CANA 2026:	297,33	Desenhado por: WENER LIMA	Data: 21/04/2026	Núcleo: 1 USINA
	PROPRIETÁRIO: ADEMIR FERREIRA DE MELLO		CARREADOR 2026:	10,10	Atualizado por:	Data:	
	FORNECEDOR: ADEMIR FERREIRA DE MELLO		COMPLEMENTARES:	0,17	Engenheiro Agrimensor: DANIEL CÉSAR DA SILVA		
	ÁREA TOTAL: 307,60 Hectares				Município: CAMPO FLORIDO	Escala: 1 : 15.000	Data Levant.: 13/04/2026

Obs.: Conferido perímetro georreferenciado.
Datum Sirgas2000 / UTM zona 22S (CM 51W)