


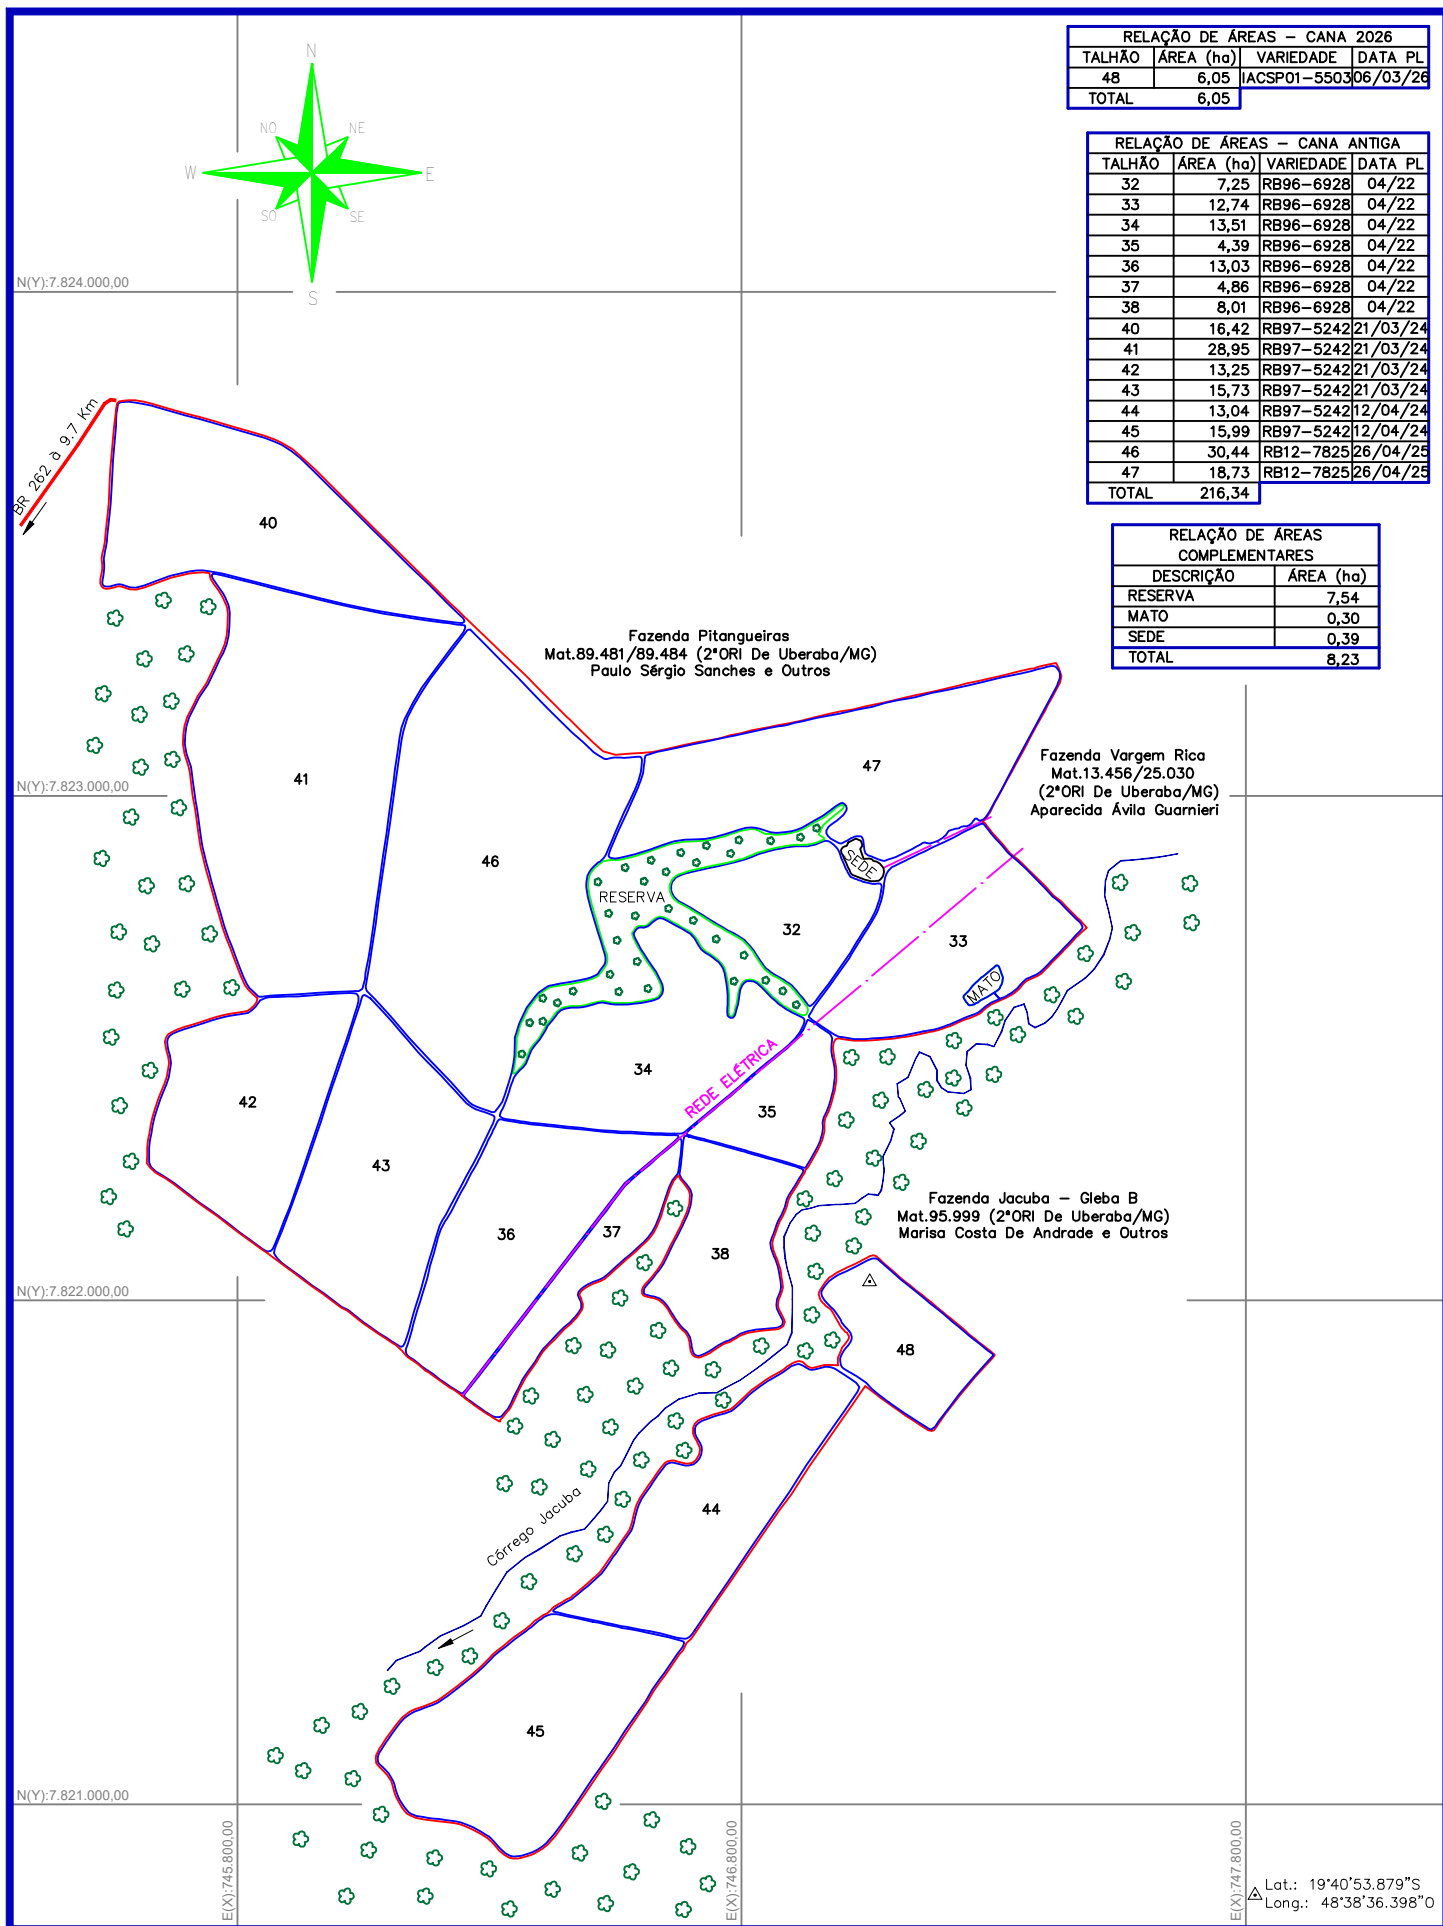

RELAÇÃO DE ÁREAS – CANA 2026			
TALHÃO	ÁREA (ha)	VARIETADE	DATA PL
48	6,05	IACSP01–5503	06/03/26
TOTAL		6,05	

RELAÇÃO DE ÁREAS – CANA ANTIGA			
TALHÃO	ÁREA (ha)	VARIETADE	DATA PL
32	7,25	RB96–6928	04/22
33	12,74	RB96–6928	04/22
34	13,51	RB96–6928	04/22
35	4,39	RB96–6928	04/22
36	13,03	RB96–6928	04/22
37	4,86	RB96–6928	04/22
38	8,01	RB96–6928	04/22
40	16,42	RB97–5242	21/03/24
41	28,95	RB97–5242	21/03/24
42	13,25	RB97–5242	21/03/24
43	15,73	RB97–5242	21/03/24
44	13,04	RB97–5242	12/04/24
45	15,99	RB97–5242	12/04/24
46	30,44	RB12–7825	26/04/25
47	18,73	RB12–7825	26/04/25
TOTAL		216,34	

RELAÇÃO DE ÁREAS COMPLEMENTARES	
DESCRIÇÃO	ÁREA (ha)
RESERVA	7,54
MATO	0,30
SEDE	0,39
TOTAL	8,23

 USINA CORUPIPE Filial Campo Florido	PROPRIEDADE: 438 – FAZENDA JACUBA	QUADRO DE ÁREAS (ha)	CANA 2026:	6,05	Desenhado por: JÚLIA GOMES	Data: 27/05/2025	Núcleo: 1 USINA	
	PROPRIETÁRIO: MARISA COSTA DE ANDRADE		CARREADOR 2026:	0,33	Revisado por: MÁRCIO GALASSI	Data: 21/04/2026		
	FORNECEDOR: ADEMIR FERREIRA DE MELLO		CANA ANTIGA:	216,34	Engenheiro Agrimensor: DANIEL CESAR DA SILVA			
	LEVANTAMENTO TOPOGRÁFICO		ÁREA TOTAL: 238,96 Hectares	CARREADOR ANTIGO:	8,01	Município: CAMPO FLORIDO	Escala: 1 : 15.000	Data Levant.: 04/2026
				COMPLEMENTARES:	8,23			