
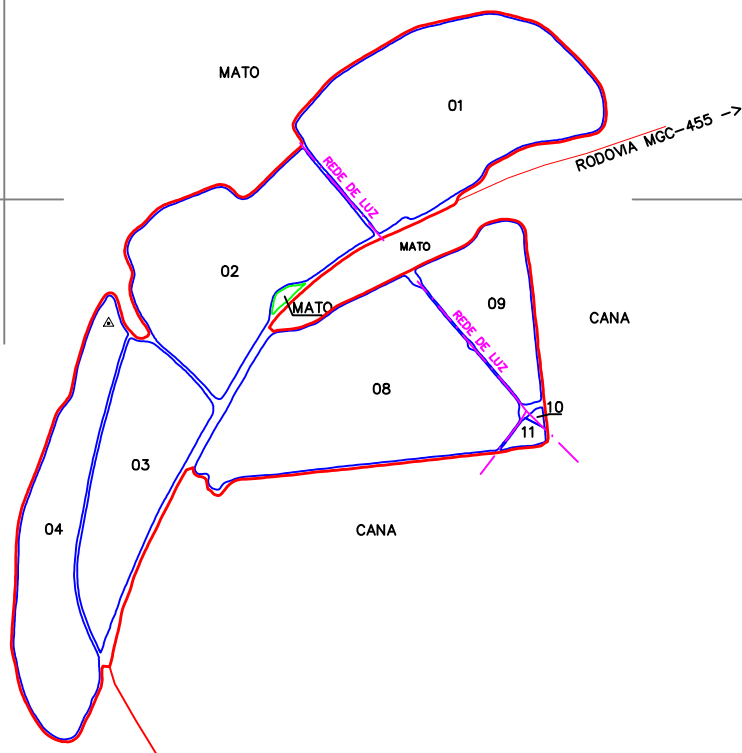
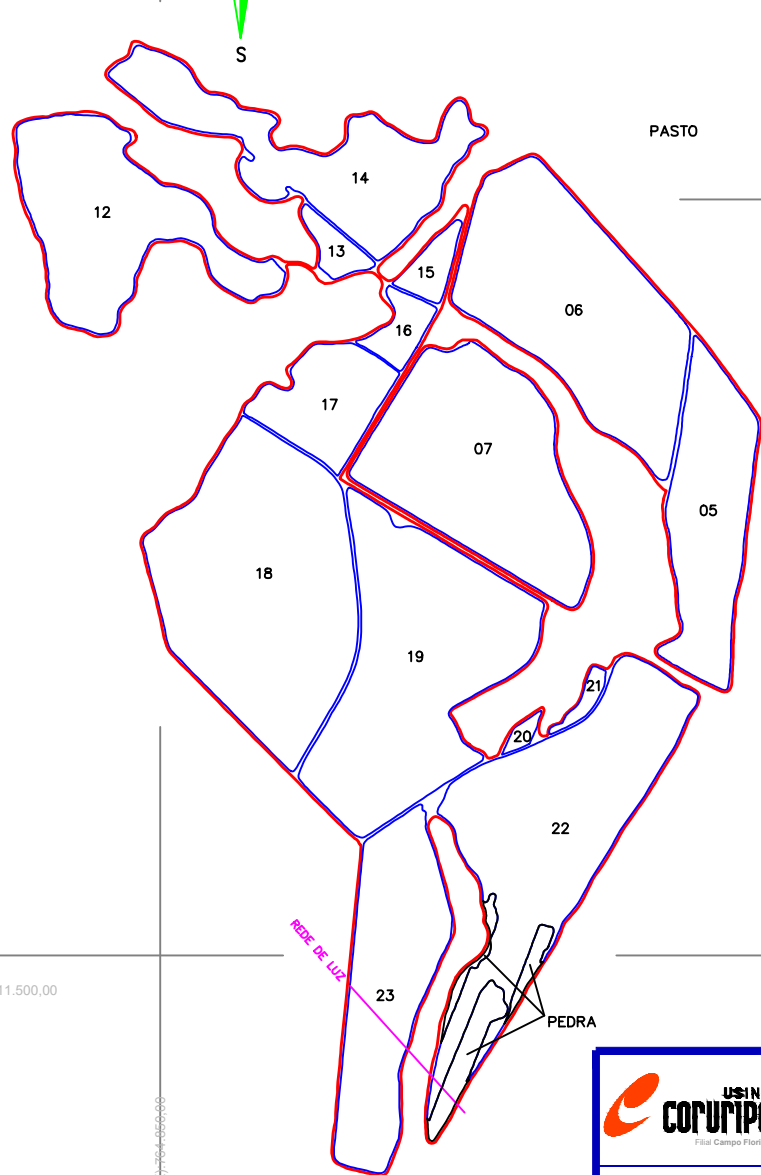


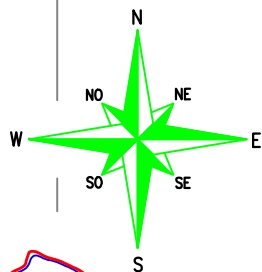

RELAÇÃO DE ÁREAS – CANA 2026			
TALHÃO	ÁREA (ha)	VARIEDADE	DATA PL
12	4,84	RB97–5201	04/2026
13	0,41	RB97–5201	04/2026
14	4,35	RB97–5201	04/2026
15	0,46	RB97–5201	04/2026
16	0,53	RB97–5201	04/2026
17	1,94	RB97–5201	04/2026
18	8,51	IAC–5503	03/2026
19	7,54	RB12–7825	03/2026
20	0,12	RB97–5201	04/2026
21	0,19	RB97–5201	04/2026
22	7,01	RB12–7825	04/2026
23	4,41	RB97–5201	04/2026
TOTAL	40,31		

RELAÇÃO DE ÁREAS – CANA 2025			
TALHÃO	ÁREA (ha)	VARIEDADE	DATA PL
01	6,98	RB97–5201	15/04/25
02	5,35	RB97–5201	15/04/25
03	3,55	RB12–7825	15/04/25
04	4,07	RB12–7825	15/04/25
05	3,73	RB97–5201	15/04/25
06	6,90	RB97–5201	15/04/25
07	6,29	RB12–7825	15/04/25
08	7,10	RB12–7825	15/04/25
09	2,16	RB12–7825	15/04/25
10	0,04	RB12–7825	15/04/25
11	0,14	RB12–7825	15/04/25
TOTAL	46,31		

RELAÇÃO DE ÁREAS COMPLEMENTARES	
DESCRIÇÃO	ÁREA (ha)
MATO:	0,06
PEDRA:	0,95
TOTAL	1,01

N(Y): 7.811.500,00

Lat.: 19°41'7.090"S
Long.: 48°34'46.795"O

 LEVANTAMENTO TOPOGRÁFICO	PROPRIEDADE: 1078 – FAZENDA GUARITAS E SÃO GREGÓRIO	QUADRO DE ÁREAS (ha)	CANA 2026:	40,31	Desenhado por:	GLAUBER PIMENTEL	Data:	19/05/2026	Núcleo: 01 USINA
	PROPRIETÁRIO: JOSÉ CARLOS DE CASTRO CASTANHEIRA		CARREADOR 2026:	3,04	Atualizado por:	—	Data:	—	
	FORNECEDOR: ALMERITA DA CONCEIÇÃO ROCHA XAVIER		CANA ANTIGA:	46,31	Responsável técnico: DANIEL CÉSAR DA SILVA				
	ÁREA TOTAL: 93,84 Hectares		CARREADOR ANTIGO:	3,17	Município: CAMPO FLORIDO—MG				
			COMPLEMENTARES:	1,01	Escala: 1 : 10.000		Data Levant.: 18/05/2026		

Obs.: Conferido perímetro georreferenciado.
Datum Sirgas2000 / UTM zona 22S (CM 51W)