

RELAÇÃO DE ÁREAS – CANA 2026			
TALHÃO	ÁREA (ha)	VARIEDADE	DATA PL
19	5,87	RB07 5322	04/2026
	9,31	RB97–5201	
TOTAL	15,18		

RELAÇÃO DE ÁREAS – CANA ANTIGA			
TALHÃO	ÁREA (ha)	VARIEDADE	DATA PL
20	16,31	RB97–5201	03/2022
21	3,74	RB97–5201	03/2022
22	14,66	RB97–5201	03/2022
23	7,15	RB97–5201	03/2022
24	1,26	RB97–5201	23/04/24
25	8,36	RB97–5201	23/04/24
26	12,98	RB97–5201	08/05/24
27	12,06	RB97–5201	05/05/24
28	2,66	RB97–5201	03/05/24
29	0,30	RB97–5201	23/04/24
32	17,41	RB97–5201	01/05/24
TOTAL	96,89		

RELAÇÃO DE ÁREAS – CANA 2025			
TALHÃO	ÁREA (ha)	VARIEDADE	DATA PL
34	0,94	RB97–5201	20/04/25
35	0,47	RB97–5201	20/04/25
36	5,08	RB97–5201	20/04/25
37	3,84	RB97–5201	20/04/25
TOTAL	10,33		


RELAÇÃO DE ÁREAS COMPLEMENTARES	
DESCRIÇÃO	ÁREA (ha)
SEDE	2,46
MATO	0,02
PEDRA	0,06
TOTAL	2,54

N(Y): 7.812.100,00

N(Y): 7.811.400,00

N(Y): 7.810.700,00

N(Y): 7.810.000,00

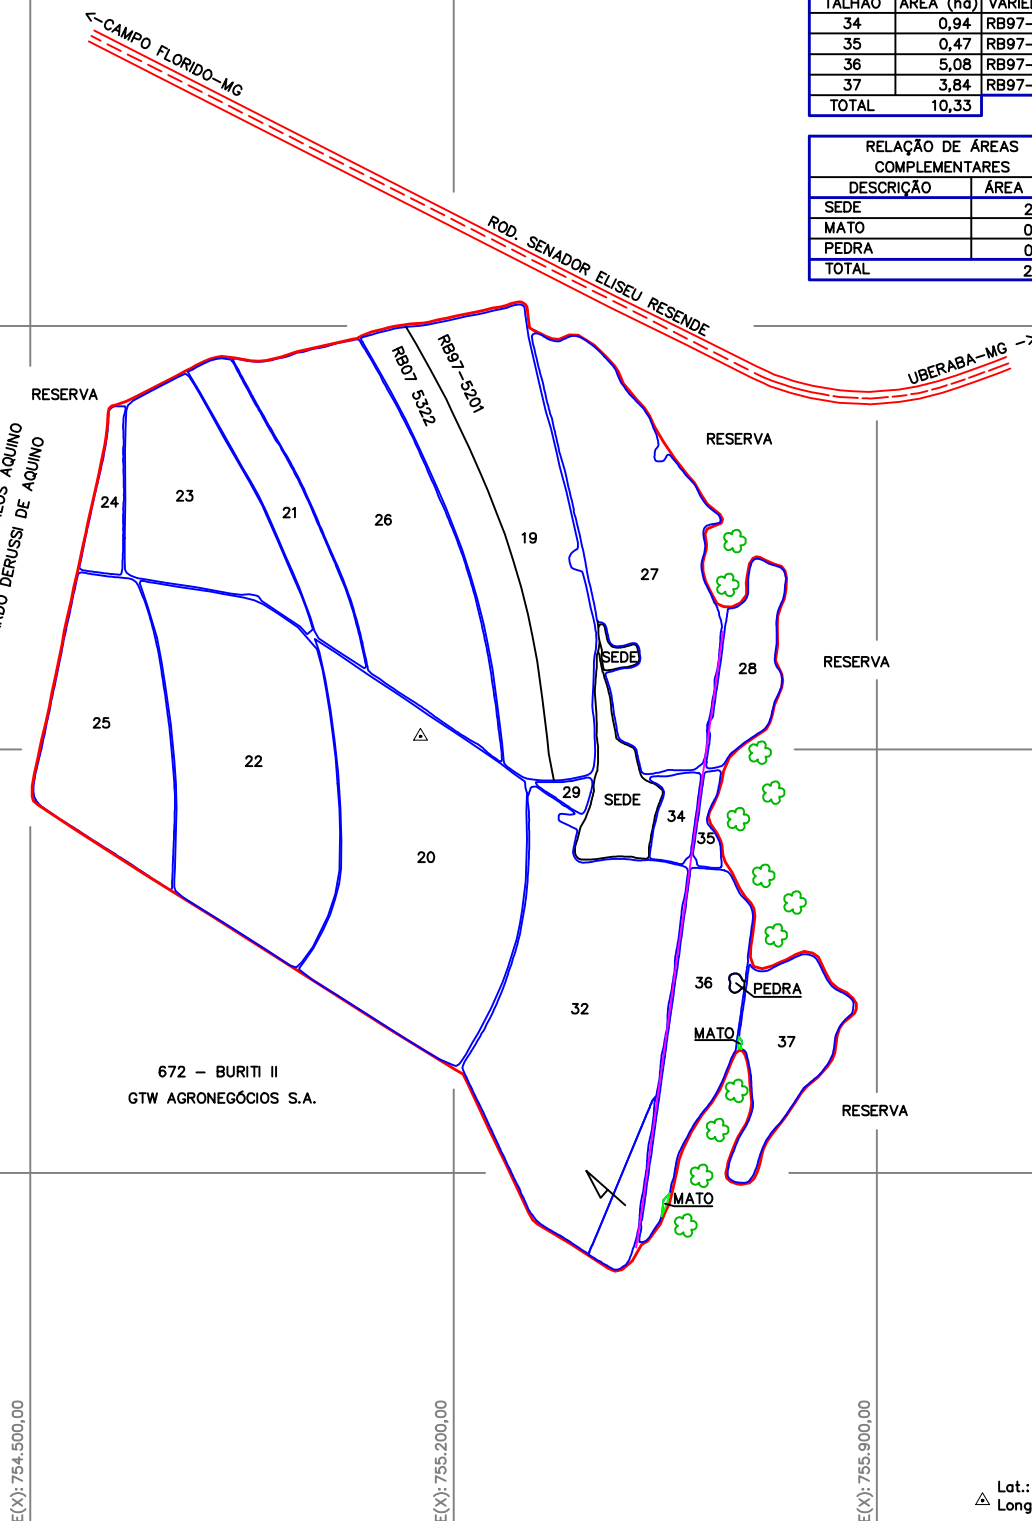

Lat.: 19°46'57.951"S
Long.: 48°33'53.195"E

 Fila Campo Florido	PROPRIEDADE: 382 – PALMEIRAS	QUADRO DE ÁREAS (ha)	CANA 2026:	15,18	Desenhado por: GLAUBER PIMENTEL	Data: 11/05/2026	Núcleo: 02 CAMPO FLORIDO
	PROPRIETÁRIO: JAIR DAVANÇO		CARREADOR 2026:	0,85	Revisado por:	Data:	
	FORNECEDOR: ALMERITA DA CONCEIÇÃO ROCHA XAVIER		CANA ANTIGA:	107,22	Responsável técnico: DANIEL CÉSAR DA SILVA		
	LEVANTAMENTO TOPOGRÁFICO		ÁREA TOTAL: 129,15 Hectares	CARREADOR ANTIGO:	3,36	Município: CAMPO FLORIDO-MG	Escala: 1 : 12.500
COMPLEMENTARES:				2,54			