


RELAÇÃO DE ÁREAS – CANA 2026			
TALHÃO	ÁREA (ha)	VARIETADE	DATA PL
18	7,01	RB12-7825	04/04/26
19	0,23	RB12-7825	04/04/26
TOTAL		7,24	

RELAÇÃO DE ÁREAS – CANA ANTIGA			
TALHÃO	ÁREA (ha)	VARIETADE	DATA PL
01	8,52	RB 03-6152	18/04/21
02	24,09	RB 03-6152	18/04/21
03	41,93	RB03-6152	01/05/25
04	24,80	RB03-6152	01/05/25
05	20,80	RB 03-6152	18/04/21
06	9,85	RB 03-6152	18/04/21
08	7,93	RB03-6152	01/05/25
09	13,77	RB03-6152	01/05/25
10	11,36	RB03-6152	01/05/25
11	7,69	RB03-6152	01/05/25
12	48,15	RB03-6152	01/05/25
13	26,30	RB03-6152	01/05/25
14	10,08	RB03-6152	01/05/25
15	41,28	RB03-6152	01/05/25
16	16,35	RB03-6152	01/05/25
17	18,16	RB03-6152	01/05/25
TOTAL		331,06	

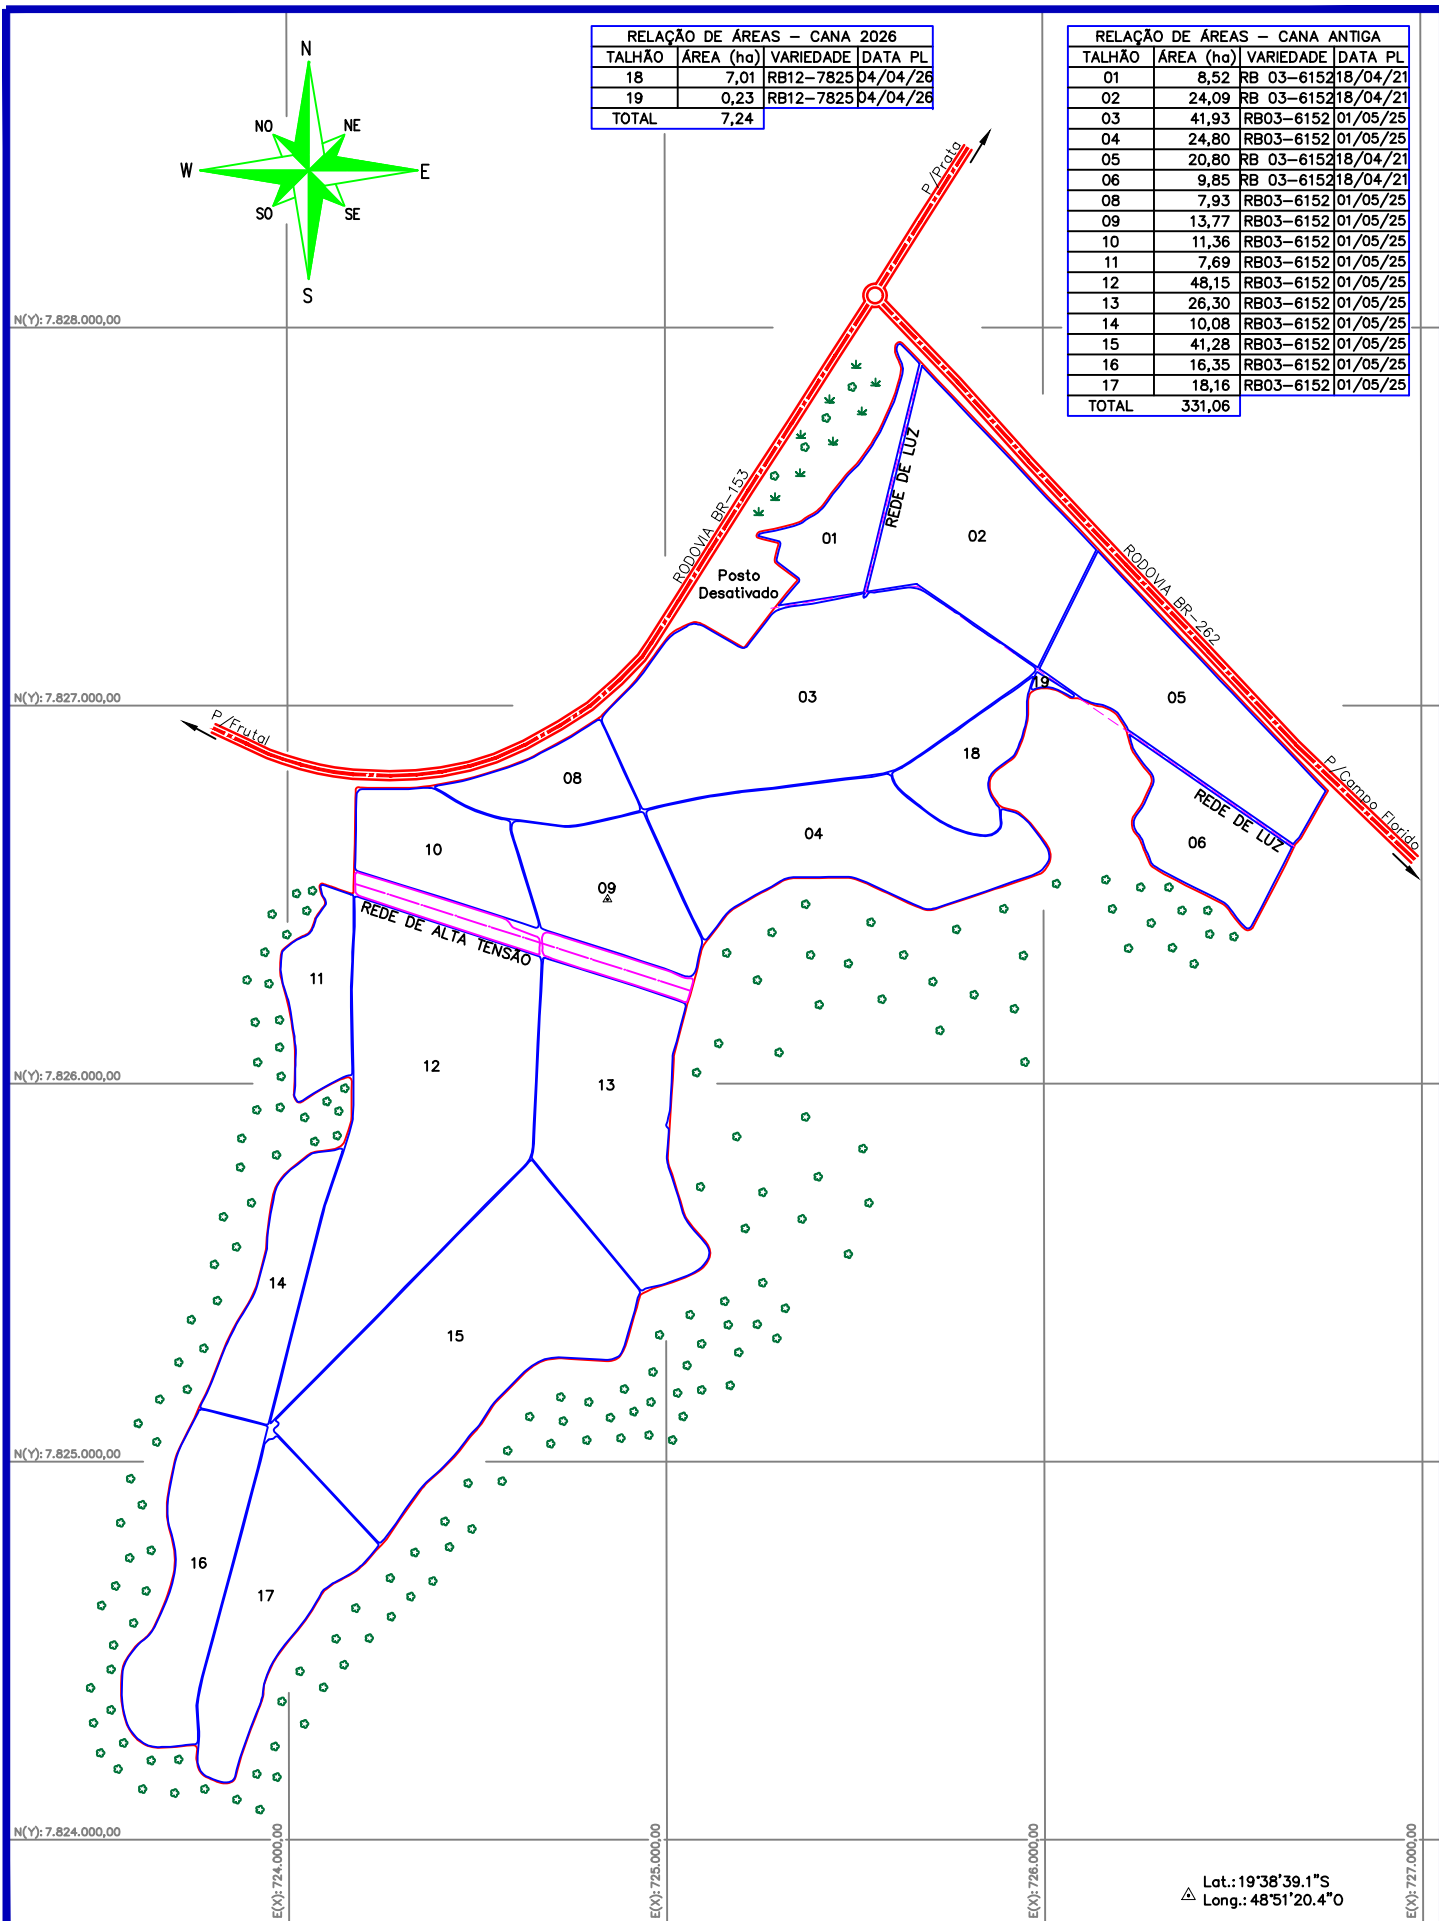

Lat.: 19°38'39.1"S
Long.: 48°51'20.4"W

 USINA CORUMPE Filial Campo Florido	PROPRIEDADE: 1051 –BOA SORTE	QUADRO DE ÁREAS (ha)	CANA 2026:	7,24	Atualizado por: MÁRCIO GALASSI	Data: 20/05/2026	Núcleo: 4 SANTA CLARA
	PROPRIETÁRIO: FELIPE MIGUEL RONCARATTI CURI		CARREADOR 2026:	0,19	Revisado por: —	Data: —	
	FORNECEDOR: FELIPE DE BRITO BRUNOZZI		CANA ANTIGA:	331,06	Engenheiro Agrimensor: DANIEL CÉSAR DA SILVA		
	ÁREA TOTAL: 353,26 Hectares		CARREADOR ANTIGO:	9,18			
LEVANTAMENTO TOPOGRÁFICO			REDE DE ALTA TENSÃO:	5,59	Município: CAMPO FLORIDO	Escala: 1 : 20.000	Data Levant.: 05/2026

Datum Sirgas2000 / UTM zona 22S (CM 51W)