


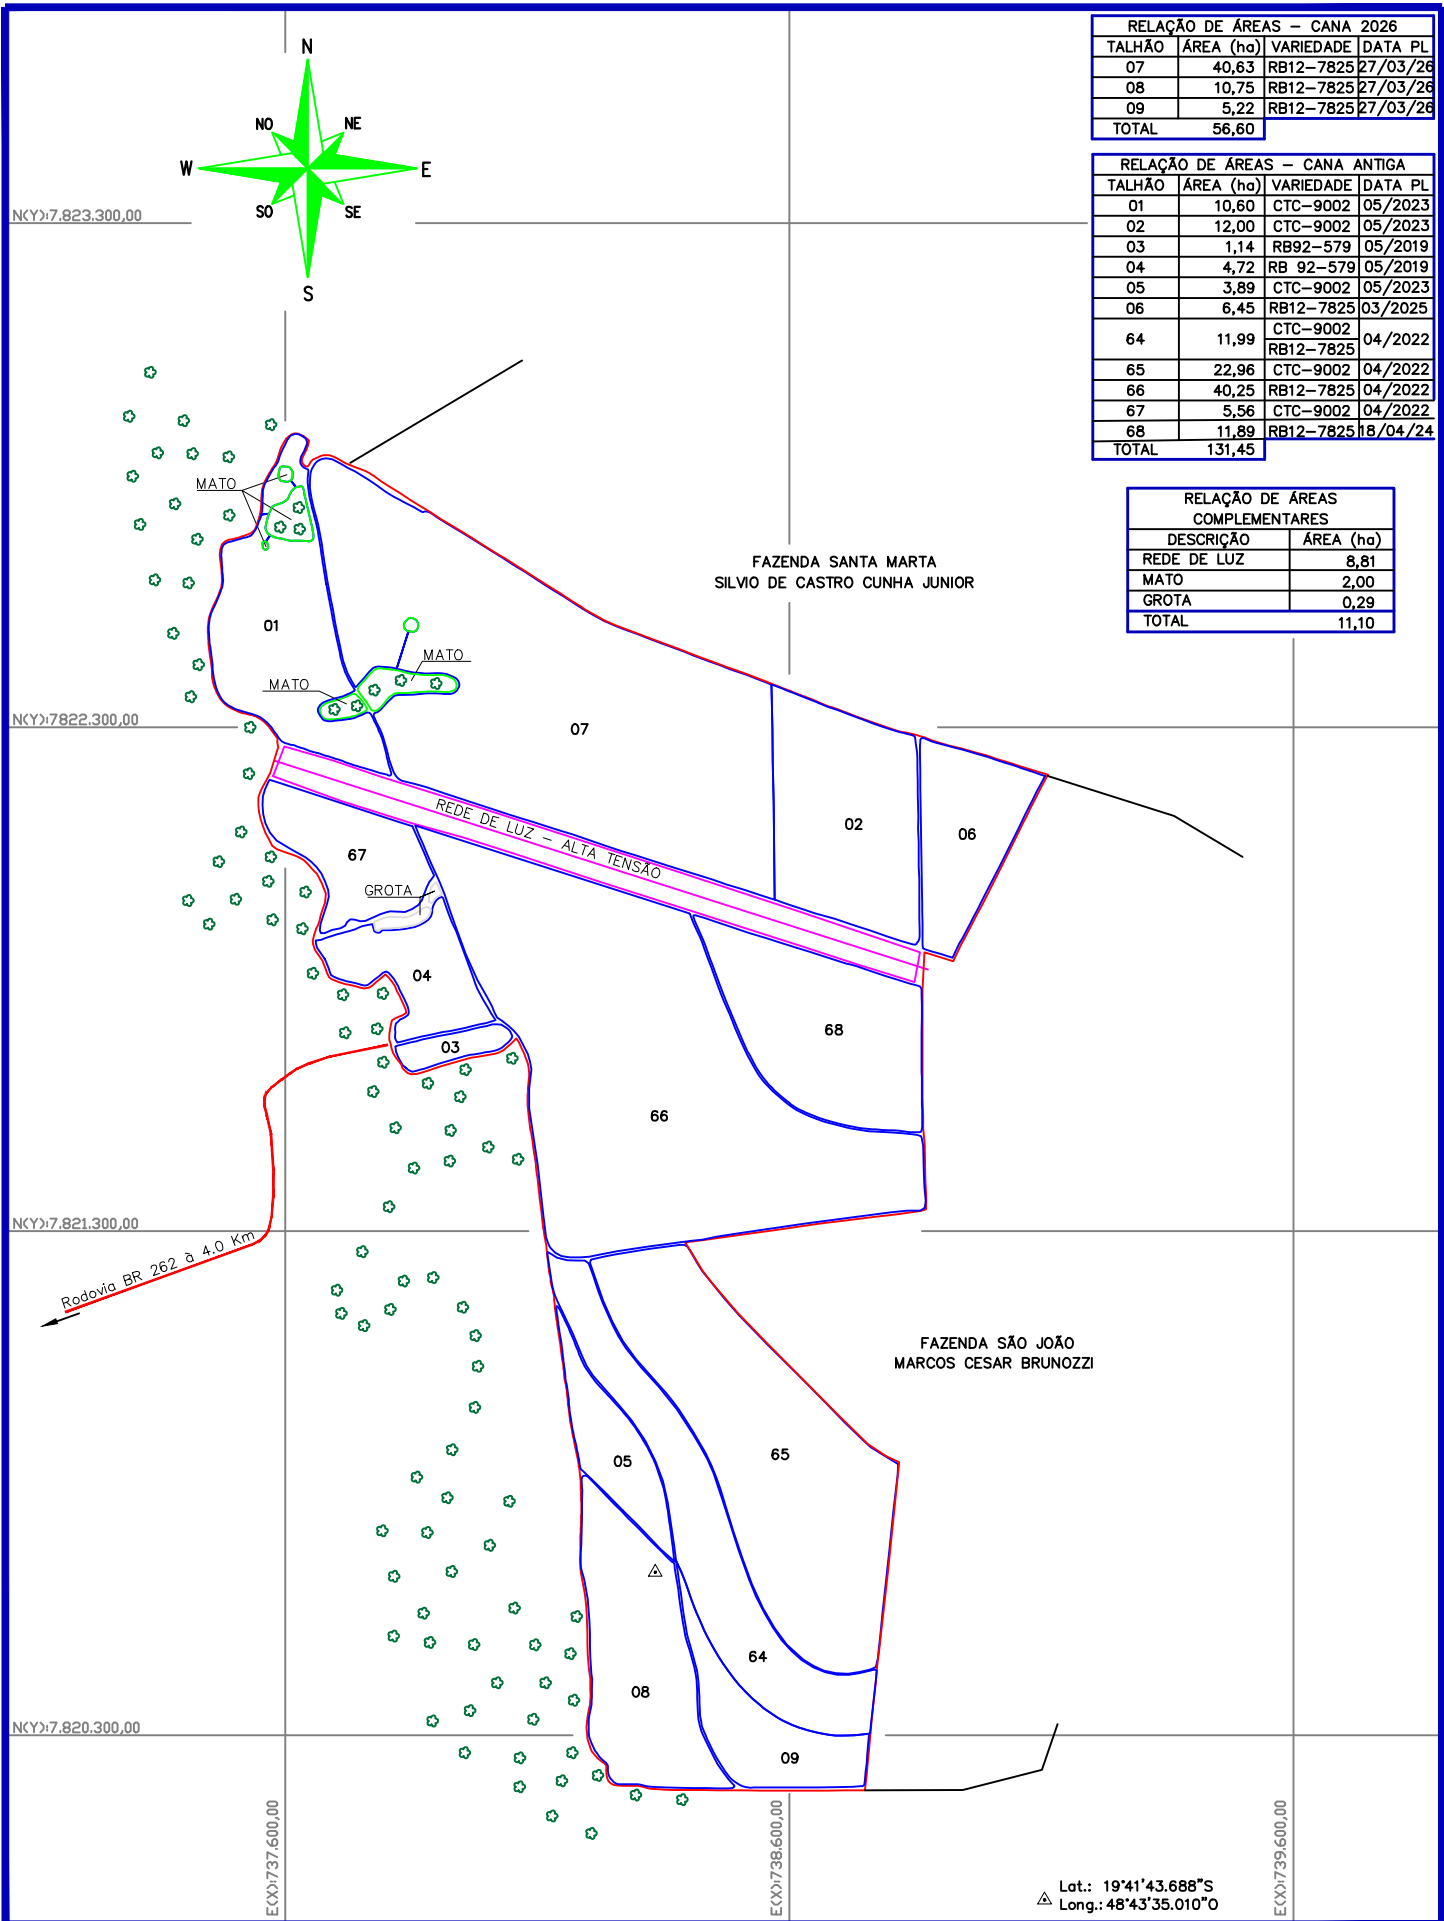

RELAÇÃO DE ÁREAS - CANA 2026			
TALHÃO	ÁREA (ha)	VARIEDADE	DATA PL
07	40,63	RB12-7825	27/03/26
08	10,75	RB12-7825	27/03/26
09	5,22	RB12-7825	27/03/26
TOTAL	56,60		

RELAÇÃO DE ÁREAS - CANA ANTIGA			
TALHÃO	ÁREA (ha)	VARIEDADE	DATA PL
01	10,60	CTC-9002	05/2023
02	12,00	CTC-9002	05/2023
03	1,14	RB92-579	05/2019
04	4,72	RB 92-579	05/2019
05	3,89	CTC-9002	05/2023
06	6,45	RB12-7825	03/2025
64	11,99	CTC-9002	04/2022
65	22,96	CTC-9002	04/2022
66	40,25	RB12-7825	04/2022
67	5,56	CTC-9002	04/2022
68	11,89	RB12-7825	18/04/24
TOTAL	131,45		

RELAÇÃO DE ÁREAS COMPLEMENTARES	
DESCRIÇÃO	ÁREA (ha)
REDE DE LUZ	8,81
MATO	2,00
GROTA	0,29
TOTAL	11,10

 USINA CORUPIPE Filial Campo Florido	PROPRIEDADE: 1139 – SÃO JOÃO	QUADRO DE ÁREAS (ha)	CANA 2026:	56,60	Desenhado por: MÁRCIO GALASSI	Data: 19/05/2026	Núcleo: 1 USINA	
	PROPRIETÁRIO: ANA LUIZA BRUNHEIRA BRUNOZZI		CARREADOR 2026:	1,69	Revisado por: —	Data: —		
	FORNECEDOR: MARCOS CESAR BRUNOZZI E OUTROS		CANA ANTIGA:	131,45	Engenheiro Agrimensor: DANIEL CÉSAR DA SILVA			
	LEVANTAMENTO TOPOGRÁFICO		ÁREA TOTAL: 206,29 Hectares	CARREADOR ANTIGO:	5,45	Município: CAMPO FLORIDO—MG		
				COMPLEMENTARES:	11,10	Escala: 1 : 15.000	Data Levant.: 05/2026	