


N(Y): 7.828.000,00

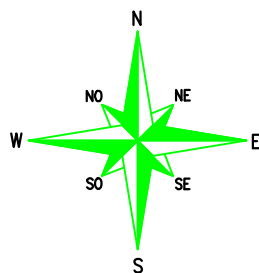


N(Y): 7.827.000,00

N(Y): 7.826.000,00

N(Y): 7.825.000,00

N(Y): 7.824.000,00

ASSENTAMENTO BRANCA MOURA
Instituto Nacional de Colonização e Reforma
Agrária - INCRA

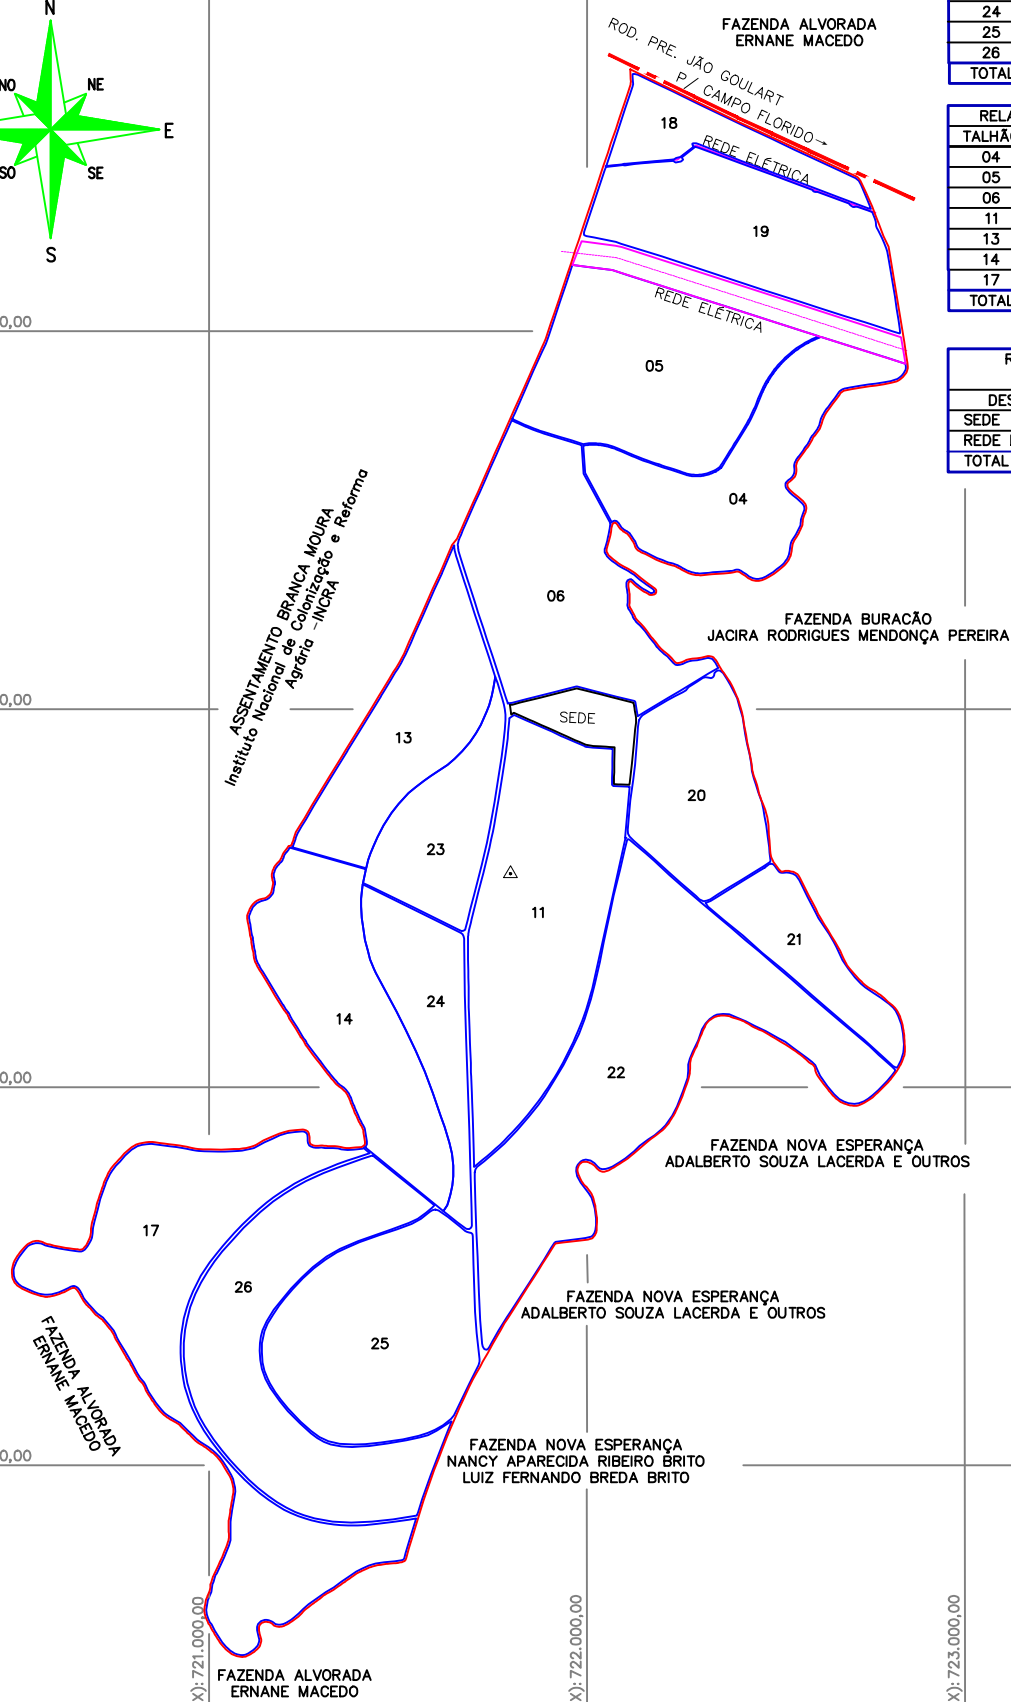

RELAÇÃO DE ÁREAS -- CANA 2026			
TALHÃO	ÁREA (ha)	VARIEDADE	DATA PL
18	7,67	RB 12-7825	21/04/26
19	22,16	RB 12-7825	21/04/26
20	15,82	RB 12-7825	21/04/26
21	8,99	RB 12-7825	21/04/26
22	42,63	RB 12-7825	21/04/26
23	11,57	RB 12-7825	21/04/26
24	11,50	RB 12-7825	21/04/26
25	26,33	RB 12-7825	21/04/26
26	29,29	RB 12-7825	21/04/26
TOTAL	175,96		

RELAÇÃO DE ÁREAS -- CANA 2020			
TALHÃO	ÁREA (ha)	VARIEDADE	DATA PL
04	20,55	RB 96-6928	09/03/20
05	26,46	RB 96-6928	09/03/20
06	26,76	RB 96-6928	09/03/20
11	32,20	RB 96-6928	09/03/20
13	17,13	RB 12-7825	21/04/26
14	22,27	RB 85-5156	09/03/20
17	36,12	RB 85-5156	09/03/20
TOTAL	181,49		

RELAÇÃO DE ÁREAS COMPLEMENTARES	
DESCRIÇÃO	ÁREA (ha)
SEDE	3,86
REDE DE LUZ	6,87
TOTAL	10,73

E(X): 721.000,00

E(X): 722.000,00

E(X): 723.000,00

Lat.: 19°39'9,97"S
 Δ Long.: 48°53'4,72"W



PROPRIEDADE:
1252 - FAZENDA UNIÃO - PEDRO MOSCHIAR
 PROPRIETÁRIO:
MARCOS CESAR BRUNOZZI
 FORNECEDOR:
MARCOS CESAR BRUNOZZI
 ÁREA TOTAL:
381,32

QUADRO DE ÁREAS
(ha)

CANA 2026:	175,96
CARREADORES 2026:	8,76
CANA ANTIGA:	181,49
CARREADORES ANTIGO:	4,38
COMPLEMENTARES:	10,73

Desenhado por:
GLAUBER PIMENTEL
 Atualizado por:
-
 Engenheiro Agrimensor:
DANIEL CESAR DA SILVA
 Município:
CAMPO FLORIDO

Data:
19/05/2026
 Data:
-
 Escala:
1 : 20.000

Núcleo:
4
SANTA CLARA
 Data Levant.:
18/05/2026

Obs.: Conferido perímetro georreferenciado.
 Datum Sirgas2000 / UTM zona 22S (CM 51W)