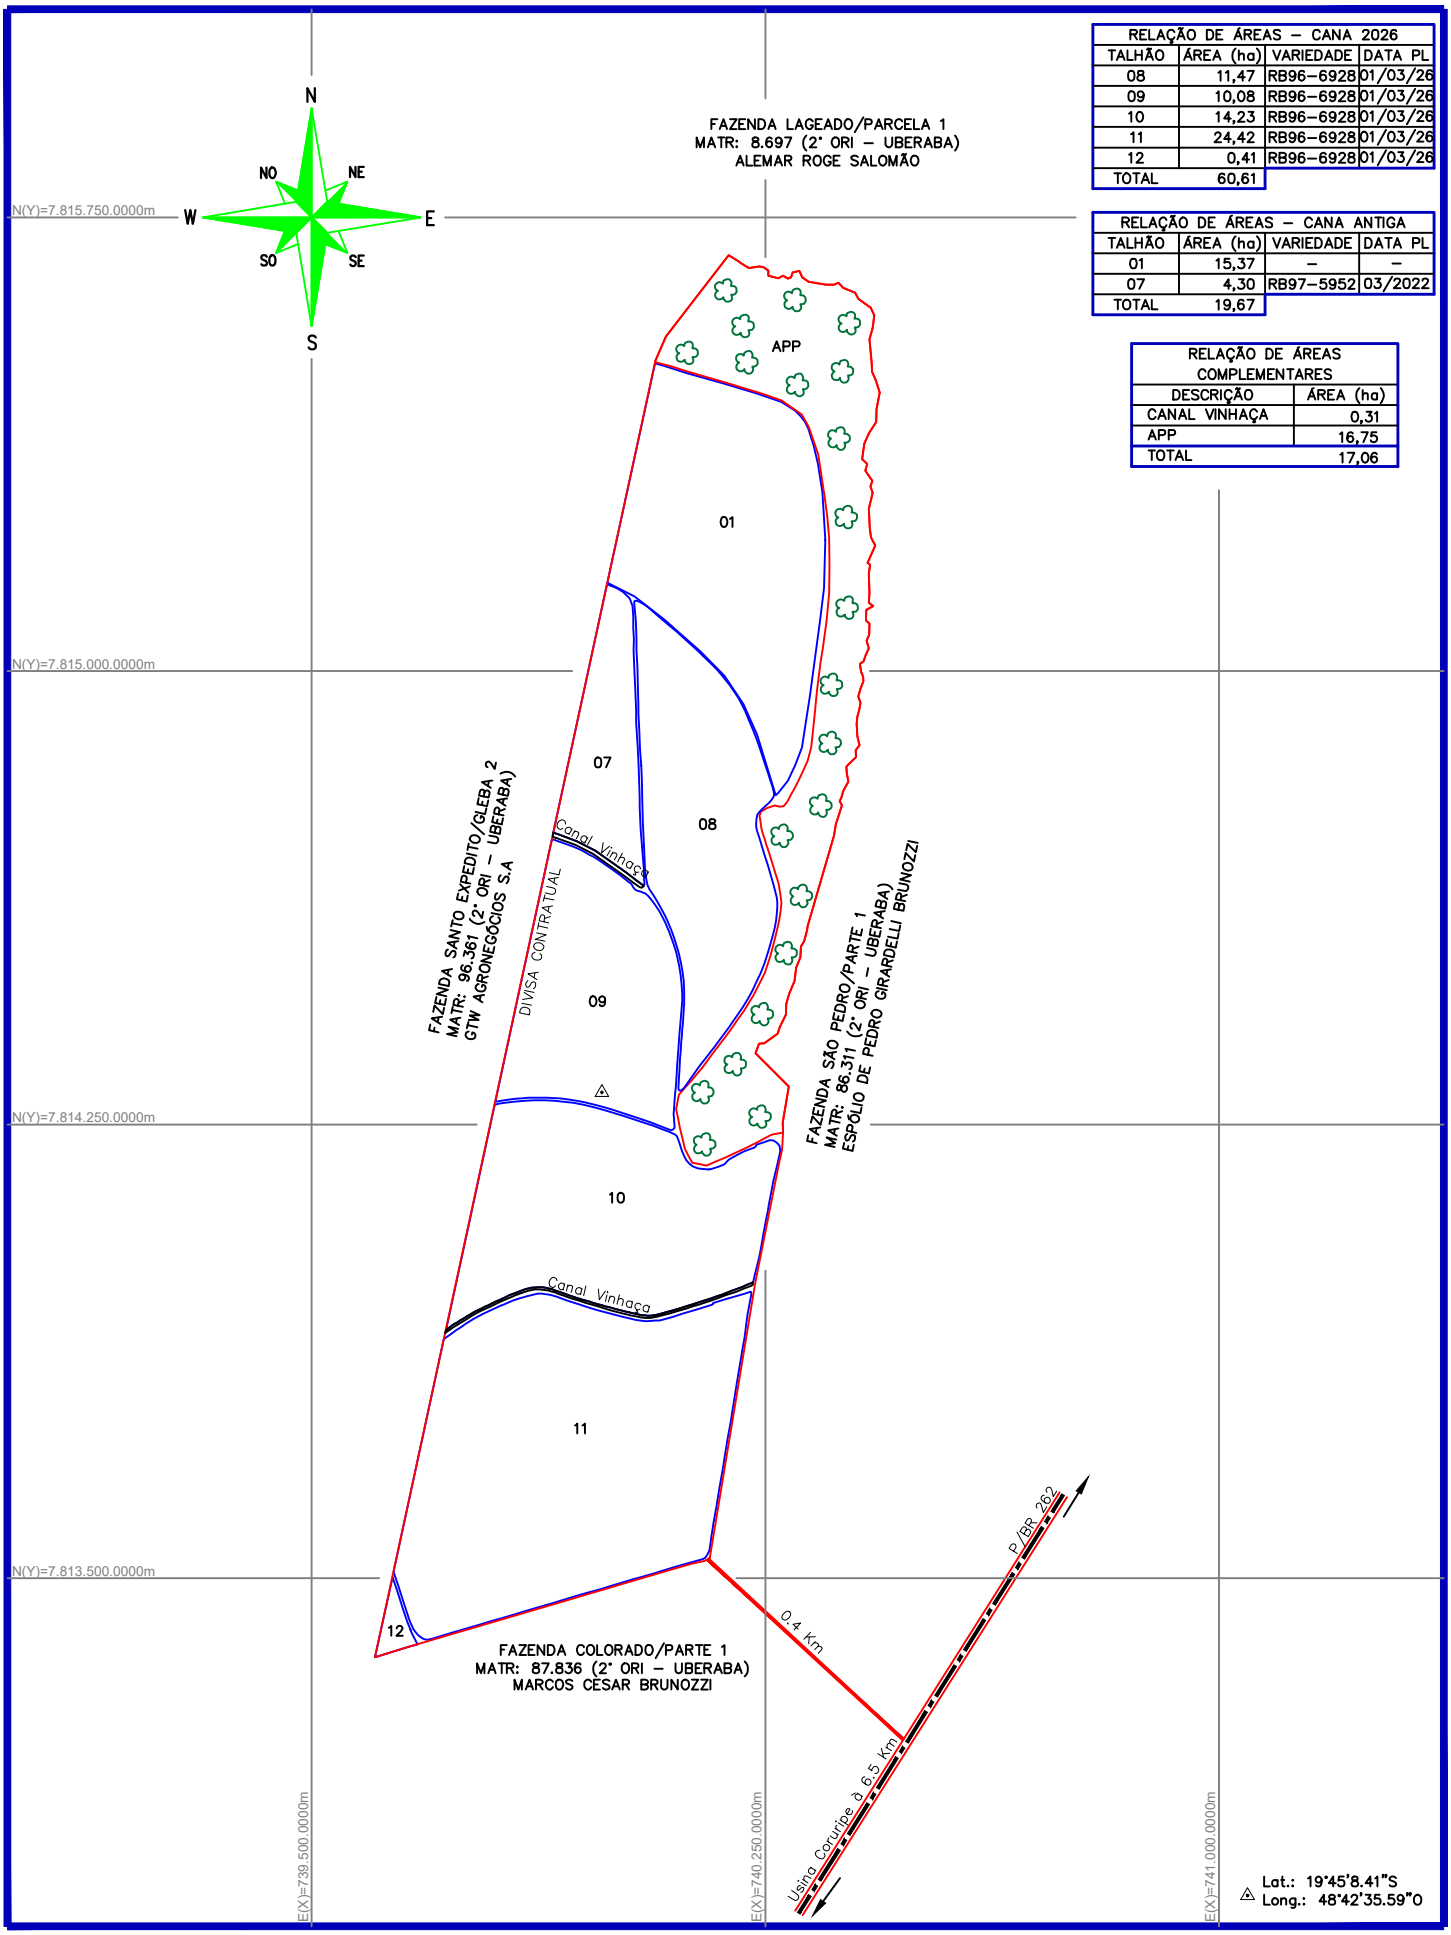

RELAÇÃO DE ÁREAS – CANA 2026			
TALHÃO	ÁREA (ha)	VARIEDADE	DATA PL
08	11,47	RB96-6928	01/03/26
09	10,08	RB96-6928	01/03/26
10	14,23	RB96-6928	01/03/26
11	24,42	RB96-6928	01/03/26
12	0,41	RB96-6928	01/03/26
TOTAL	60,61		

RELAÇÃO DE ÁREAS – CANA ANTIGA			
TALHÃO	ÁREA (ha)	VARIEDADE	DATA PL
01	15,37	–	–
07	4,30	RB97-5952	03/2022
TOTAL	19,67		

RELAÇÃO DE ÁREAS COMPLEMENTARES	
DESCRIÇÃO	ÁREA (ha)
CANAL VINHAÇA	0,31
APP	16,75
TOTAL	17,06

USINA CORURIPE
Filial Campo Florido

LEVANTAMENTO TOPOGRÁFICO

PROPRIEDADE: 1259 – SANTO EXPEDITO – GLEBA SÃO JOÃO II
PROPRIETÁRIO: MGV PARTICIPAÇÕES E EMPREENDIMENTOS
FORNECEDOR: FELIPE DE BRITO BRUNOZZI
ÁREA TOTAL: 99,88 Hectares

QUADRO DE ÁREAS (ha)

CANA 2026:	60,61
CARREADOR 2026:	1,51
CANA ANTIGA:	19,67
CARREADOR ANTIGO:	1,03
COMPLEMENTARES:	17,06

Desenhado por: MÁRCIO GALASSI | Data: 11/05/2026
Atualizado por: – | Data: –
Engenheiro Agrimensor: DANIEL CÉSAR DA SILVA
Município: CAMPO FLORIDO–MG | Escala: 1 : 12.500 | Data Levant.: 05/2026
Núcleo: 01 USINA

Datum Sirgas2000 / UTM zona 22S (CM 51W)