


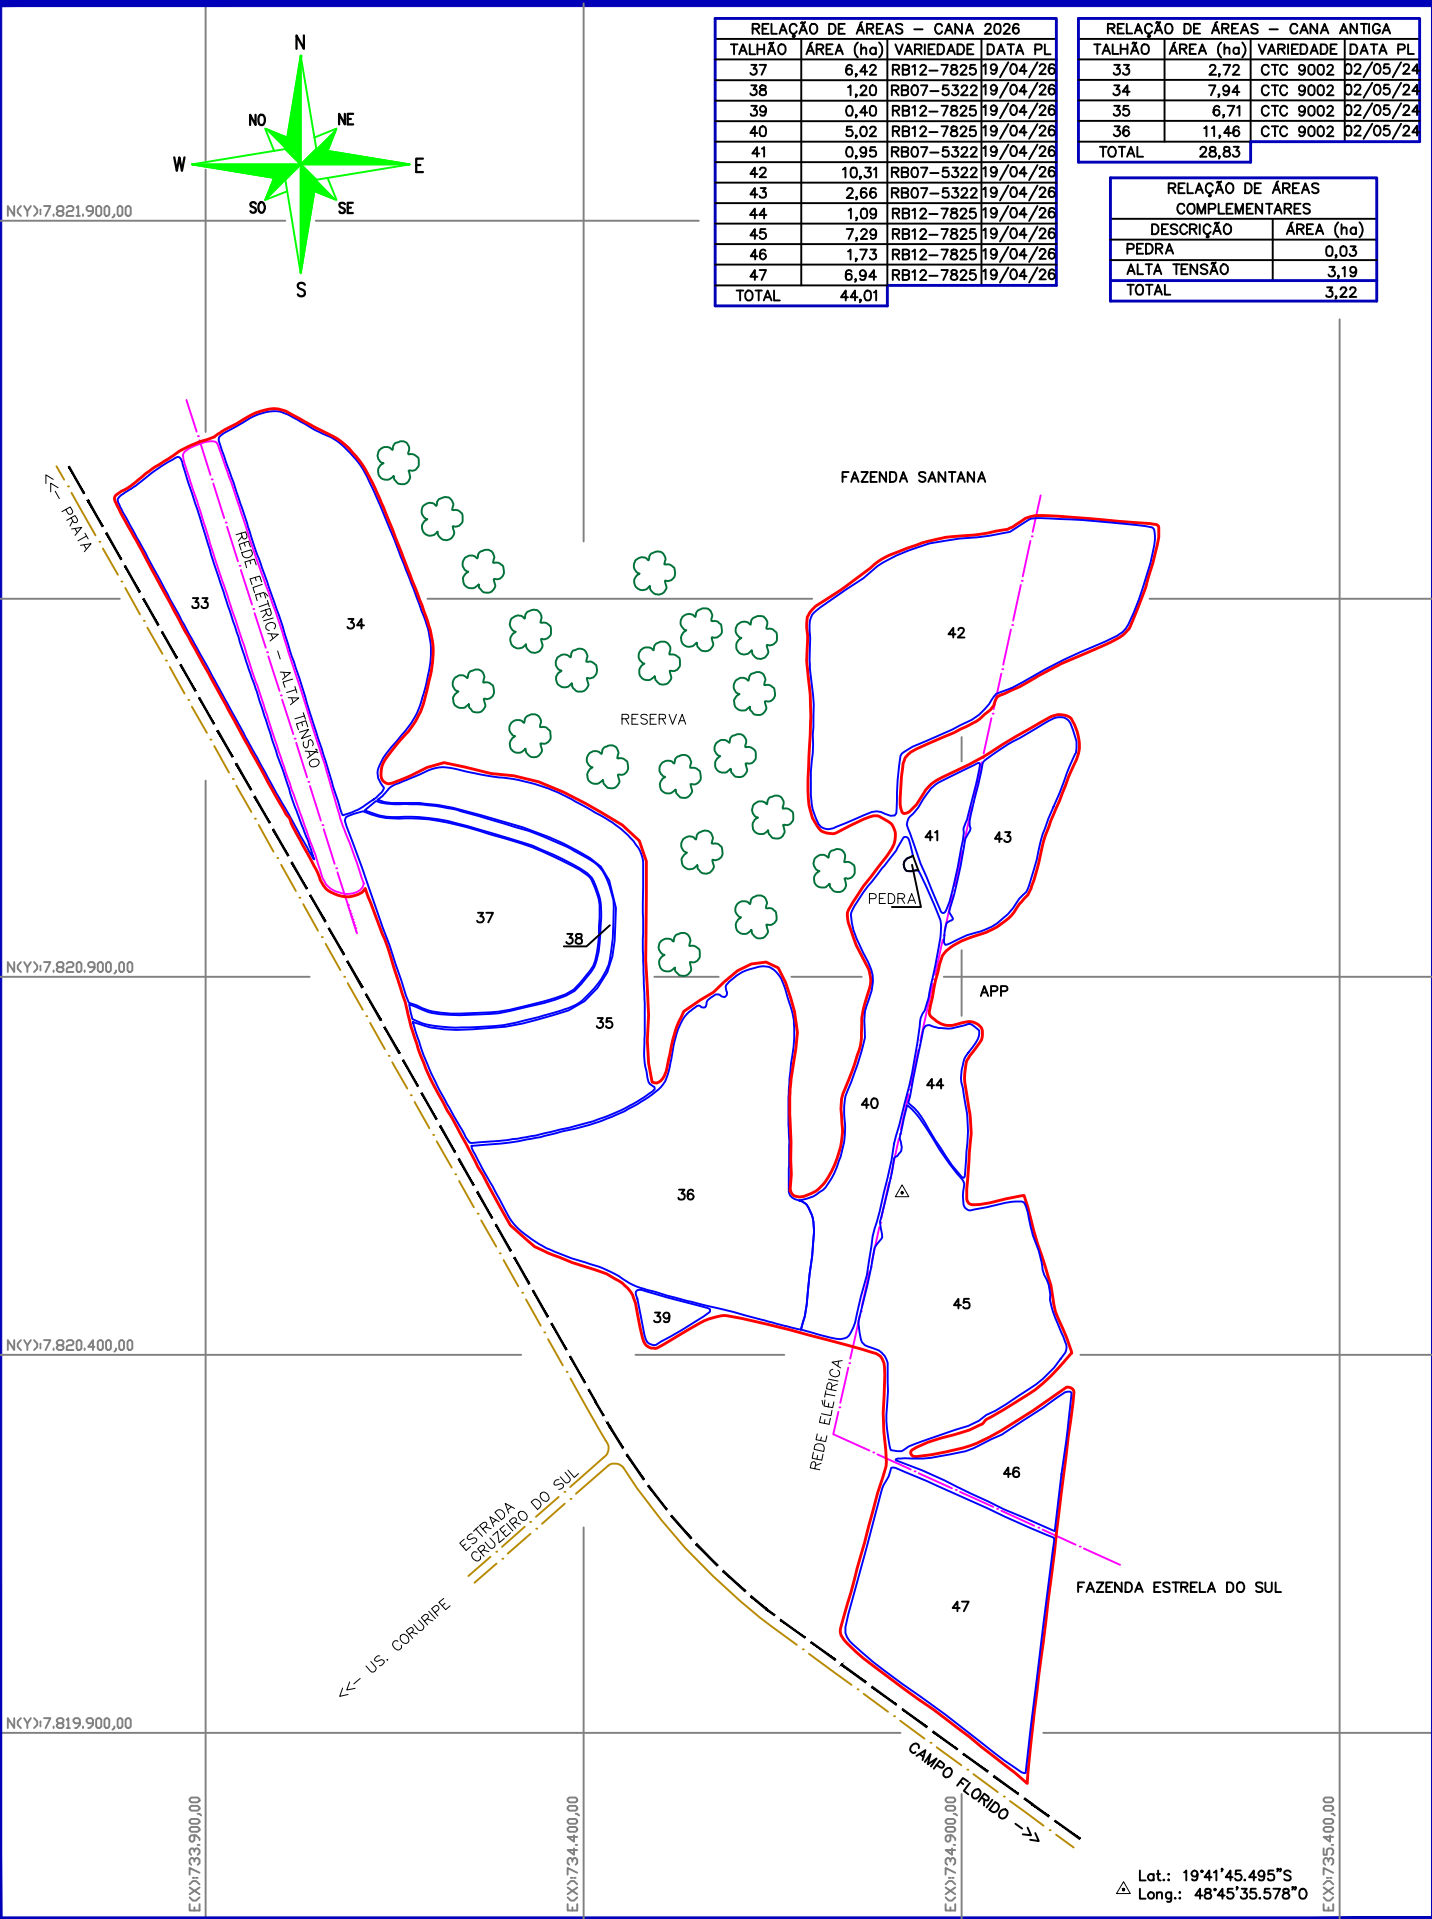

|   |                                                        |                         |                   |                 |                                                 |                       |       |                          |                           |  |
|---|--------------------------------------------------------|-------------------------|-------------------|-----------------|-------------------------------------------------|-----------------------|-------|--------------------------|---------------------------|--|
| <br>USINA<br>CORUPE<br>Filial Campo Florido | PROPRIEDADE:<br>490 – ESTRELA DO SUL                   | QUADRO DE ÁREAS<br>(ha) | CANA 2026:        | 44,01           | Desenhado por:                                  | MARCIO GALASSI        | Data: | 20/05/2026               | Núcleo:<br><br>1<br>USINA |  |
|   | PROPRIETÁRIO:<br>CARVALHO & SOUZA PARTICIPAÇÕES E EMP. |                         | CARREADOR 2026:   | 3,17            | Revisado por:                                   |                       | Data: |                          |                           |  |
|   | FORNECEDOR:<br>MARCOS CESAR BRUNOZZI                   |                         | CANA ANTIGA:      | 28,83           | Engenheiro Agrimensor:<br>DANIEL CÉSAR DA SILVA |                       |       |                          |                           |  |
|   | ÁREA TOTAL:<br>81,10 Hectares                          |                         | CARREADOR ANTIGO: | 1,87            | Município:<br>CAMPO FLORIDO                     |                       |       |                          |                           |  |
|   | LEVANTAMENTO TOPOGRÁFICO                               |                         |                   | COMPLEMENTARES: | 3,22                                            | Escala:<br>1 : 10.000 |       | Data Levant.:<br>05/2026 |                           |  |