


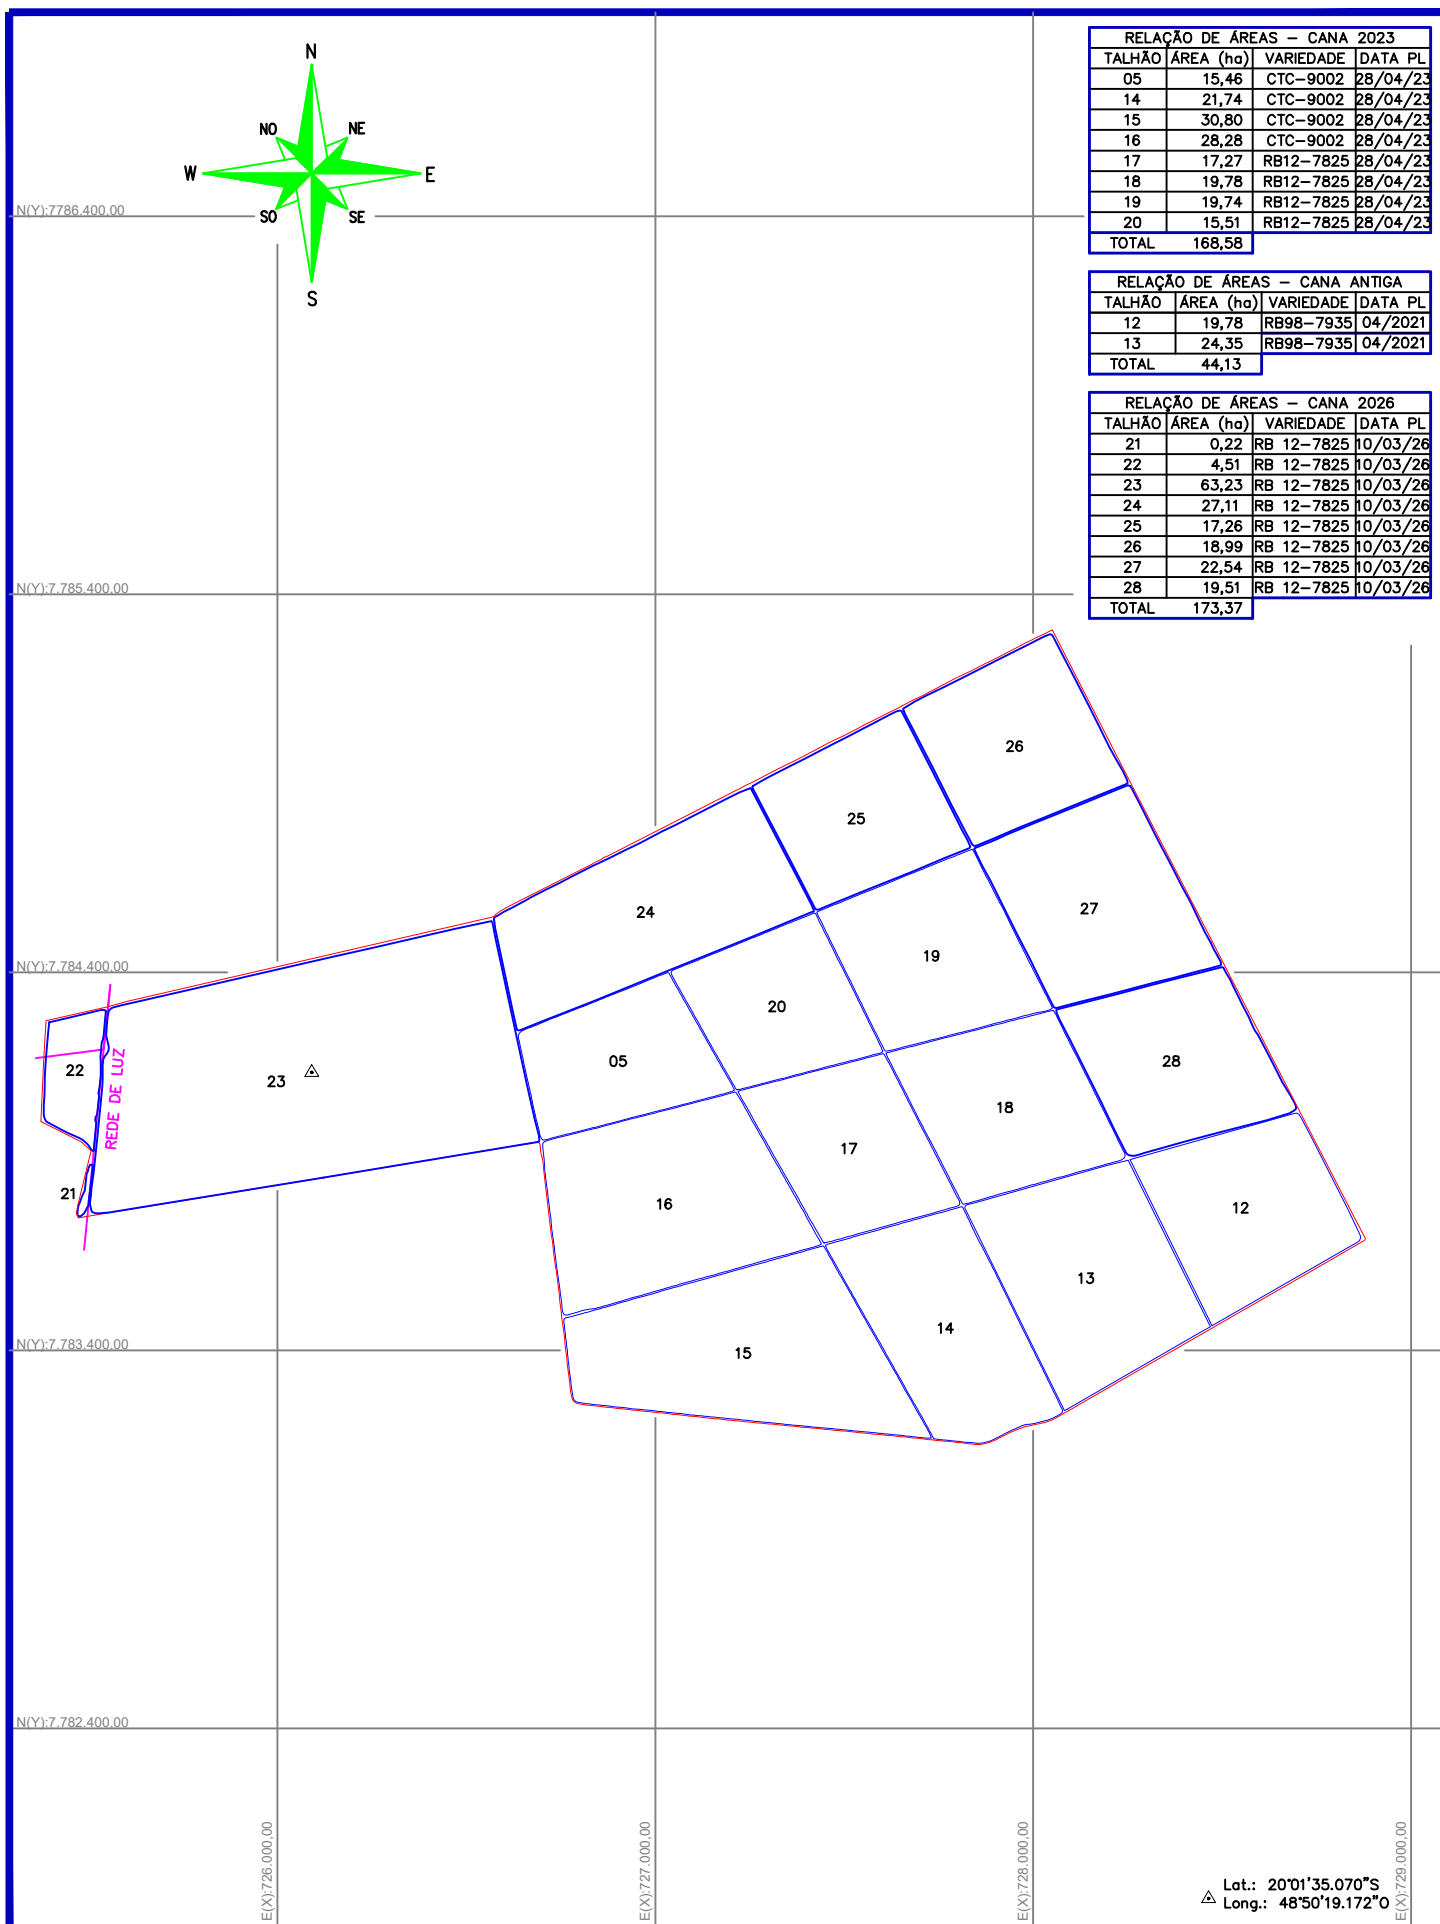

RELAÇÃO DE ÁREAS – CANA 2023			
TALHÃO	ÁREA (ha)	VARIETADE	DATA PL
05	15,46	CTC-9002	28/04/23
14	21,74	CTC-9002	28/04/23
15	30,80	CTC-9002	28/04/23
16	28,28	CTC-9002	28/04/23
17	17,27	RB12-7825	28/04/23
18	19,78	RB12-7825	28/04/23
19	19,74	RB12-7825	28/04/23
20	15,51	RB12-7825	28/04/23
TOTAL	168,58		

RELAÇÃO DE ÁREAS – CANA ANTIGA			
TALHÃO	ÁREA (ha)	VARIETADE	DATA PL
12	19,78	RB98-7935	04/2021
13	24,35	RB98-7935	04/2021
TOTAL	44,13		

RELAÇÃO DE ÁREAS – CANA 2026			
TALHÃO	ÁREA (ha)	VARIETADE	DATA PL
21	0,22	RB 12-7825	10/03/26
22	4,51	RB 12-7825	10/03/26
23	63,23	RB 12-7825	10/03/26
24	27,11	RB 12-7825	10/03/26
25	17,26	RB 12-7825	10/03/26
26	18,99	RB 12-7825	10/03/26
27	22,54	RB 12-7825	10/03/26
28	19,51	RB 12-7825	10/03/26
TOTAL	173,37		

 LEVANTAMENTO TOPOGRÁFICO	PROPRIEDADE: 494 – CONTELIVA	QUADRO DE ÁREAS (ha)	CANA 2026: 173,37	Desenhado por: ARTHUR VENANCIO	Data: 18/07/2023	Núcleo: 6 CONTELIVA
	PROPRIETÁRIO: VITOR WANDERLEY E FILHOS LTDA		CARREADOR 2026: 5,77	Atualizado por: -	Data: -	
	FORNECEDOR: MARCOS CÉSAR BRUNOZZI		CANA ANTIGA: 212,71	Eng. Agrimensor: DANIEL CÉSAR DA SILVA		
	ÁREA TOTAL: 395,82 Hectares		CARREADOR ANTIGO: 3,97	Município: FRUTAL – MG	Escala: 1 : 20.000	Data Levant.: 07/07/2023

Obs.: Conferido perímetro georreferenciado.
Datum Sirgas2000 / UTM zona 22S (CM 51W)