


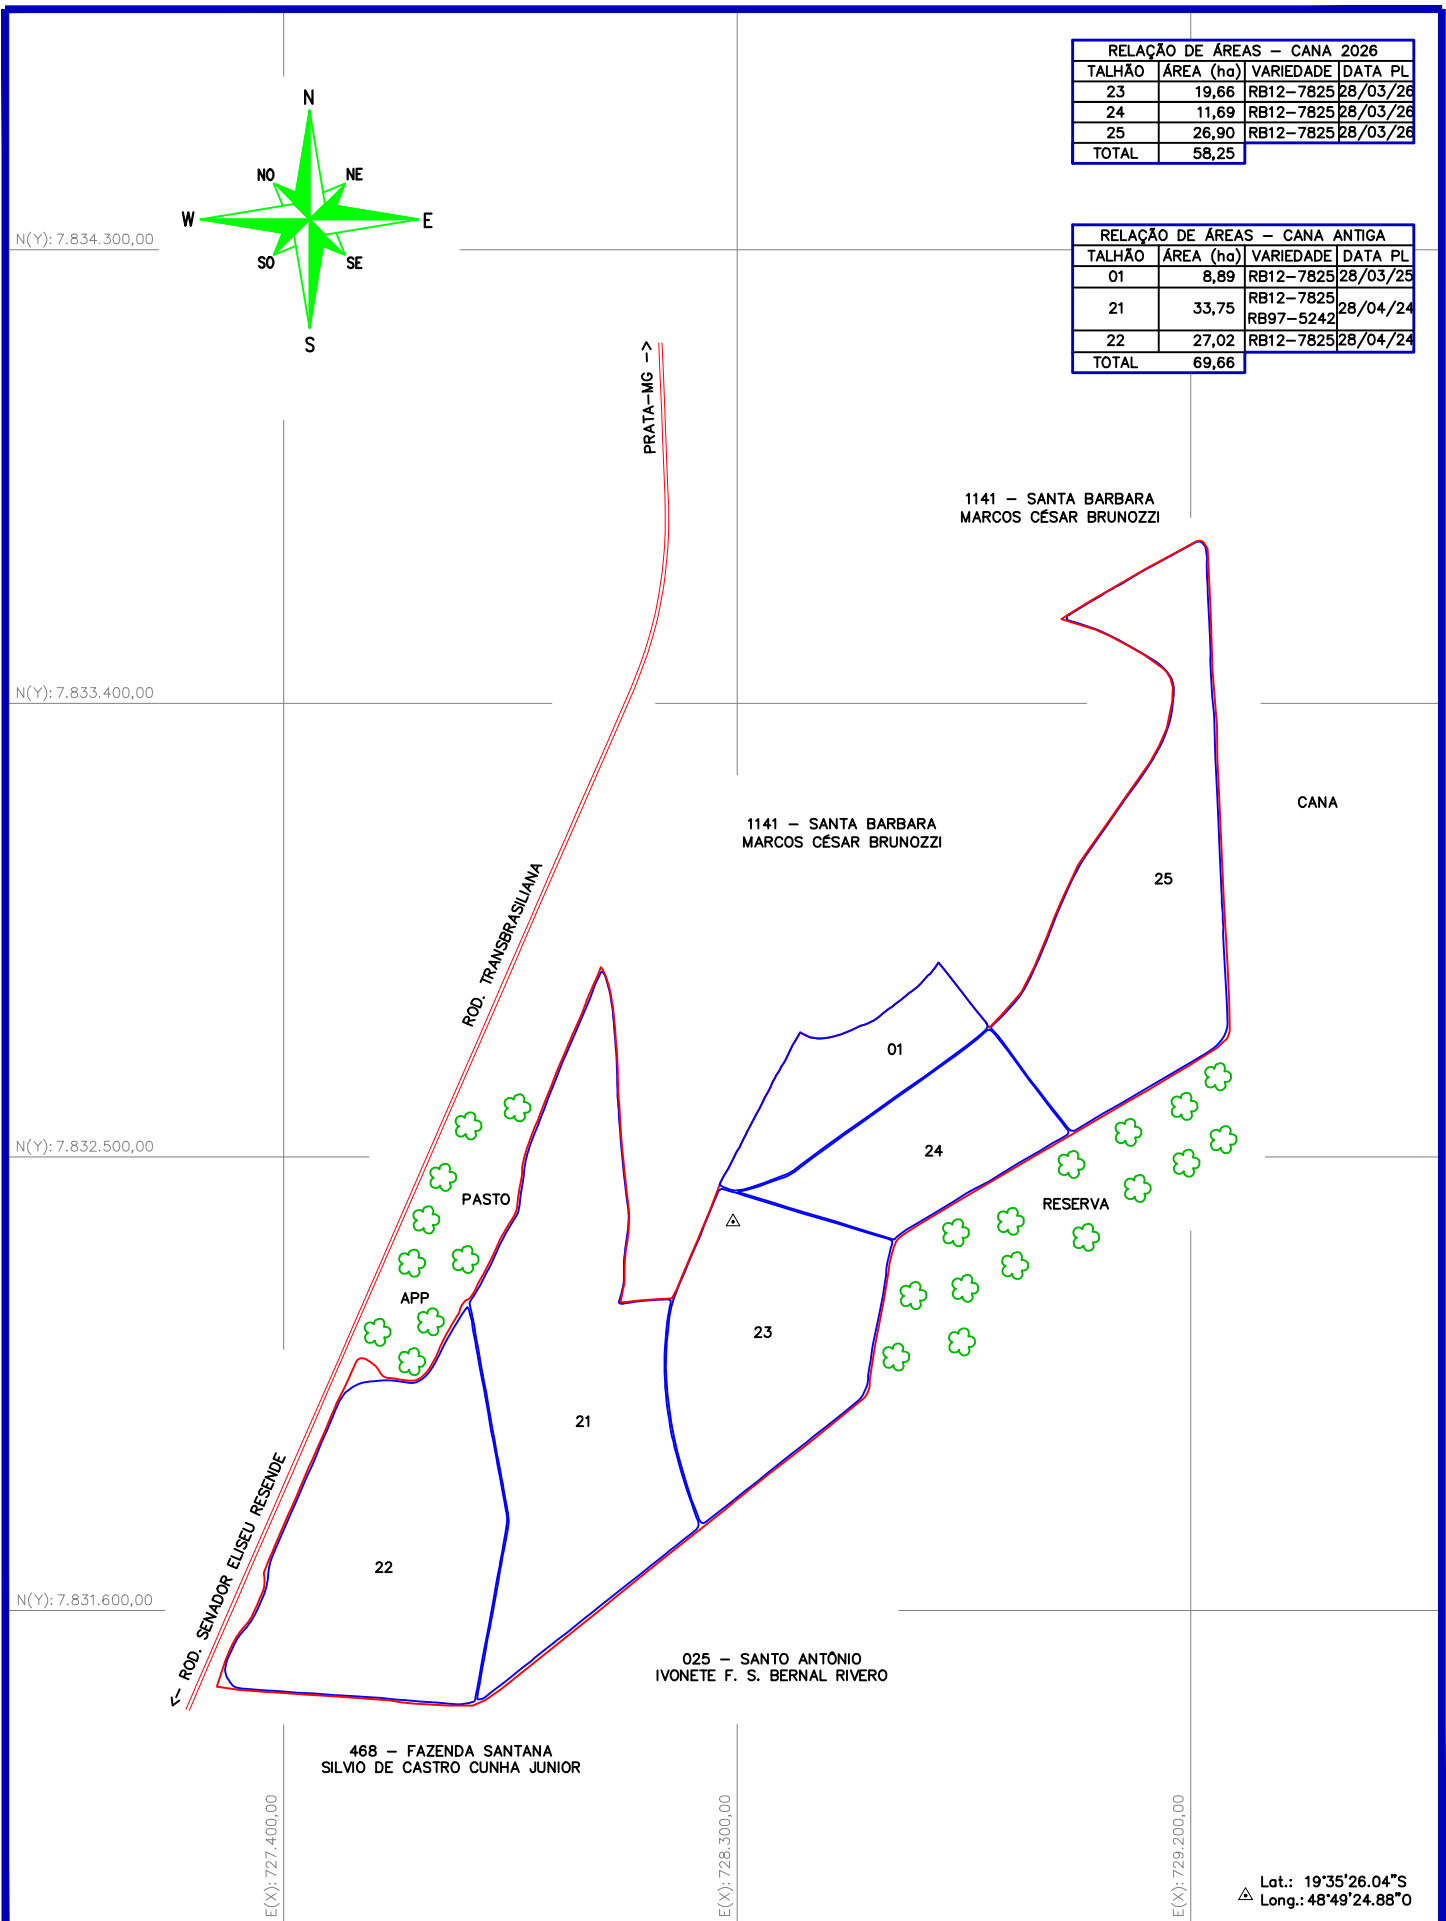

RELATÓRIO DE ÁREAS - CANA 2026			
TALHÃO	ÁREA (ha)	VARIEDADE	DATA PL
23	19,66	RB12-7825	28/03/26
24	11,69	RB12-7825	28/03/26
25	26,90	RB12-7825	28/03/26
TOTAL	58,25		

RELATÓRIO DE ÁREAS - CANA ANTIGA			
TALHÃO	ÁREA (ha)	VARIEDADE	DATA PL
01	8,89	RB12-7825	28/03/25
21	33,75	RB12-7825	28/04/24
22	27,02	RB97-5242	28/04/24
TOTAL	69,66		

 USINA CORUMPE Filial Campo Florido	PROPRIEDADE: 627 – SANTA BARBARA	QUADRO DE ÁREAS (ha)	CANA 2026:	58,25	Desenhado por: DOUGLAS WISTERSON	Data: 21/05/2026	Núcleo: 04 SANTA CLARA
	PROPRIETÁRIO: MARCOS CESAR BRUNOZZI		CARREADOR 2026:	1,84	Revisado por: —	Data: —	
	FORNECEDOR: MARCOS CESAR BRUNOZZI		CANA ANTIGA:	69,66	Engenheiro Agrimensor: DANIEL CÉSAR DA SILVA		
	ÁREA TOTAL: 131,58 Hectares		CARREADOR ANTIGO:	1,83	Município: PRATA—MG	Escala: 1 : 15.000	Data Levant.: 05/2026
LEVANTAMENTO TOPOGRÁFICO				COMPLEMENTARES:	—		