


N(Y)=7.791.800,00

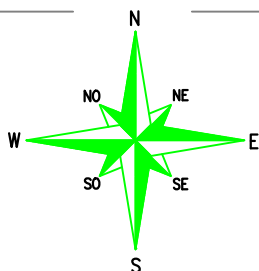

N(Y)=7.790.300,00

RELAÇÃO DE ÁREAS – CANA 2025			
TALHÃO	ÁREA (ha)	VARIEDADE	DATA PL
12	9,41	RB12-7825	01/04/25
13	22,00	RB12-7825	01/04/25
14	21,26	RB12-7825	01/04/25
15	24,70	RB12-7825	01/04/25
16	15,48	RB12-7825	01/04/25
17	5,93	RB12-7825	01/04/25
TOTAL	98,78		

RELAÇÃO DE ÁREAS – CANA 2026			
TALHÃO	ÁREA (ha)	VARIEDADE	DATA PL
61	31,25	RB 12-7825	11/04/26
62	21,77	RB 12-7825	11/04/26
63	16,16	RB 12-7825	11/04/26
64	7,47	RB 12-7825	11/04/26
65	37,38	RB 12-7825	11/04/26
66	33,43	RB 12-7825	11/04/26
TOTAL	147,46		


RELAÇÃO DE ÁREAS – CANA ANTIGA			
TALHÃO	ÁREA (ha)	VARIEDADE	DATA PL
01	33,03	RB98-7935	04/2021
05	10,99	RB98-7935	04/2021
06	25,09	RB98-7935	04/2021
07	27,48	RB98-7935	04/2021
08	3,95	RB98-7935	04/2021
09	25,55	CTC9002	03/05/23
10	36,55	CTC9002	03/05/23
11	6,30	CTC9002	03/05/23
19	1,07	COMPOSTAGEM	04/2021
22	3,88	CTC-9002	04/2021
27	17,28	RB85-5536	03/2019
28	33,69	CTC-9002	03/2019
31	7,84	RB86-7515	04/2020
34	19,26	RB86-7515	03/2019
35	17,61	RB86-7515	03/2019
43	15,74	RB86-7515	03/2019
44	17,27	RB86-7515	03/2019
47	7,04	RB86-7515	04/2020
48	21,88	RB86-7515	03/2019
49	21,75	RB86-7515	03/2019
52	21,95	RB86-7515	04/2020
53	16,90	RB86-7515	04/2020
54	12,46	RB12-7815	04/2022
55	25,53	CTC-9001	04/2022
56	21,14	CTC-9002	04/2022
57	14,80	CTC-9002	04/2022
TOTAL	466,03		

N(Y)=7.788.800,00

N(Y)=7.787.300,00

N(Y)=7.785.800,00

N(Y)=7.784.300,00

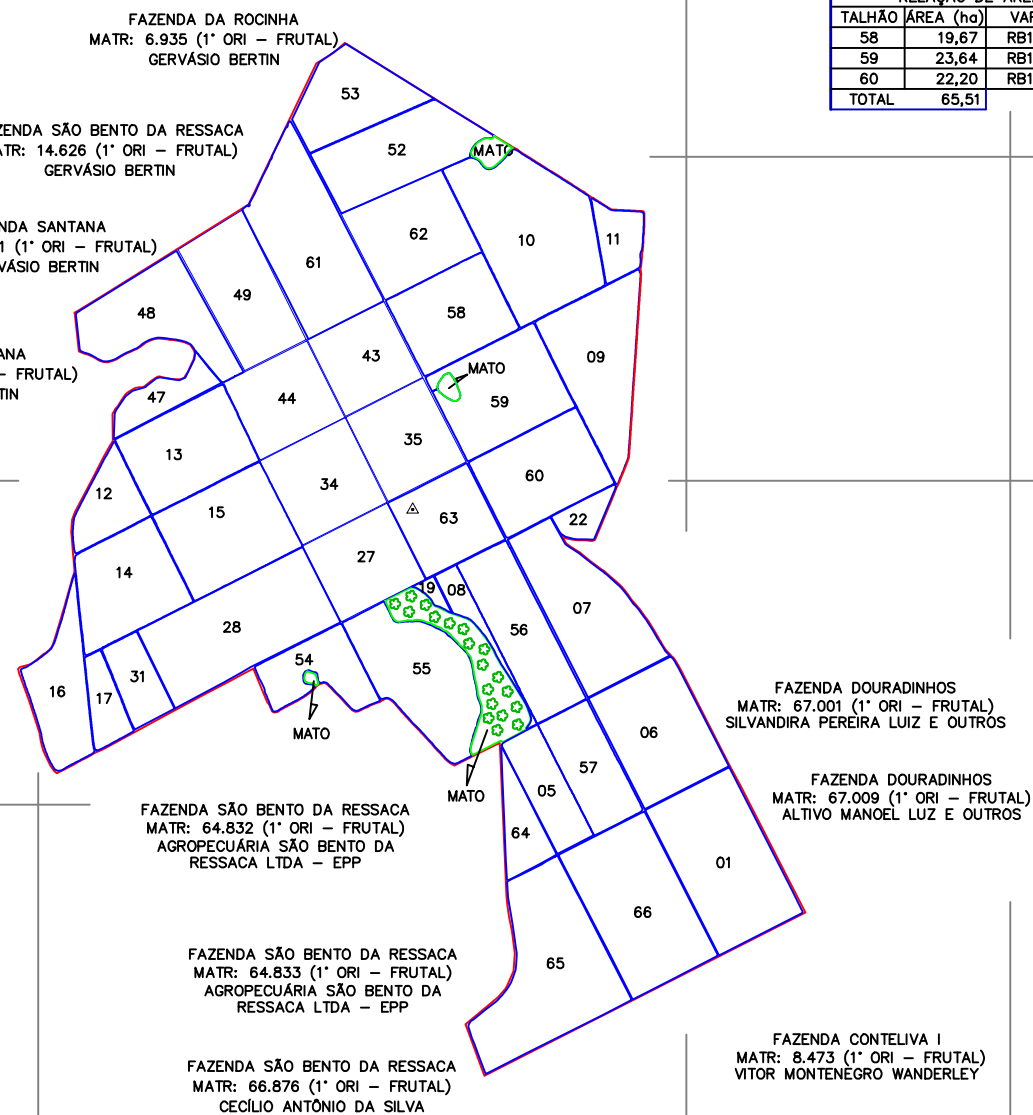

RELAÇÃO DE ÁREAS – CANA 2024			
TALHÃO	ÁREA (ha)	VARIEDADE	DATA PL
58	19,67	RB12-7825	07/03/24
59	23,64	RB12-7825	07/03/24
60	22,20	RB12-7825	07/03/24
TOTAL	65,51		

E(X)=724.500,00

Lat.: 19°59'56.501"S
Δ Long.: 48°50'15.619"O

PROPRIEDADE:
653 – CONTELIVA

PROPRIETÁRIO:
VITOR WANDERLEY E FILHOS LTDA

FORNECEDOR:
MARCOS CESAR BRUNOZZI E OUTROS

ÁREA TOTAL:
815,71 Hectares

QUADRO DE ÁREAS
(ha)

CANA 2026:	147,46
CARREADOR 2026:	5,58
CANA ANTIGA:	630,32
CARREADOR ANTIGO:	16,10
MATO:	16,25

Desenhado por:
YGOR DOS SANTOS

Revisado por:
-

Engenheiro Agrimensor:
DANIEL CESAR DA SILVA

Município:
FRUTAL – MG

Data:
16/06/25

Data:
-

Escala:
1 : 35.000

Data Levant.:
12/06/25

Núcleo:
6 CONTELIVA

Datum Sirgas2000 / UTM zona 22S (CM 51W)