


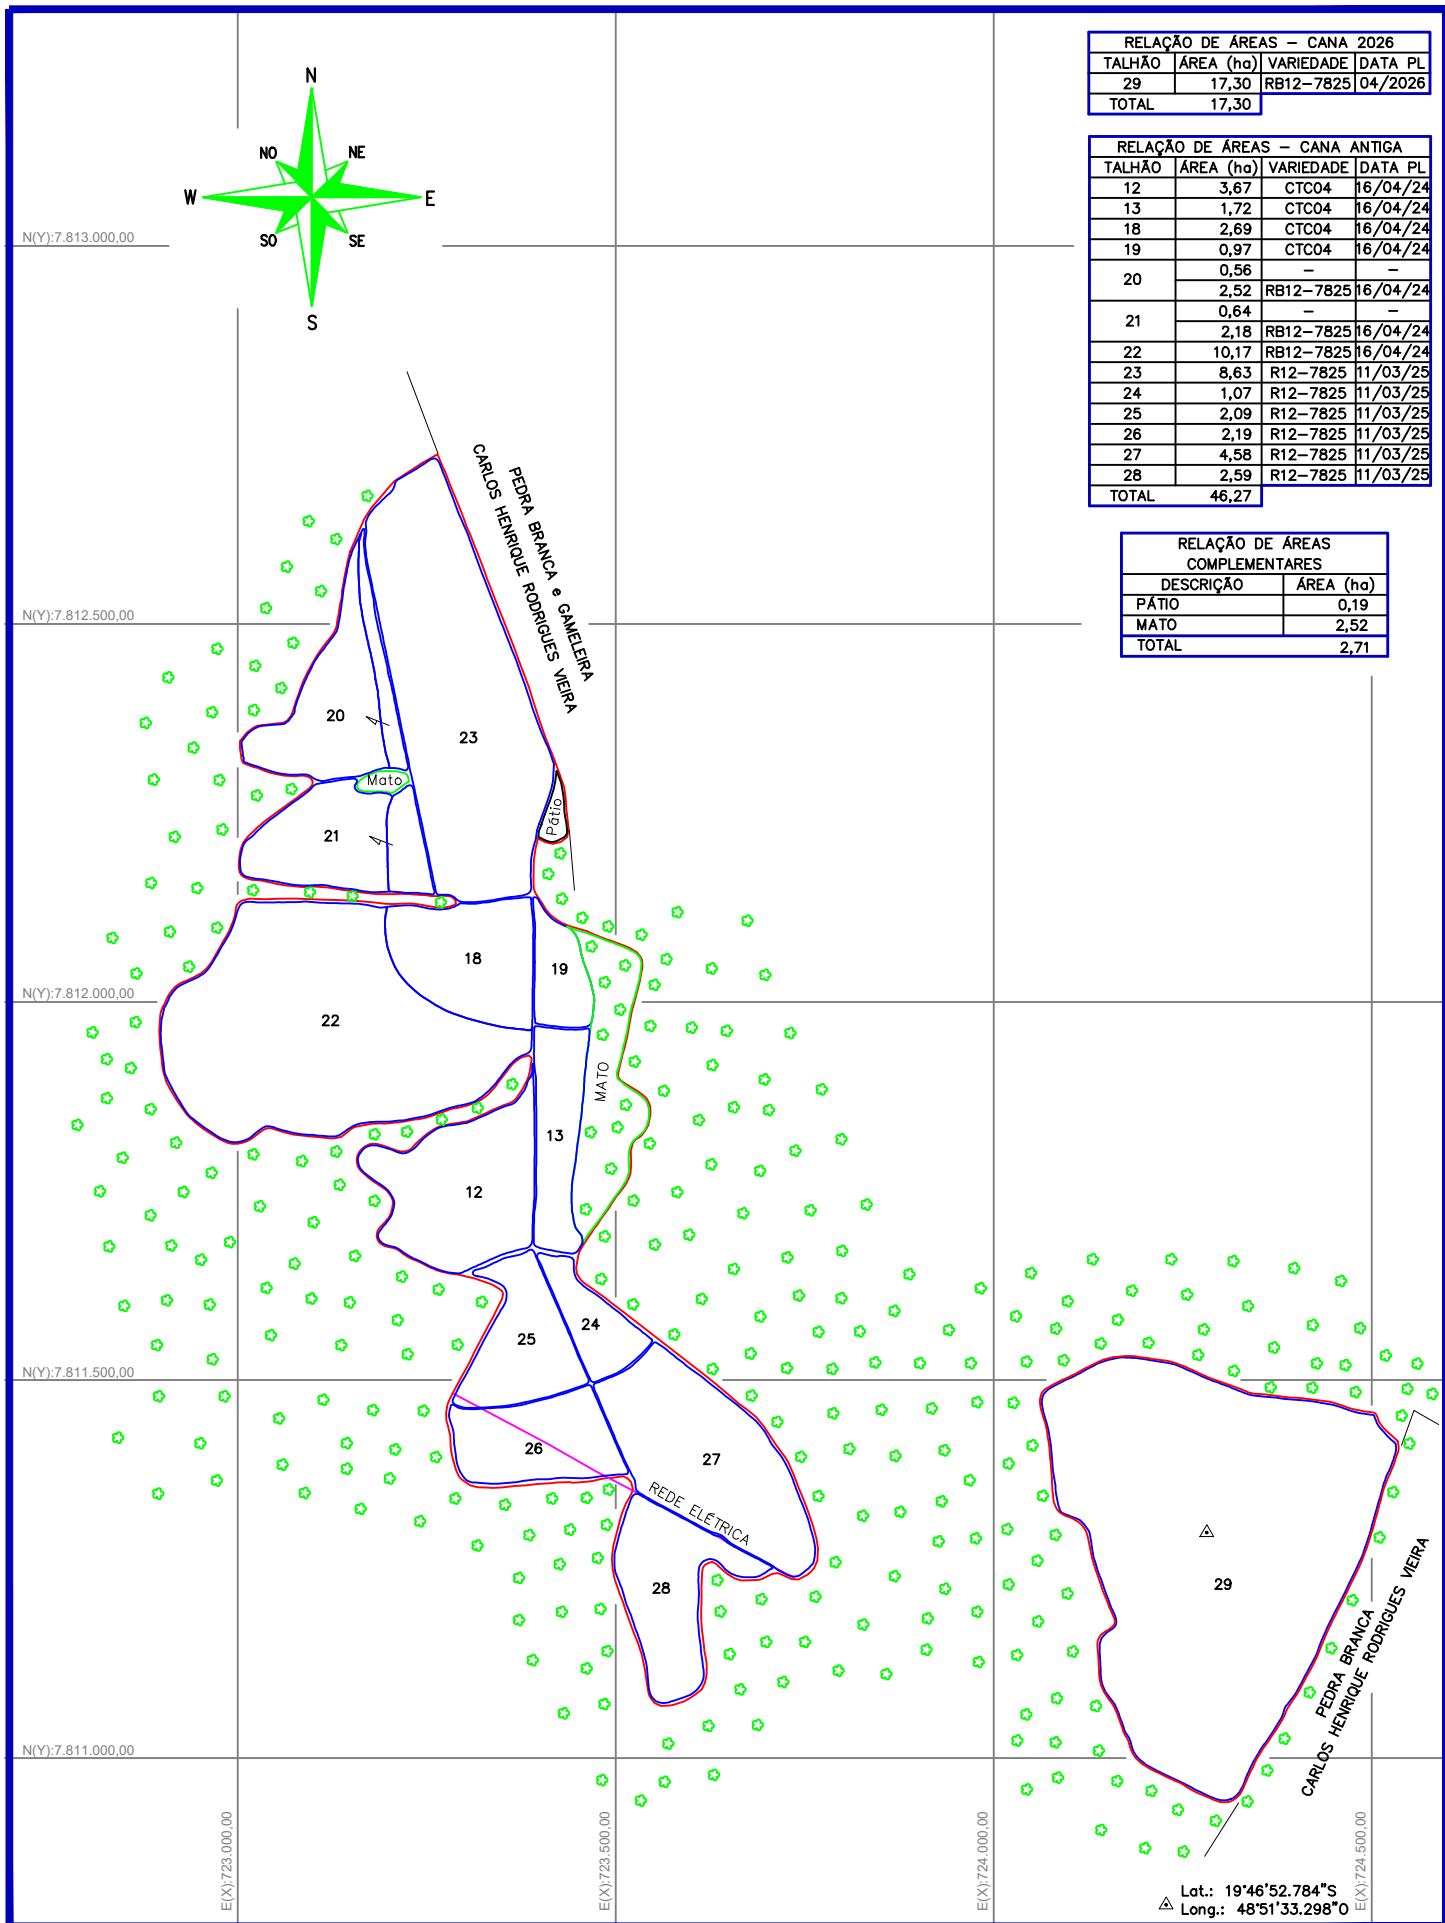

|   |                                                 |                         |                   |       |                                                 |                             |                              |
|---|-------------------------------------------------|-------------------------|-------------------|-------|-------------------------------------------------|-----------------------------|------------------------------|
| <br>LEVANTAMENTO TOPOGRÁFICO | PROPRIEDADE:<br>624 –FAZENDA PEDRA BRANCA – ENI | QUADRO DE ÁREAS<br>(ha) | CANA 2026:        | 17,30 | Desenhado por:<br>MARCIO GALASSI                | Data:<br>29/04/2026         | Núcleo:<br>3<br>PEDRA BRANCA |
|   | PROPRIETÁRIO:<br>JOSÉ BERNABE                   |                         | CARREADOR 2026:   | 0,42  | Revisado por:                                   | Data:                       |                              |
|   | FORNECEDOR:<br>CARLOS HENRIQUE RODRIGUES VIEIRA |                         | CANA ANTIGA:      | 46,27 | Engenheiro Agrimensor:<br>DANIEL CÉSAR DA SILVA |                             |                              |
|   | ÁREA TOTAL:<br>69,04 Hectares                   |                         | CARREADOR ANTIGO: | 2,34  | Município:<br>COMENDADOR GOMES – MG             | Escala:<br>1 : 10.000       |                              |
|   |                                                 |                         | COMPLEMENTARES:   | 2,71  |                                                 | Data Levant.:<br>27/04/2026 |                              |

Datum Sirgas2000 / UTM zona 22S (CM 51W)