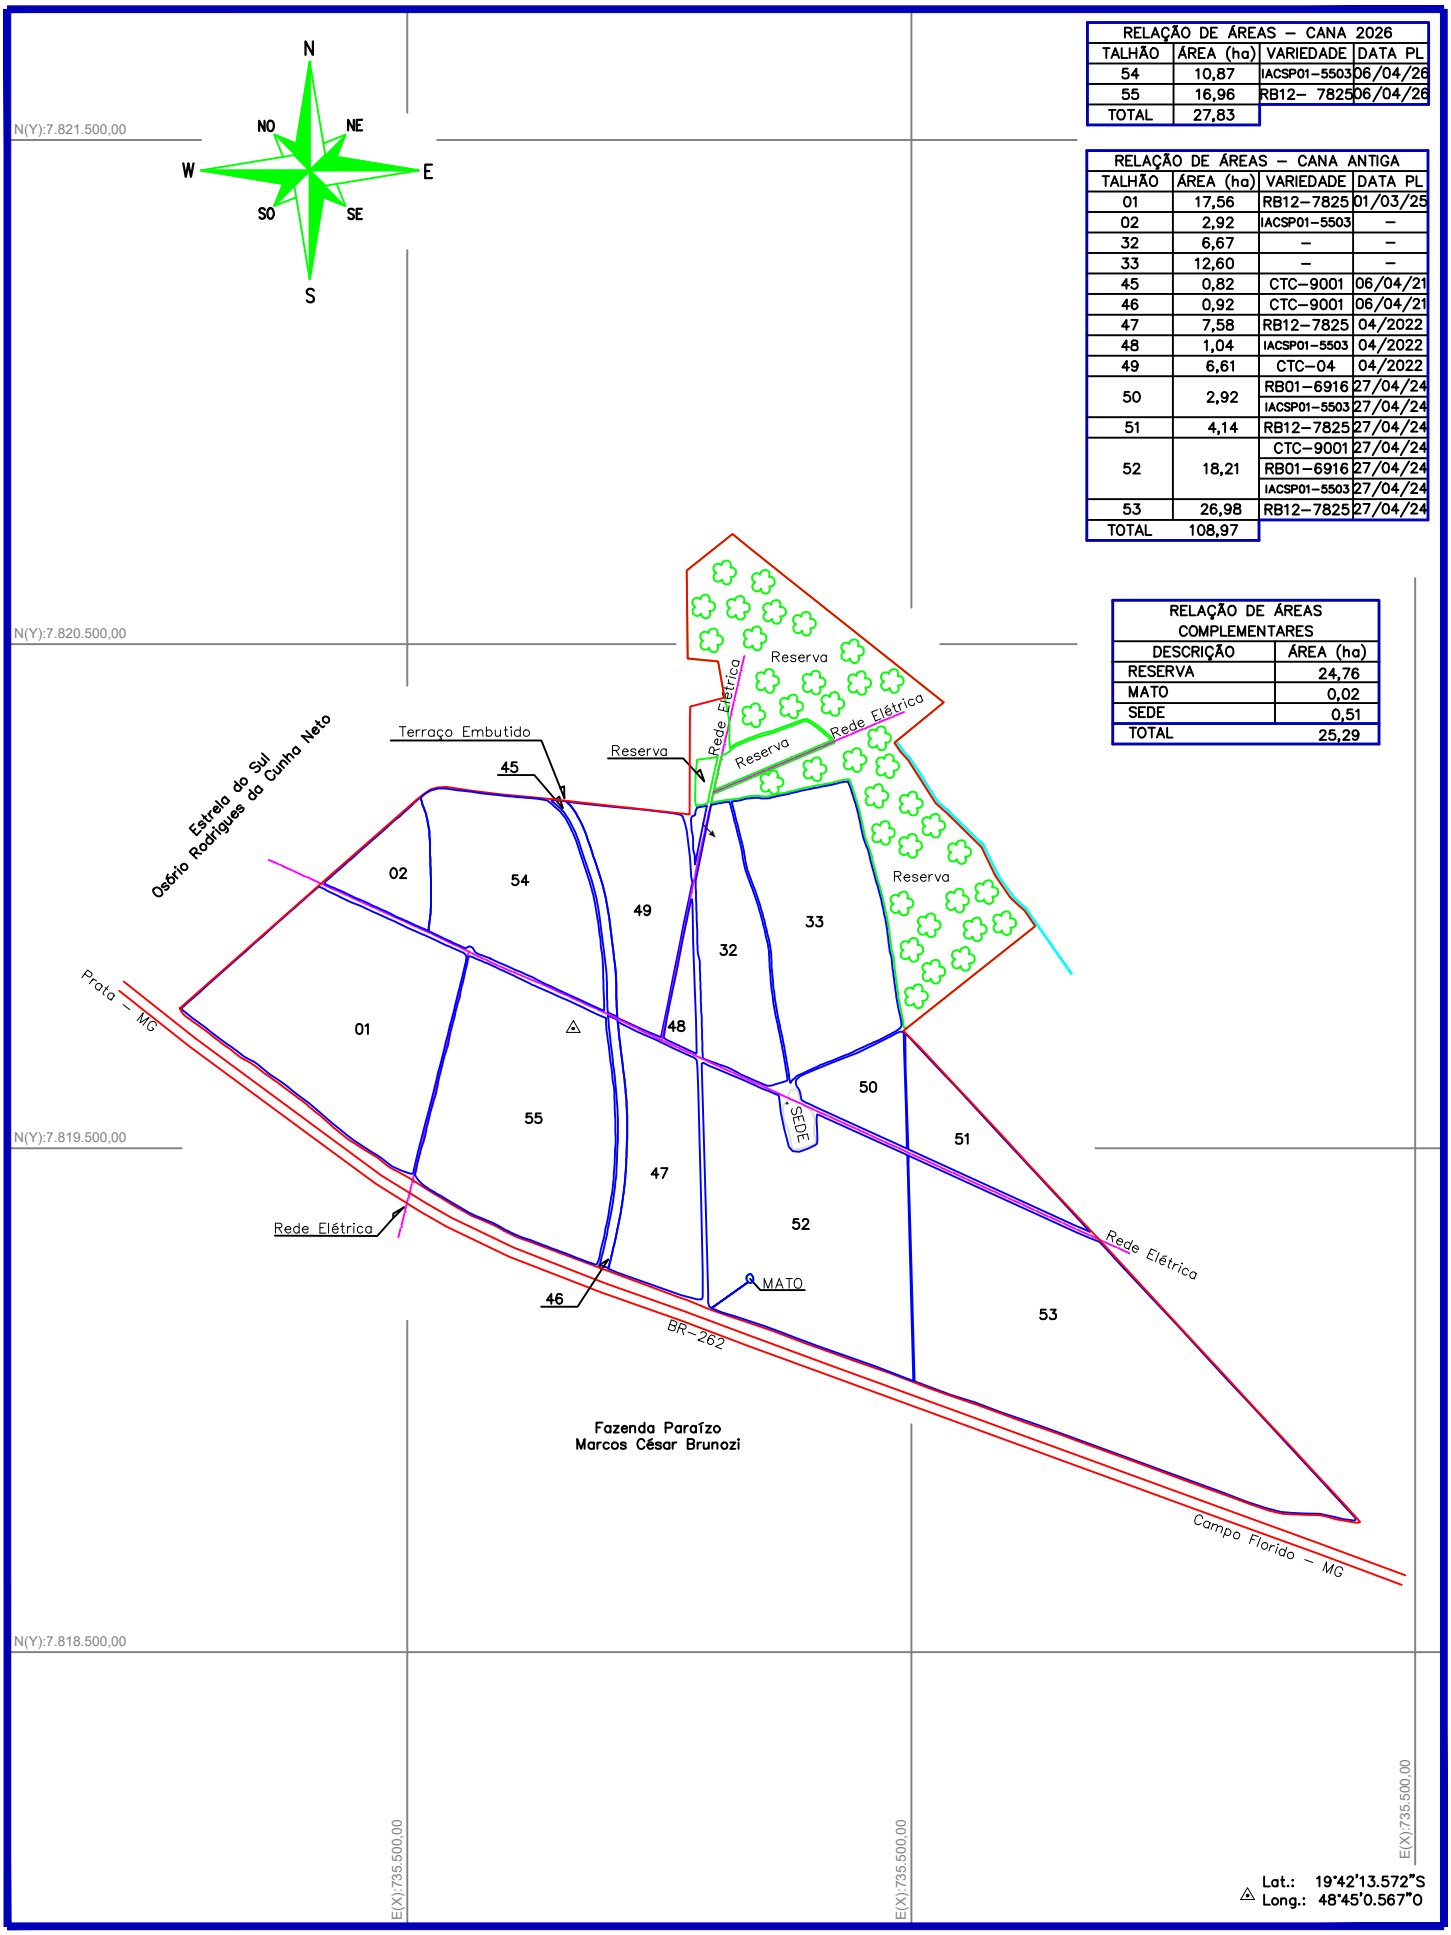


RELAÇÃO DE ÁREAS – CANA 2026			
TALHÃO	ÁREA (ha)	VARIEDADE	DATA PL
54	10,87	IACSP01-5503	06/04/26
55	16,96	RB12- 7825	06/04/26
TOTAL	27,83		

RELAÇÃO DE ÁREAS – CANA ANTIGA			
TALHÃO	ÁREA (ha)	VARIEDADE	DATA PL
01	17,56	RB12-7825	01/03/25
02	2,92	IACSP01-5503	–
32	6,67	–	–
33	12,60	–	–
45	0,82	CTC-9001	06/04/21
46	0,92	CTC-9001	06/04/21
47	7,58	RB12-7825	04/2022
48	1,04	IACSP01-5503	04/2022
49	6,61	CTC-04	04/2022
50	2,92	RB01-6916	27/04/24
		IACSP01-5503	27/04/24
51	4,14	RB12-7825	27/04/24
52	18,21	CTC-9001	27/04/24
		RB01-6916	27/04/24
		IACSP01-5503	27/04/24
53	26,98	RB12-7825	27/04/24
TOTAL	108,97		

RELAÇÃO DE ÁREAS COMPLEMENTARES	
DESCRIÇÃO	ÁREA (ha)
RESERVA	24,76
MATO	0,02
SEDE	0,51
TOTAL	25,29

USINA CORURIPE
Filial Campo Florido

LEVANTAMENTO TOPOGRÁFICO

PROPRIEDADE:
150 – FAZENDA SANTA CLARA

PROPRIETÁRIO:
CÉLIA DRUMSTA PRADO

FORNECEDOR:
CÉLIA DRUMSTA PRADO

ÁREA TOTAL:
169,48 Hectares

QUADRO DE ÁREAS (ha)

CANA 2026:	27,83
CARREADOR 2026:	0,52
CANA ANTIGA:	108,97
CARREADOR ANTIGO:	6,87
COMPLEMENTARES:	25,29

Desenhado por: MARCIO GALASSI | Data: 29/04/2026
Revisado por: – | Data: –
Responsável Técnico: DANIEL CESAR DA SILVA
Município: CAMPO FLORIDO | Escala: 1 : 15.000 | Data Levant.: 28/04/2026
Núcleo: 1 USINA

Datum Sirgas2000 / UTM zona 22S (CM 51W)