

NCY>7.845.300,00

NCY>7.844.300,00


NCY>7.843.300,00

EXX>732.300,00

EXX>733.300,00

RELAÇÃO DE ÁREAS – CANA 2024			
TALHÃO	ÁREA (ha)	VARIIDADE	DATA PL
1	6,37	RB12-7825	01/05/24
2	23,64	RB12-7825	01/05/24
3	1,50	RB12-7825	01/05/24
4	0,06	RB12-7825	01/05/24
5	1,98	RB12-7825	01/05/24
6	0,82	RB12-7825	01/05/24
7	1,20	RB12-7825	01/05/24
8	0,63	RB12-7825	01/05/24
9	3,97	RB12-7825	01/05/24
10	0,29	RB12-7825	01/05/24
11	1,61	RB12-7825	01/05/24
12	1,00	RB12-7825	01/05/24
13	3,03	RB12-7825	01/05/24
14	0,89	RB12-7825	01/05/24
15	2,23	RB12-7825	01/05/24
16	1,79	RB12-7825	01/05/24
17	2,30	RB12-7825	01/05/24
18	11,32	RB12-7825	01/05/24
19	0,31	RB12-7825	01/05/24
20	10,81	RB12-7825	01/05/24
21	4,69	RB12-7825	01/05/24
22	7,74	RB12-7825	01/05/24
23	20,01	RB12-7825	01/05/24
24	10,47	RB12-7825	01/05/24
TOTAL	118,66		

RELAÇÃO DE ÁREAS COMPLEMENTARES	
DESCRIÇÃO	ÁREA (ha)
MATO	0,28
LAGOA	0,24
ÚMIDO	1,73
ALTA TENSÃO	3,39
TOTAL	5,64

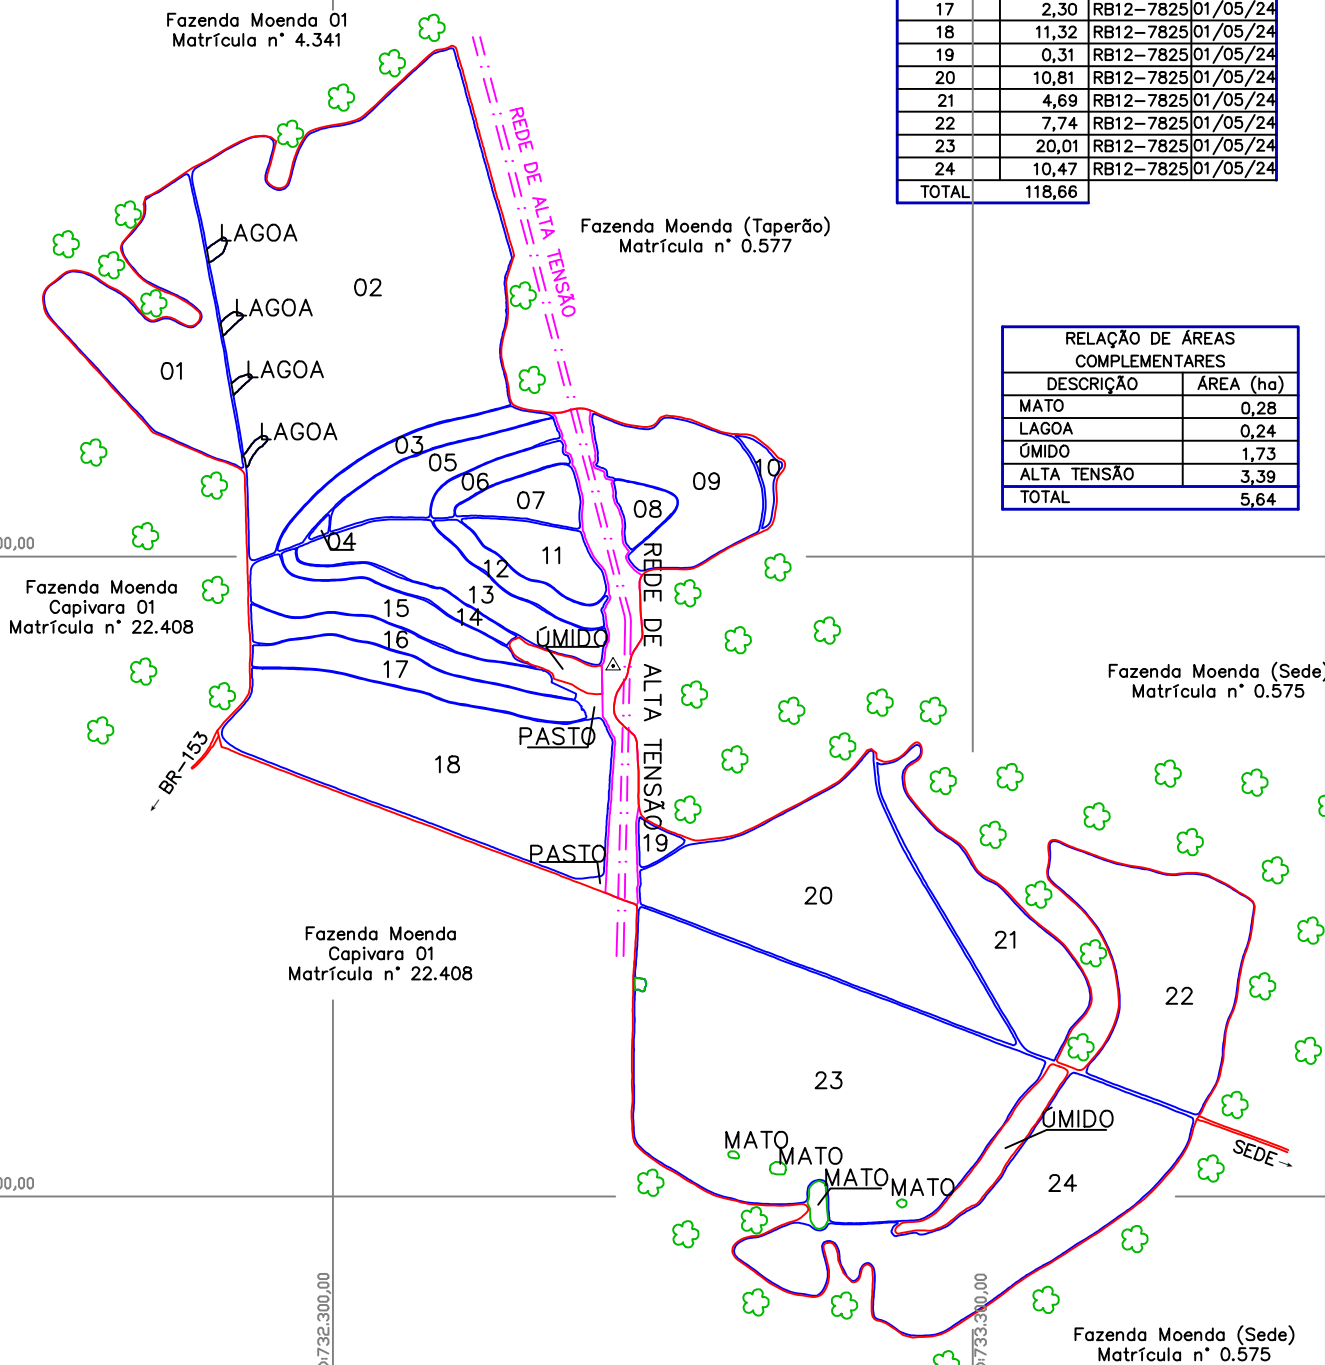

Lat.: 19°29'1.94"S
Long.: 48°46'57.59"E

 USINA CORUPIPE Filial Campo Florido	PROPRIEDADE: 53006 – FAZENDA MOENDA	QUADRO DE ÁREAS (ha)	CANA 2024:	118,66	Desenhado por: VINICIUS	Data: 30/04/2026	Núcleo: 16 PRATA
	PROPRIETÁRIO: USINA CERRADAO		CARREADOR 2024:	5,14	Revisado por:	Data:	
	FORNECEDOR: USINA CERRADAO		COMPLEMENTARES:	5,64	Engenheiro Agrimensor: DANIEL CÉSAR DA SILVA		
	LEVANTAMENTO TOPOGRAFICO		ÁREA TOTAL: 129,44 Hectares		Município: PRATA-MG	Escala: 1 : 12.500	Data Levant.: 17/05/2024