


RELAÇÃO DE ÁREAS – CANA 2026			
TALHÃO	ÁREA (ha)	VARIEDADE	DATA PL
21	25,00	RB12-7825	—
	4,72	RB10-5949	—
22	1,00	RB10-5949	—
	0,88	RB12-7825	—
TOTAL		31,60	

RELAÇÃO DE ÁREAS – CANA 2023			
TALHÃO	ÁREA (ha)	VARIEDADE	DATA PL
2	0,48	RB127825	10/04/23
3	10,67	RB127825	10/04/23
4	4,37	RB127825	10/04/23
5	4,56	RB127825	10/04/23
6	4,71	RB127825	10/04/23
7	4,30	RB127825	10/04/23
8	7,25	RB127825	10/04/23
9	10,40	RB127825	10/04/23
10	0,60	RB127825	10/04/23
11	0,59	RB127825	10/04/23
12	1,48	RB127825	10/04/23
13	2,26	RB127825	10/04/23
14	3,32	RB127825	10/04/23
15	6,46	RB127825	10/04/23
16	15,19	RB127825	10/04/23
17	0,63	RB127825	10/04/23
18	1,59	RB127825	10/04/23
19	6,07	RB127825	10/04/23
20	12,54	RB127825	10/04/23
TOTAL		97,47	

RELAÇÃO DE ÁREAS COMPLEMENTARES	
DESCRIÇÃO	ÁREA (ha)
DEPOSITO	0,02
TOTAL	0,02

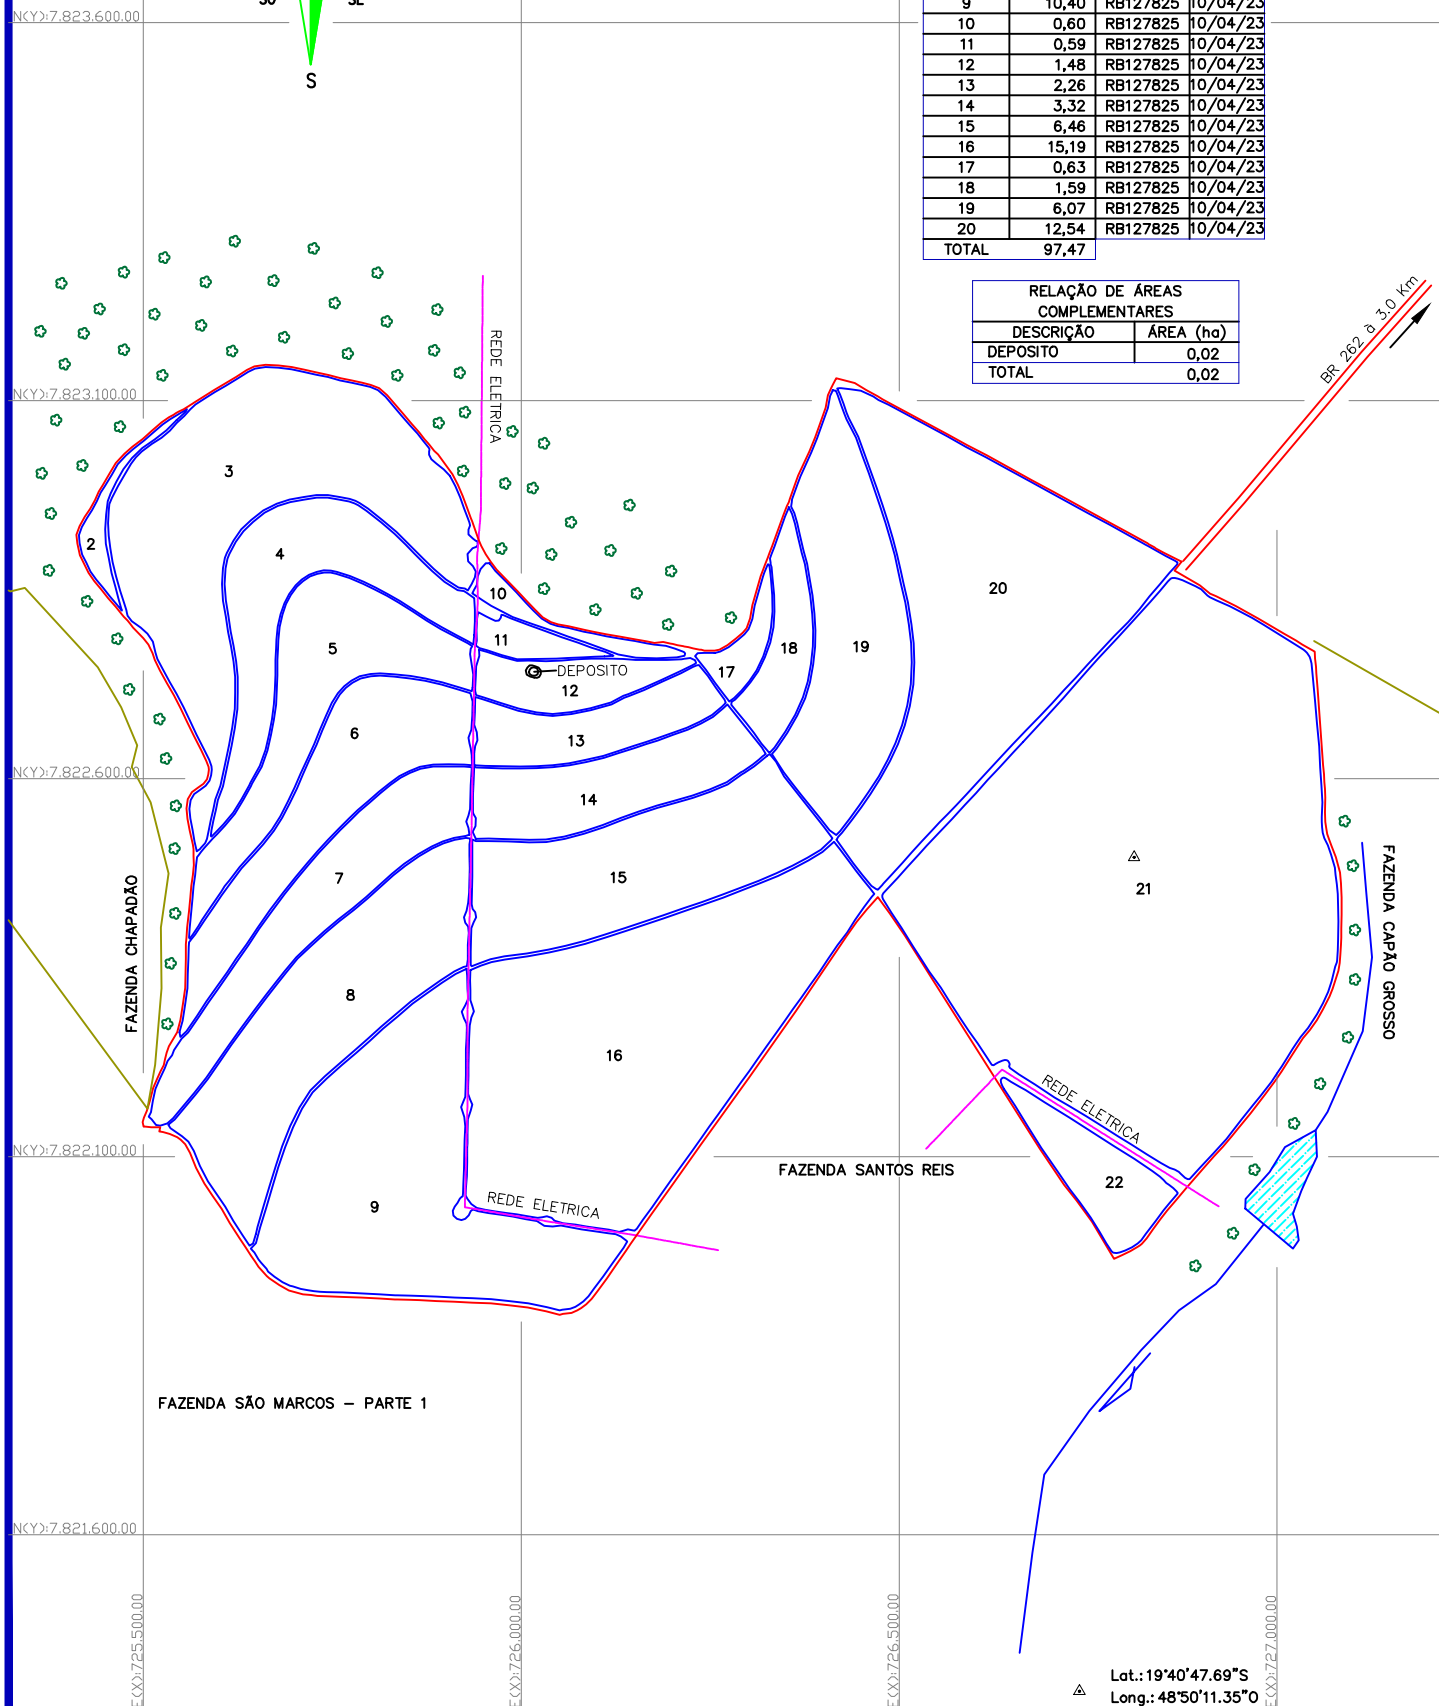

Lat.: 19°40'47.69"S
Long.: 48°50'11.35"W



LEVANTAMENTO TOPOGRAFICO

PROPRIEDADE:
1243 – FAZ NOSSA SRA AP. – PALMIERI
PROPRIETÁRIO:
FERNANDO PALMIERI
FORNECEDOR:
SILVIO DE CASTRO CUNHA JUNIOR
ÁREA TOTAL:
135,37 Hectares

QUADRO DE ÁREAS
(ha)

CANA 2026:	31,60
CARREADOR 2026:	1,06
CANA ANTIGA:	97,47
CARREADOR ANTIGO:	5,22
COMPLEMENTARES:	0,02

Desenhado por:
MÁRCIO GALASSI
Atualizado por:
—
Engº Agrimensor:
DANIEL CESAR DA SILVA
Município:
CAMPO FLORIDO
Escala:
1 : 10.000

Data:
25/05/2025

Data:
—

Núcleo:
4
SANTA CLARA

Data Levant.:
05/2026