


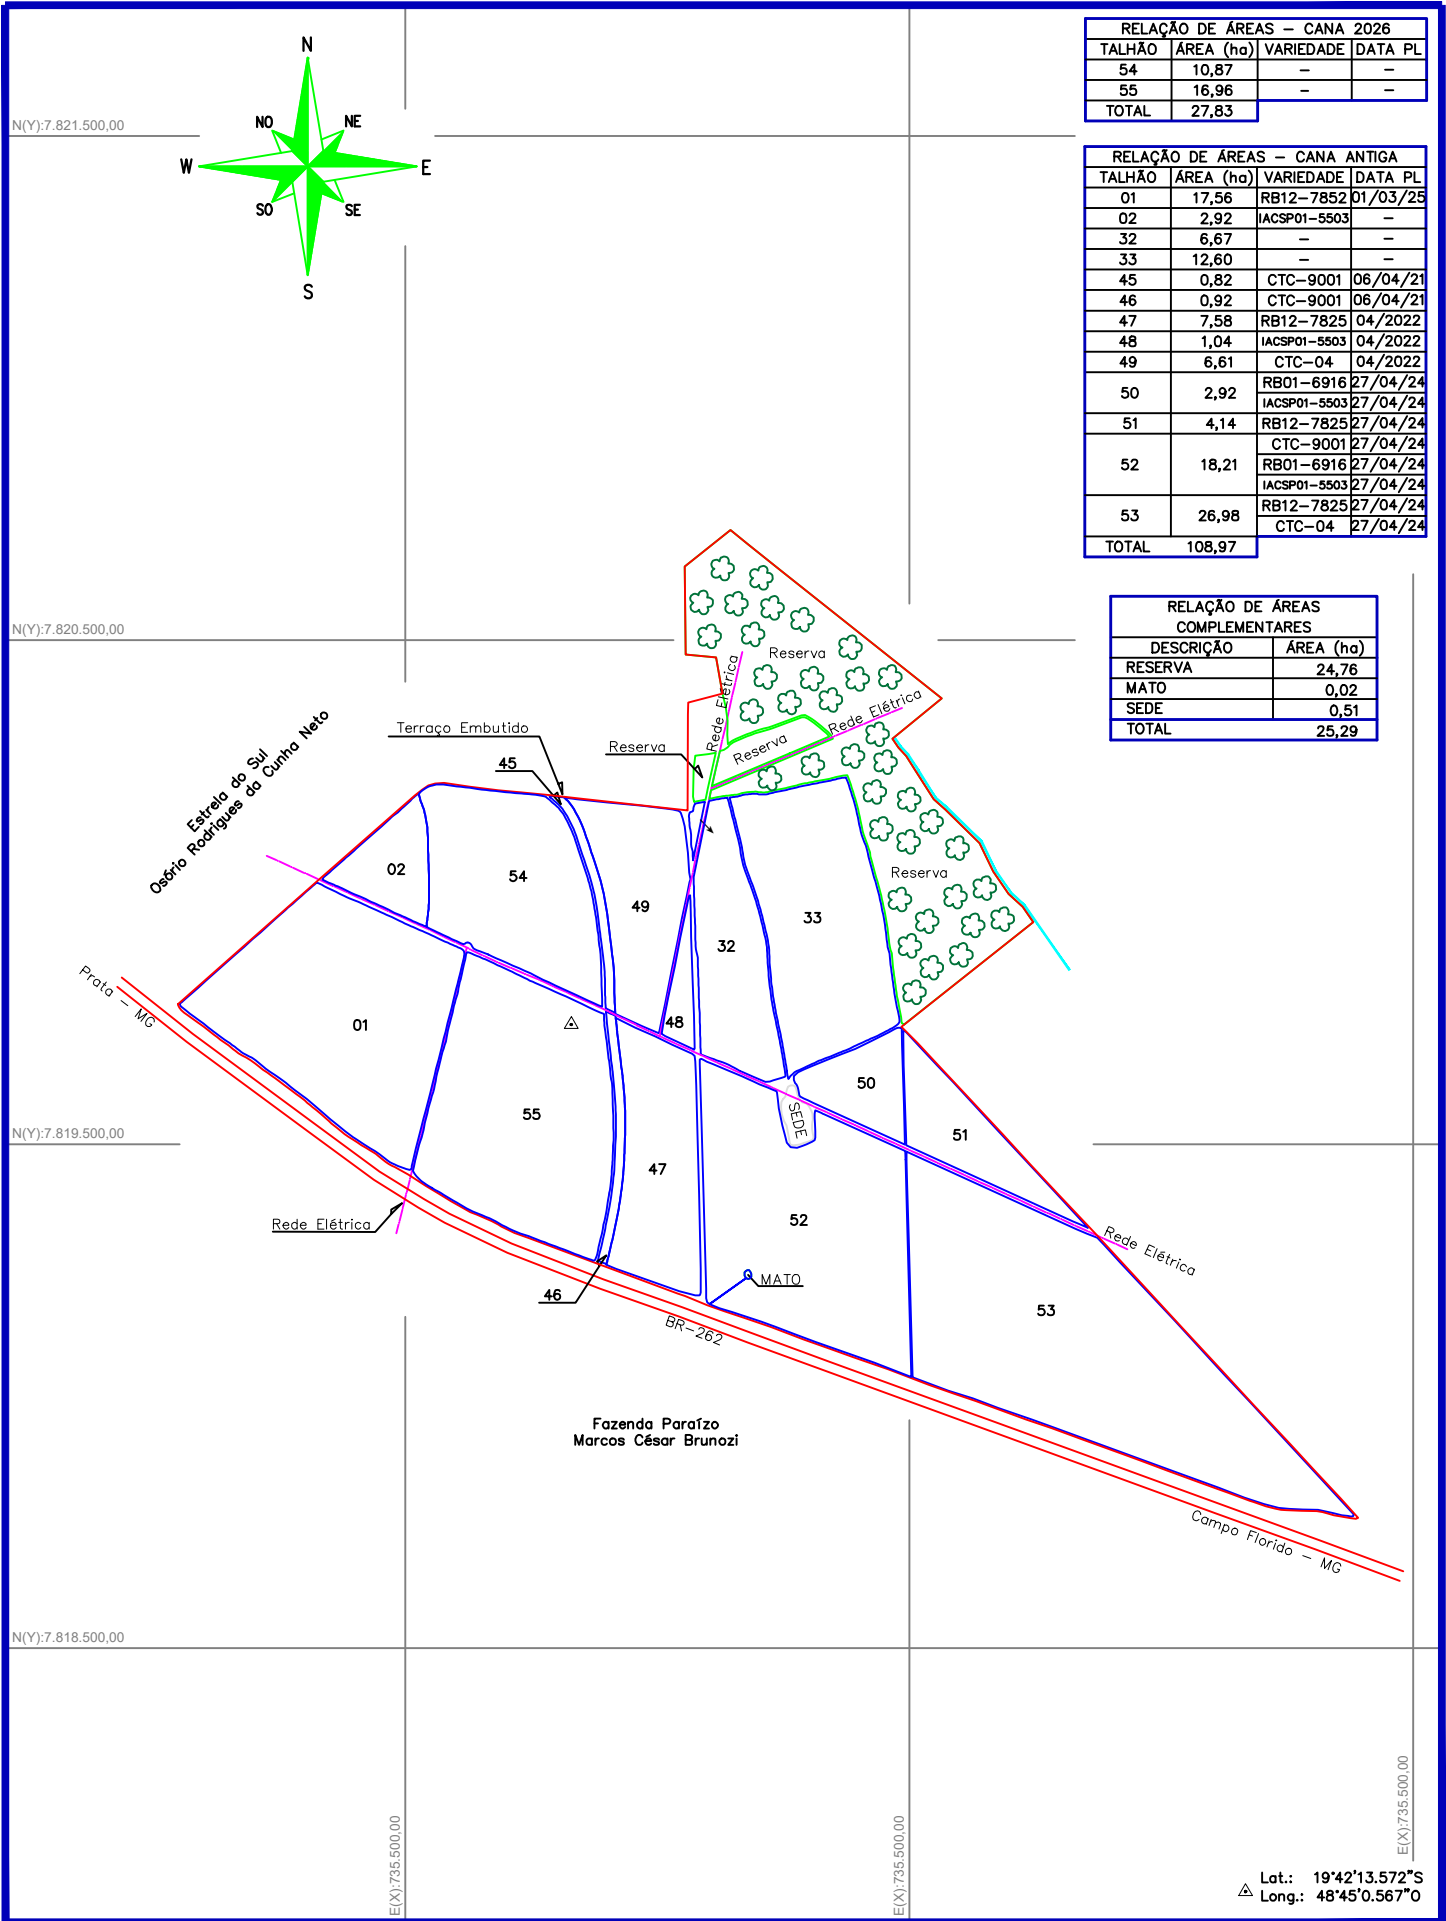

RELAÇÃO DE ÁREAS – CANA 2026			
TALHÃO	ÁREA (ha)	VARIETADE	DATA PL
54	10,87	–	–
55	16,96	–	–
TOTAL	27,83		

RELAÇÃO DE ÁREAS – CANA ANTIGA			
TALHÃO	ÁREA (ha)	VARIETADE	DATA PL
01	17,56	RB12-7852	01/03/25
02	2,92	IACSP01-5503	–
32	6,67	–	–
33	12,60	–	–
45	0,82	CTC-9001	06/04/21
46	0,92	CTC-9001	06/04/21
47	7,58	RB12-7825	04/2022
48	1,04	IACSP01-5503	04/2022
49	6,61	CTC-04	04/2022
50	2,92	RB01-6916	27/04/24
		IACSP01-5503	27/04/24
51	4,14	RB12-7825	27/04/24
		CTC-9001	27/04/24
52	18,21	RB01-6916	27/04/24
		IACSP01-5503	27/04/24
53	26,98	RB12-7825	27/04/24
		CTC-04	27/04/24
TOTAL	108,97		

RELAÇÃO DE ÁREAS COMPLEMENTARES	
DESCRIÇÃO	ÁREA (ha)
RESERVA	24,76
MATO	0,02
SEDE	0,51
TOTAL	25,29

 USINA CORUMPE Filial Campo Florido	PROPRIEDADE: 150 – FAZENDA SANTA CLARA	QUADRO DE ÁREAS (ha)	CANA 2026:	27,83	Desenhado por: MARCIO GALASSI	Data: 29/04/2026	Núcleo: 1 USINA	
	PROPRIETÁRIO: CÉLIA DRUMSTA PRADO		CARREADOR 2026:	0,52	Revisado por: —	Data: —		
	FORNECEDOR: CÉLIA DRUMSTA PRADO		CANA ANTIGA:	108,97	Responsável Técnico: DANIEL CESAR DA SILVA			
	LEVANTAMENTO TOPOGRÁFICO		ÁREA TOTAL: 169,48 Hectares	CARREADOR ANTIGO:	6,87	Município: CAMPO FLORIDO	Escala: 1 : 15.000	Data Levant.: 28/04/2026
				COMPLEMENTARES:	25,29			

Datum Sirgas2000 / UTM zona 22S (CM 51W)