

N(Y): 7.831.800,00

N(Y): 7.830.800,00


N(Y): 7.829.800,00

025 - FAZENDA SANTO ANTÔNIO
IVONE DE FÁTIMA DOS SANTOS BERNÃO RIVEIRA

468 - FAZENDA SANTANA
SILVIO DE CASTRO CUNHA JÚNIOR

387 - FAZENDA PIRACANJUBA/IRARAS
SILVIO DE CASTRO CUNHA JÚNIOR

387 - FAZENDA PIRACANJUBA/IRARAS
SILVIO DE CASTRO CUNHA JÚNIOR

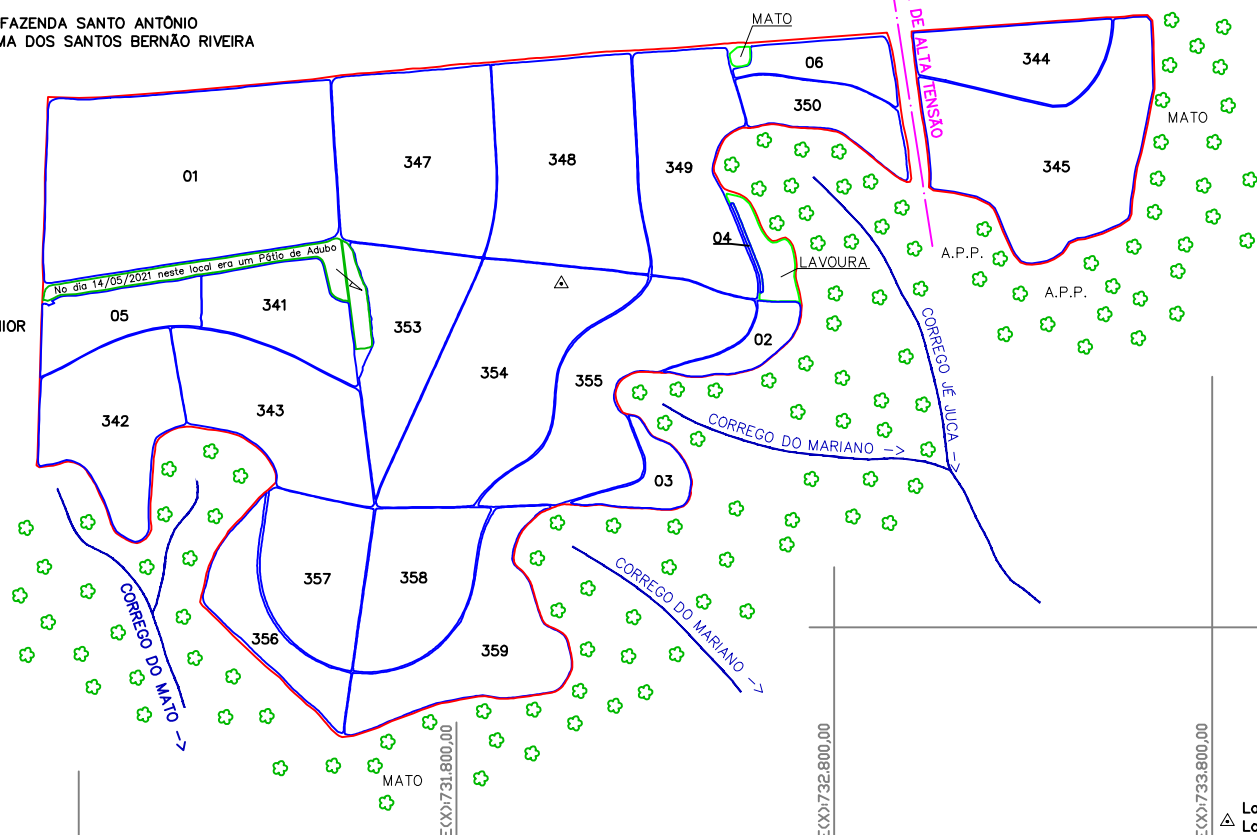

RELAÇÃO DE ÁREAS COMPLEMENTARES	
DESCRIÇÃO	ÁREA (ha)
LAVOURA	2,09
PÁTIO DE ADUBO	4,35
MATO	0,24
TOTAL	6,68

RELAÇÃO DE ÁREAS - CANA 2021			
TALHÃO	ÁREA (ha)	VARIEDADE	DATA PL
341	8,49	RB86-7515	04/2021
342	13,16	RB86-7515	04/2021
343	14,89	RB86-7515	04/2021
TOTAL	36,54		

RELAÇÃO DE ÁREAS - CANA 2022			
TALHÃO	ÁREA (ha)	VARIEDADE	DATA PL
344	8,68	CTC-04	03/2022
345	22,23	CTC-04	03/2022
TOTAL	30,91		

RELAÇÃO DE ÁREAS - CANA 2024			
TALHÃO	ÁREA (ha)	VARIEDADE	DATA PL
347	10,05	CTC-3445	29/02/24
	1,90	CTC 14294	29/02/24
	1,90	CTC 153902	29/02/24
	1,90	CTC 143522	29/02/24
	1,90	RB04-1443	29/02/24
348	1,90	RB06-5173	29/02/24
	9,00	CTC 3445	29/02/24
	9,99	RB01-6916	29/02/24
	1,00	CTC 1886	29/02/24
	1,00	CTC 2519	29/02/24
349	13,00	RB12-7825	29/02/24
	2,51	CTC 1886	29/02/24
350	6,01	RB12-7825	29/02/24
353	11,21	CTC 3445	29/02/24
		RB04-1443	29/02/24
		RB06-5173	29/02/24
		CTC 3445	29/02/24
354	11,00	CTC 3445	29/02/24
		RB01-6916	29/02/24
		CTC 1886	29/02/24
		CTC 2519	29/02/24
		RB12-7825	29/02/24
		RB01-6916	29/02/24
		RB04-6299	29/02/24
		RB15-7400	29/02/24
		SYN146	29/02/24
		IAC 2361	29/02/24
		CTC 1886	29/02/24
		IAC 021064	29/02/24
355	5,00	IAC 5503	29/02/24
		RB12-7825	29/02/24
		IAC-5503	29/02/24
		RB12-7825	29/02/24
		RB12-7825	29/02/24
356	5,90	RB12-7825	29/02/24
357	10,75	RB12-7825	29/02/24
358	11,25	RB12-7825	29/02/24
359	12,78	RB12-7825	29/02/24
TOTAL	155,72		

RELAÇÃO DE ÁREAS - CANA 2025			
TALHÃO	ÁREA (ha)	VARIEDADE	DATA PL
01	34,48	CTC-3445	30/03/25
		IAC-5503	30/03/25
02	2,72	SC07-1717	30/03/25
		CTC 11	30/03/25
		RB06-6351	30/03/25
		RB10-6893	30/03/25
		RB10-5949	30/03/25
		BR07-6553	30/03/25
		B12-7546	30/03/25
03	2,93	CTC 11	30/03/25
04	0,18	CTC 11	30/03/25
TOTAL	40,31		

RELAÇÃO DE ÁREAS - CANA 2026			
TALHÃO	ÁREA (ha)	VARIEDADE	DATA PL
05	6,06	RB10-6893	-
		S.N 01	-
06	4,33	NA 03559	-
TOTAL	10,39		



LEVANTAMENTO TOPOGRÁFICO

PROPRIEDADE:
611 - FAZENDA SÃO SEBASTIÃO II
PROPRIETÁRIO:
SILVIO DE CASTRO CUNHA JÚNIOR
FORNECEDOR:
SILVIO DE CASTRO CUNHA JÚNIOR
ÁREA TOTAL:
290,13 Hectares

QUADRO DE ÁREAS (ha)
CANA 2026: 10,39
CARREADOR 2026: 1,44
CANA ANTIGA: 263,48
CARREADOR ANTIGO: 8,14
COMPLEMENTARES: 6,68

Desenhado por: DOUGLAS WISTERSON
Data: 22/05/2026
Atualizado por: -
Data: -
Engenheiro Agrimensor: DANIEL CESAR DA SILVA
Município: CAMPO FLORIDO-MG
Escala: 1 : 20.000
Data Levant.: 05/2026
Núcleo: 4
SANTA CLARA