


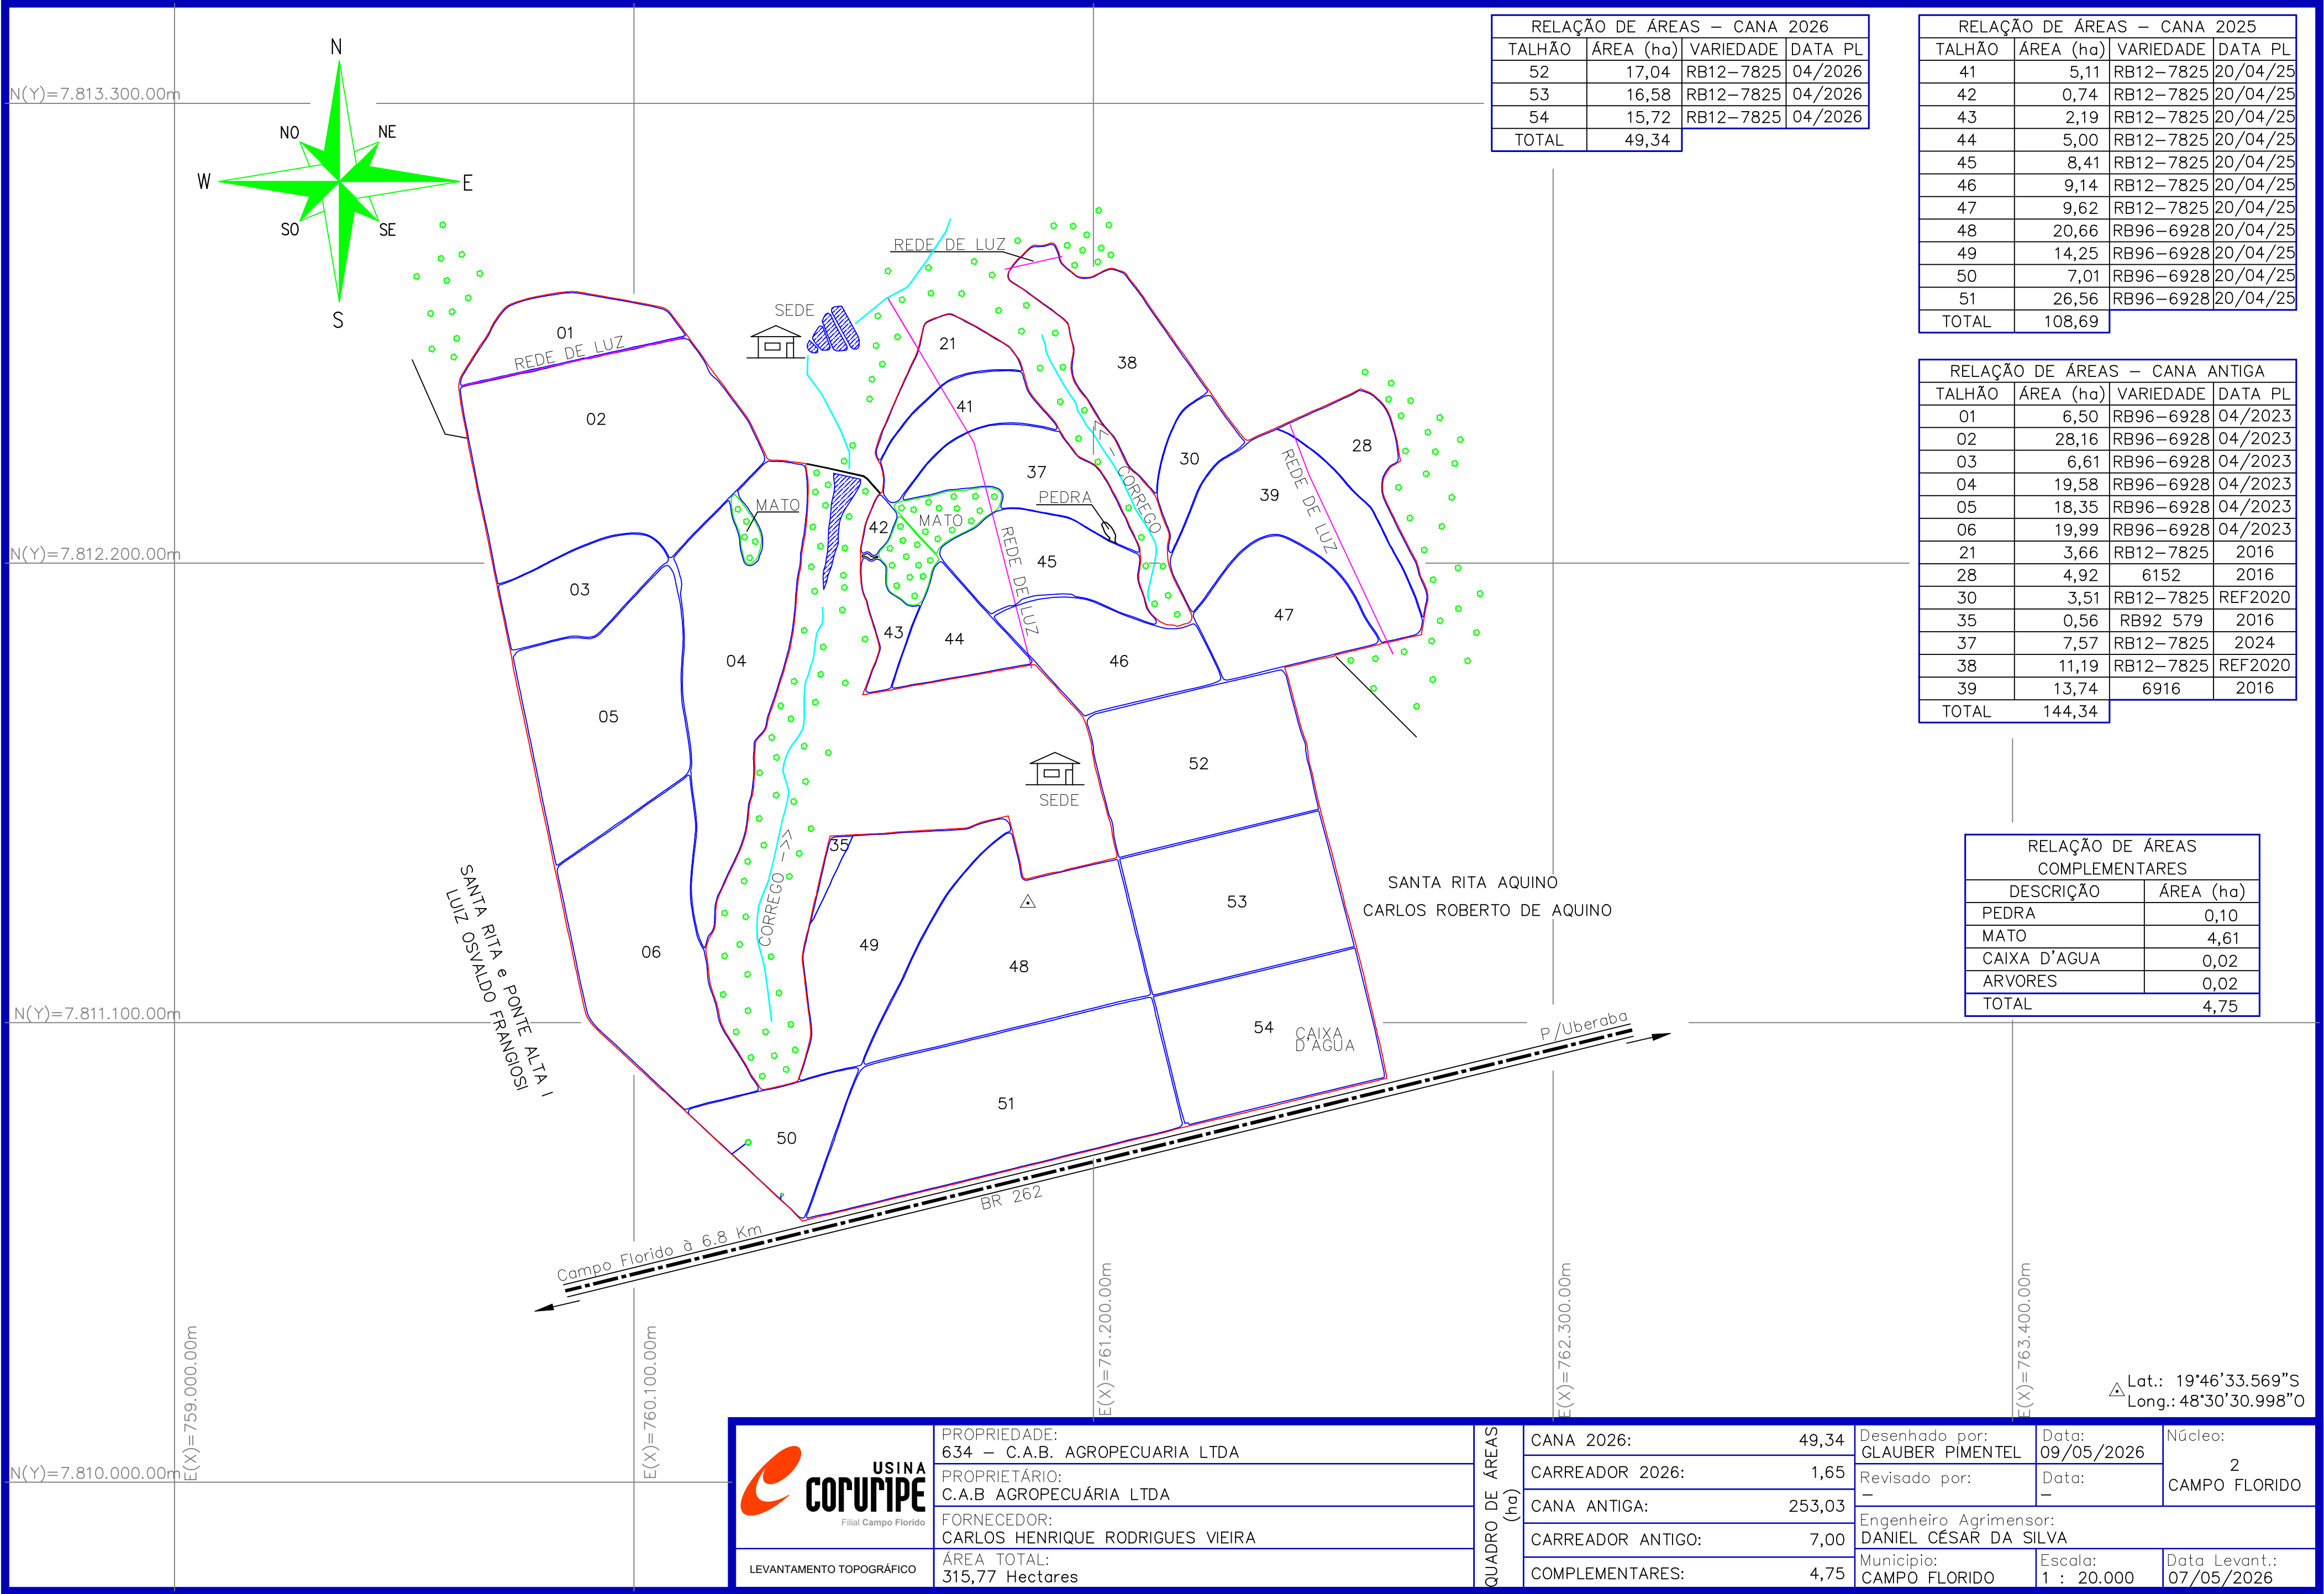

RELAÇÃO DE ÁREAS – CANA 2026			
TALHÃO	ÁREA (ha)	VARIEDADE	DATA PL
52	17,04	RB12–7825	04/2026
53	16,58	RB12–7825	04/2026
54	15,72	RB12–7825	04/2026
TOTAL	49,34		

RELAÇÃO DE ÁREAS – CANA 2025			
TALHÃO	ÁREA (ha)	VARIEDADE	DATA PL
41	5,11	RB12–7825	20/04/25
42	0,74	RB12–7825	20/04/25
43	2,19	RB12–7825	20/04/25
44	5,00	RB12–7825	20/04/25
45	8,41	RB12–7825	20/04/25
46	9,14	RB12–7825	20/04/25
47	9,62	RB12–7825	20/04/25
48	20,66	RB96–6928	20/04/25
49	14,25	RB96–6928	20/04/25
50	7,01	RB96–6928	20/04/25
51	26,56	RB96–6928	20/04/25
TOTAL	108,69		

RELAÇÃO DE ÁREAS – CANA ANTIGA			
TALHÃO	ÁREA (ha)	VARIEDADE	DATA PL
01	6,50	RB96–6928	04/2023
02	28,16	RB96–6928	04/2023
03	6,61	RB96–6928	04/2023
04	19,58	RB96–6928	04/2023
05	18,35	RB96–6928	04/2023
06	19,99	RB96–6928	04/2023
21	3,66	RB12–7825	2016
28	4,92	6152	2016
30	3,51	RB12–7825	REF2020
35	0,56	RB92 579	2016
37	7,57	RB12–7825	2024
38	11,19	RB12–7825	REF2020
39	13,74	6916	2016
TOTAL	144,34		

RELAÇÃO DE ÁREAS COMPLEMENTARES	
DESCRIÇÃO	ÁREA (ha)
PEDRA	0,10
MATO	4,61
CAIXA D'ÁGUA	0,02
ARVORES	0,02
TOTAL	4,75

 USINA CORUPIPE Filial Campo Florido	PROPRIEDADE: 634 – C.A.B. AGROPECUARIA LTDA	QUADRO DE ÁREAS (ha)	CANA 2026:	49,34	Desenhado por: GLAUBER PIMENTEL	Data: 09/05/2026	Núcleo: 2 CAMPO FLORIDO
	PROPRIETÁRIO: C.A.B AGROPECUÁRIA LTDA		CARREADOR 2026:	1,65	Revisado por: –	Data: –	
	FORNECEDOR: CARLOS HENRIQUE RODRIGUES VIEIRA		CANA ANTIGA:	253,03	Engenheiro Agrimensor: DANIEL CÉSAR DA SILVA		
	ÁREA TOTAL: 315,77 Hectares		CARREADOR ANTIGO:	7,00	Município: CAMPO FLORIDO	Escala: 1 : 20.000	Data Levant.: 07/05/2026
LEVANTAMENTO TOPOGRÁFICO	COMPLEMENTARES:		4,75				