

RELAÇÃO DE ÁREAS – CANA 2021			
TALHÃO	ÁREA (ha)	VARIEDADE	DATA PL
81	14,21	RB92-579	10/04/21
82	14,04	RB92-579	10/04/21
83	9,46	RB92-579	10/04/21
84	2,30	RB92-579	10/04/21
85	8,94	RB92-579	10/04/21
86	1,93	RB92-579	10/04/21
87	10,57	RB92-579	10/04/21
88	3,68	RB92-579	10/04/21
89	11,49	RB92-579	10/04/21
90	6,44	RB92-579	10/04/21
TOTAL		83,06	

RELAÇÃO DE ÁREAS – CANA 2022			
TALHÃO	ÁREA (ha)	VARIEDADE	DATA PL
92	17,81	RB12-7825	04/22
93	20,76	RB12-7825	04/22
94	32,71	RB12-7825	04/22
95	6,60	RB12-7825	04/22
96	20,44	RB12-7825	04/22
97	10,38	RB12-7825	04/22
98	18,29	RB12-7825	04/22
99	9,43	CV-6654	04/22
TOTAL		136,42	

RELAÇÃO DE ÁREAS – CANA 2023			
TALHÃO	ÁREA (ha)	VARIEDADE	DATA PL
01	31,25	RB12-7825	27/03/23
02	17,32	RB12-7825	27/03/23
03	2,17	RB12-7825	27/03/23
04	14,57	RB12-7825	27/03/23
05	9,62	RB12-7825	27/03/23
06	25,65	RB12-7825	27/03/23
07	38,00	RB12-7825	27/03/23
08	1,26	RB12-7825	27/03/23
09	9,42	RB12-7825	27/03/23
10	6,72	RB12-7825	27/03/23
11	5,88	107602	27/03/23
TOTAL		161,86	

RELAÇÃO DE ÁREAS – CANA 2024			
TALHÃO	ÁREA (ha)	VARIEDADE	DATA PL
100	0,60	RB12-7825	03/2024
101	0,58	RB12-7825	03/2024
102	1,54	RB12-7825	03/2024
103	1,66	RB12-7825	03/2024
104	7,52	RB12-7825	03/2024
105	2,14	RB12-7825	03/2024
106	5,03	RB12-7825	03/2024
TOTAL		19,07	

RELAÇÃO DE ÁREAS – CANA 2026			
TALHÃO	ÁREA (ha)	VARIEDADE	DATA PL
91	10,00	RB12-7825	05/2026
	4,99	RB10-5949	05/2026
TOTAL		14,99	


N(y):7.826.100,00

N(y):7.824.800,00

N(y):7.823.500,00

N(y):7.822.200,00

FAZENDA DO PINTO
MATR: 39.709; 21.598 (2º ORI – UBERABA)
D.C.C. AGROPECUÁRIA ESPERANÇA LTDA

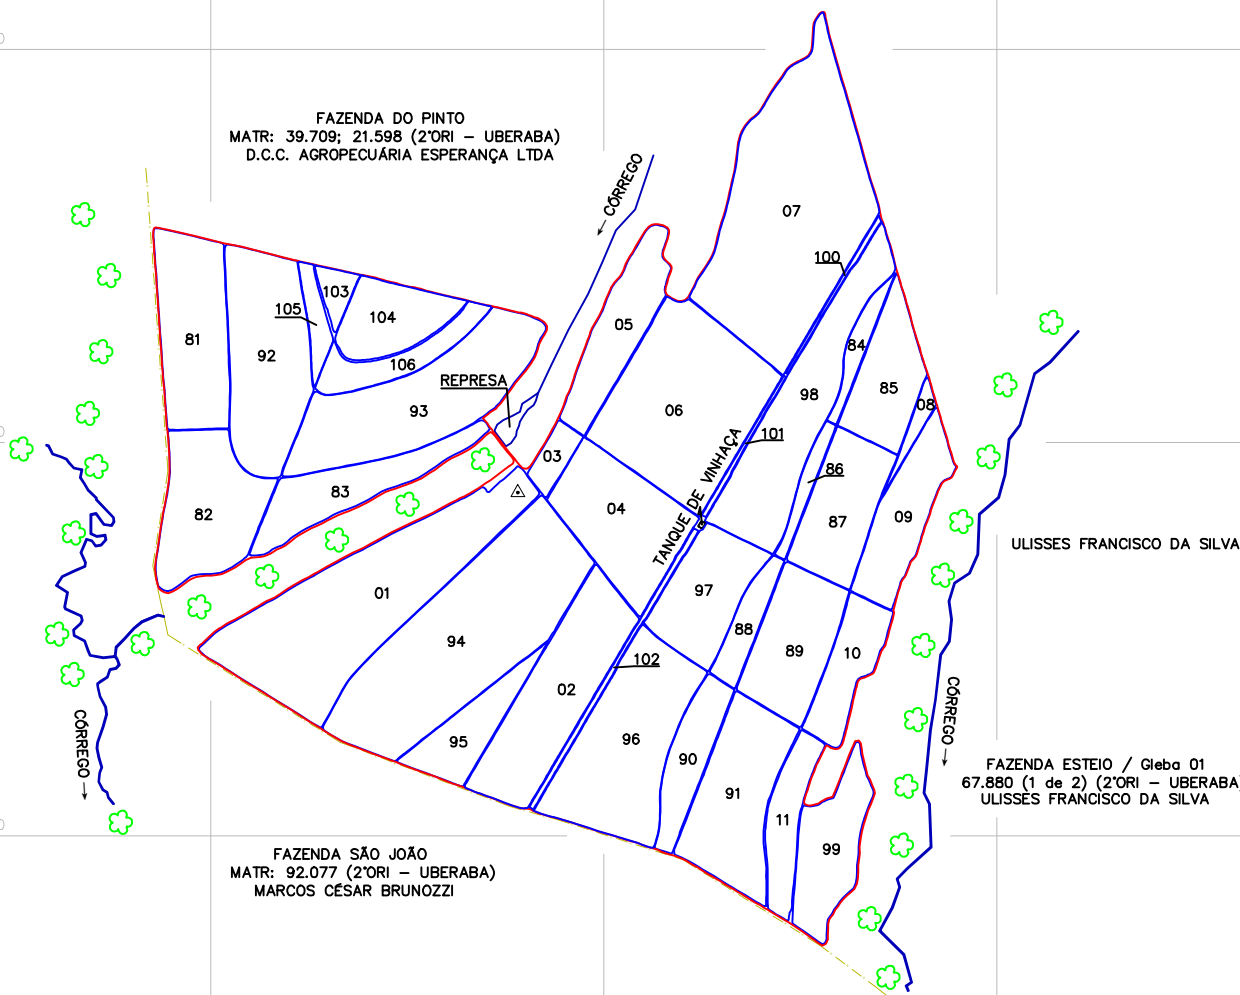

ULISSES FRANCISCO DA SILVA

FAZENDA ESTEIO / Gleba 01
67.880 (1 de 2) (2º ORI – UBERABA)
ULISSES FRANCISCO DA SILVA

Lat.: 19°40'15.329"S
Long.: 48°43'19.800"O

 LEVANTAMENTO TOPOGRÁFICO	PROPRIEDADE: 935 – SANTA MARTA	QUADRO DE ÁREAS (ha)	CANA 2026:	14,99	Desenhado por: YGOR DOS SANTOS	Data: 23/05/2026	Núcleo: 1 USINA
	PROPRIETÁRIO: MARIA INEZ BORGES DE CASTRO CUNHA		CARREADOR 2026:	0,75	Atualizado por:	Data:	
	FORNECEDOR: SILVIO DE CASTRO CUNHA JUNIOR		CANA ANTIGA:	400,41	Engº Agrimensor: DANIEL CESAR DA SILVA		
	ÁREA TOTAL: 426,86 ha		CARREADOR ANTIGO:	10,68	Município: CAMPO FLORIDO		
			TANQUE DE VINHAÇA:	0,03	Escala: 1 : 25.000		
			Data Levant.: 05/2026				