


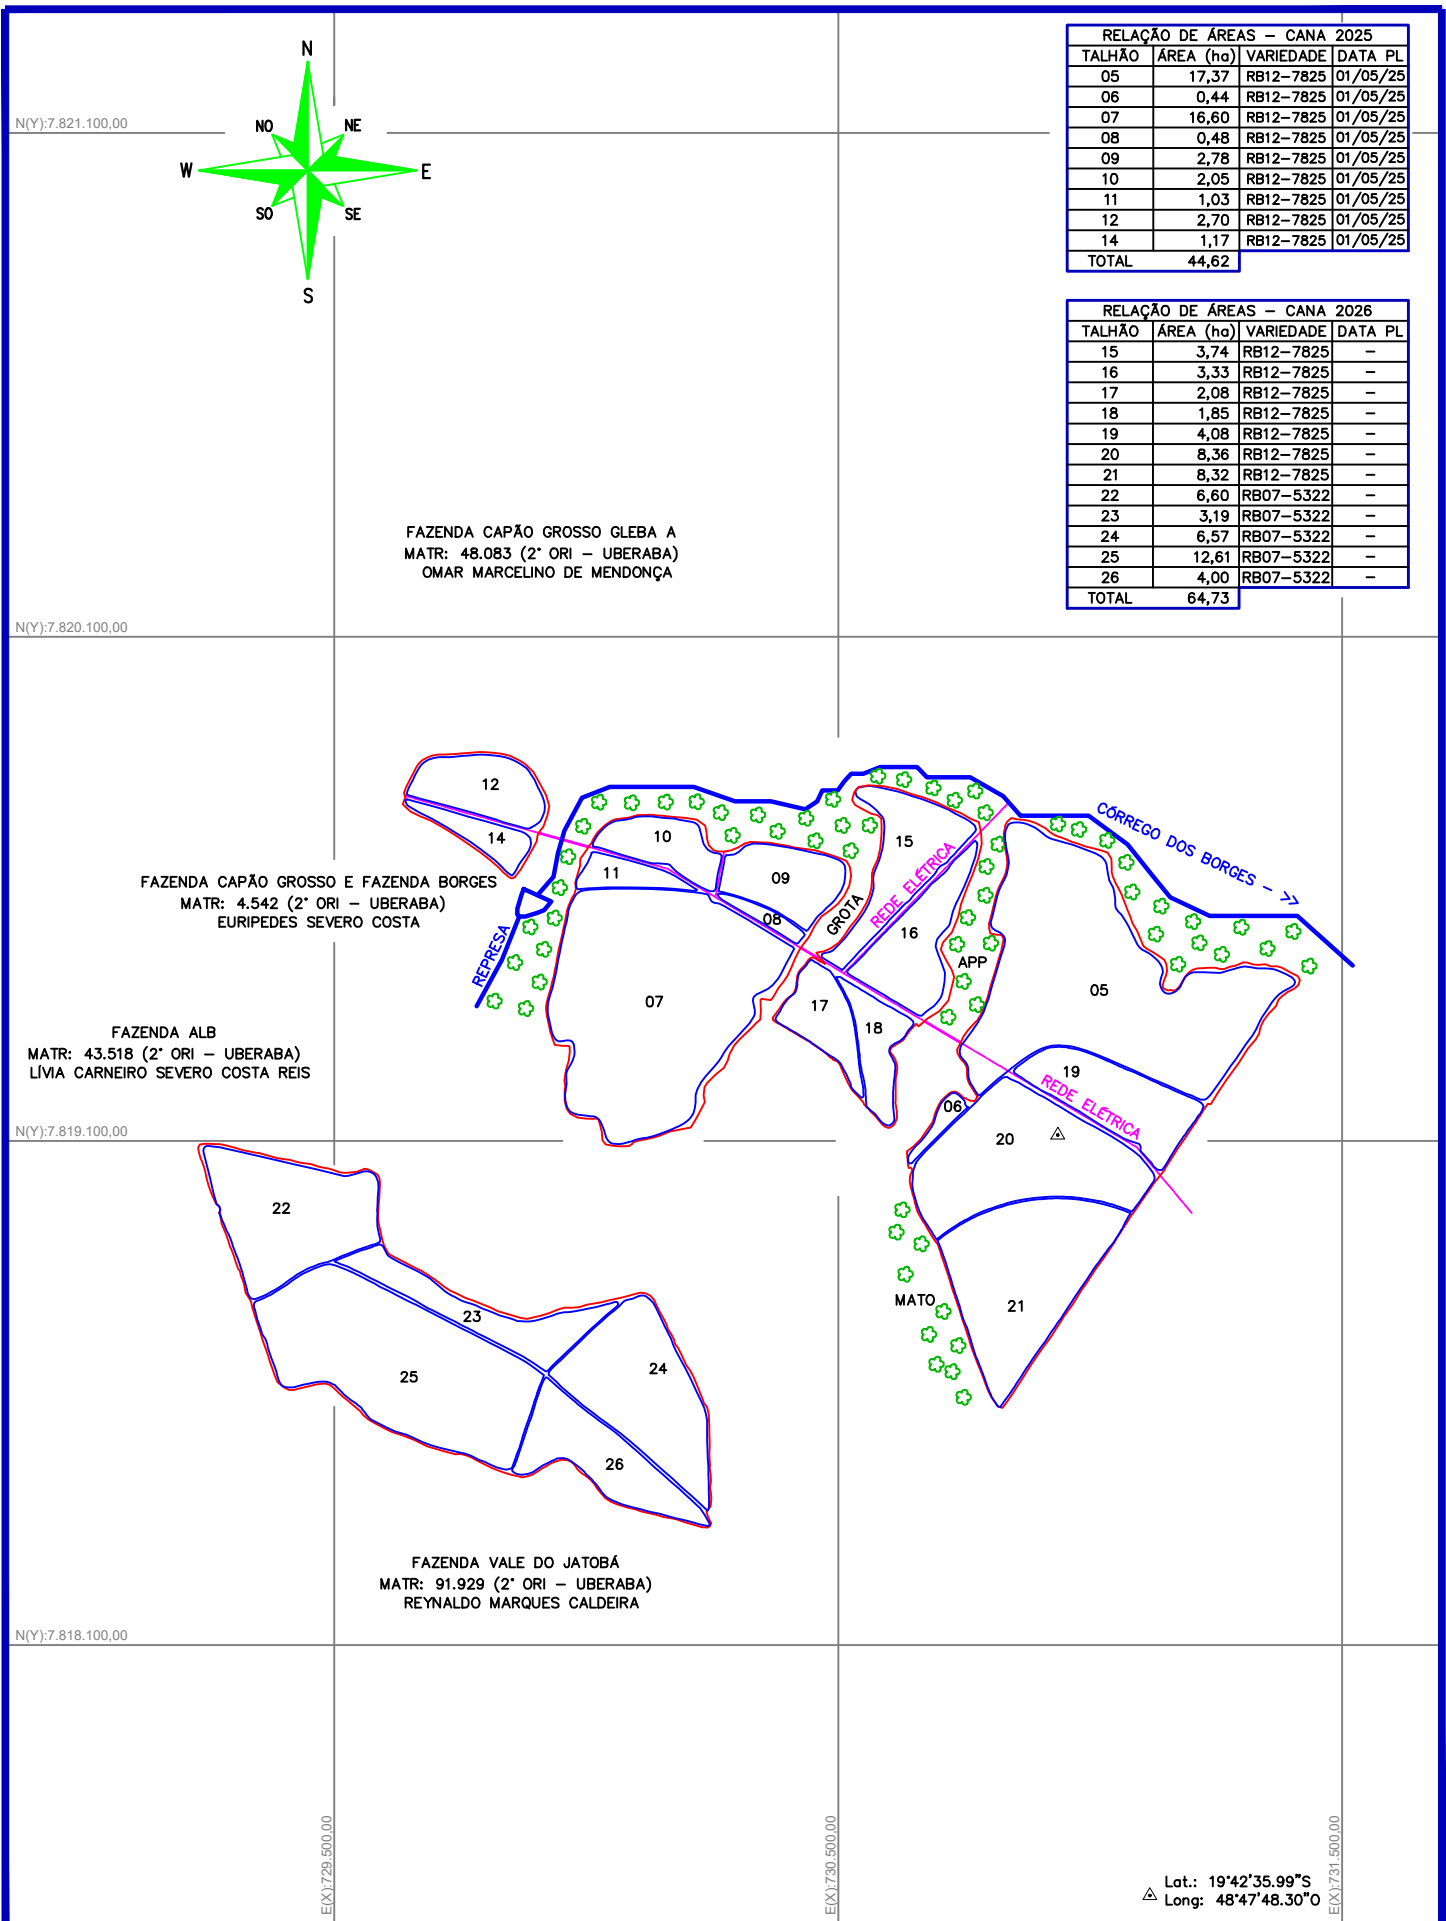

RELAÇÃO DE ÁREAS - CANA 2025			
TALHÃO	ÁREA (ha)	VARIEDADE	DATA PL
05	17,37	RB12-7825	01/05/25
06	0,44	RB12-7825	01/05/25
07	16,60	RB12-7825	01/05/25
08	0,48	RB12-7825	01/05/25
09	2,78	RB12-7825	01/05/25
10	2,05	RB12-7825	01/05/25
11	1,03	RB12-7825	01/05/25
12	2,70	RB12-7825	01/05/25
14	1,17	RB12-7825	01/05/25
TOTAL	44,62		

RELAÇÃO DE ÁREAS - CANA 2026			
TALHÃO	ÁREA (ha)	VARIEDADE	DATA PL
15	3,74	RB12-7825	-
16	3,33	RB12-7825	-
17	2,08	RB12-7825	-
18	1,85	RB12-7825	-
19	4,08	RB12-7825	-
20	8,36	RB12-7825	-
21	8,32	RB12-7825	-
22	6,60	RB07-5322	-
23	3,19	RB07-5322	-
24	6,57	RB07-5322	-
25	12,61	RB07-5322	-
26	4,00	RB07-5322	-
TOTAL	64,73		

 LEVANTAMENTO TOPOGRÁFICO	PROPRIEDADE: 940 – FAZENDA CRISTO REI	QUADRO DE ÁREAS (ha)	CANA 2026:	64,73	Desenhado por: YGOR DOS SANTOS	Data: 23/05/2026	Núcleo: 4 SANTA CLARA
	PROPRIETÁRIO: ANGELO JOSE DA SILVA FILHO		CARREADOR 2026:	4,71	Revisado por: —	Data: —	
	FORNECEDOR: SILVIO DE CASTRO CUNHA JUNIOR		CANA ANTIGA:	44,62	Responsável técnico: DANIEL CÉSAR DA SILVA		
	ÁREA TOTAL: 118,50 Hectares		CARREADOR ANTIGO:	4,44	Município: CAMPO FLORIDO	Escala: 1 : 15.000	Data Levant.: 15/05/2025