


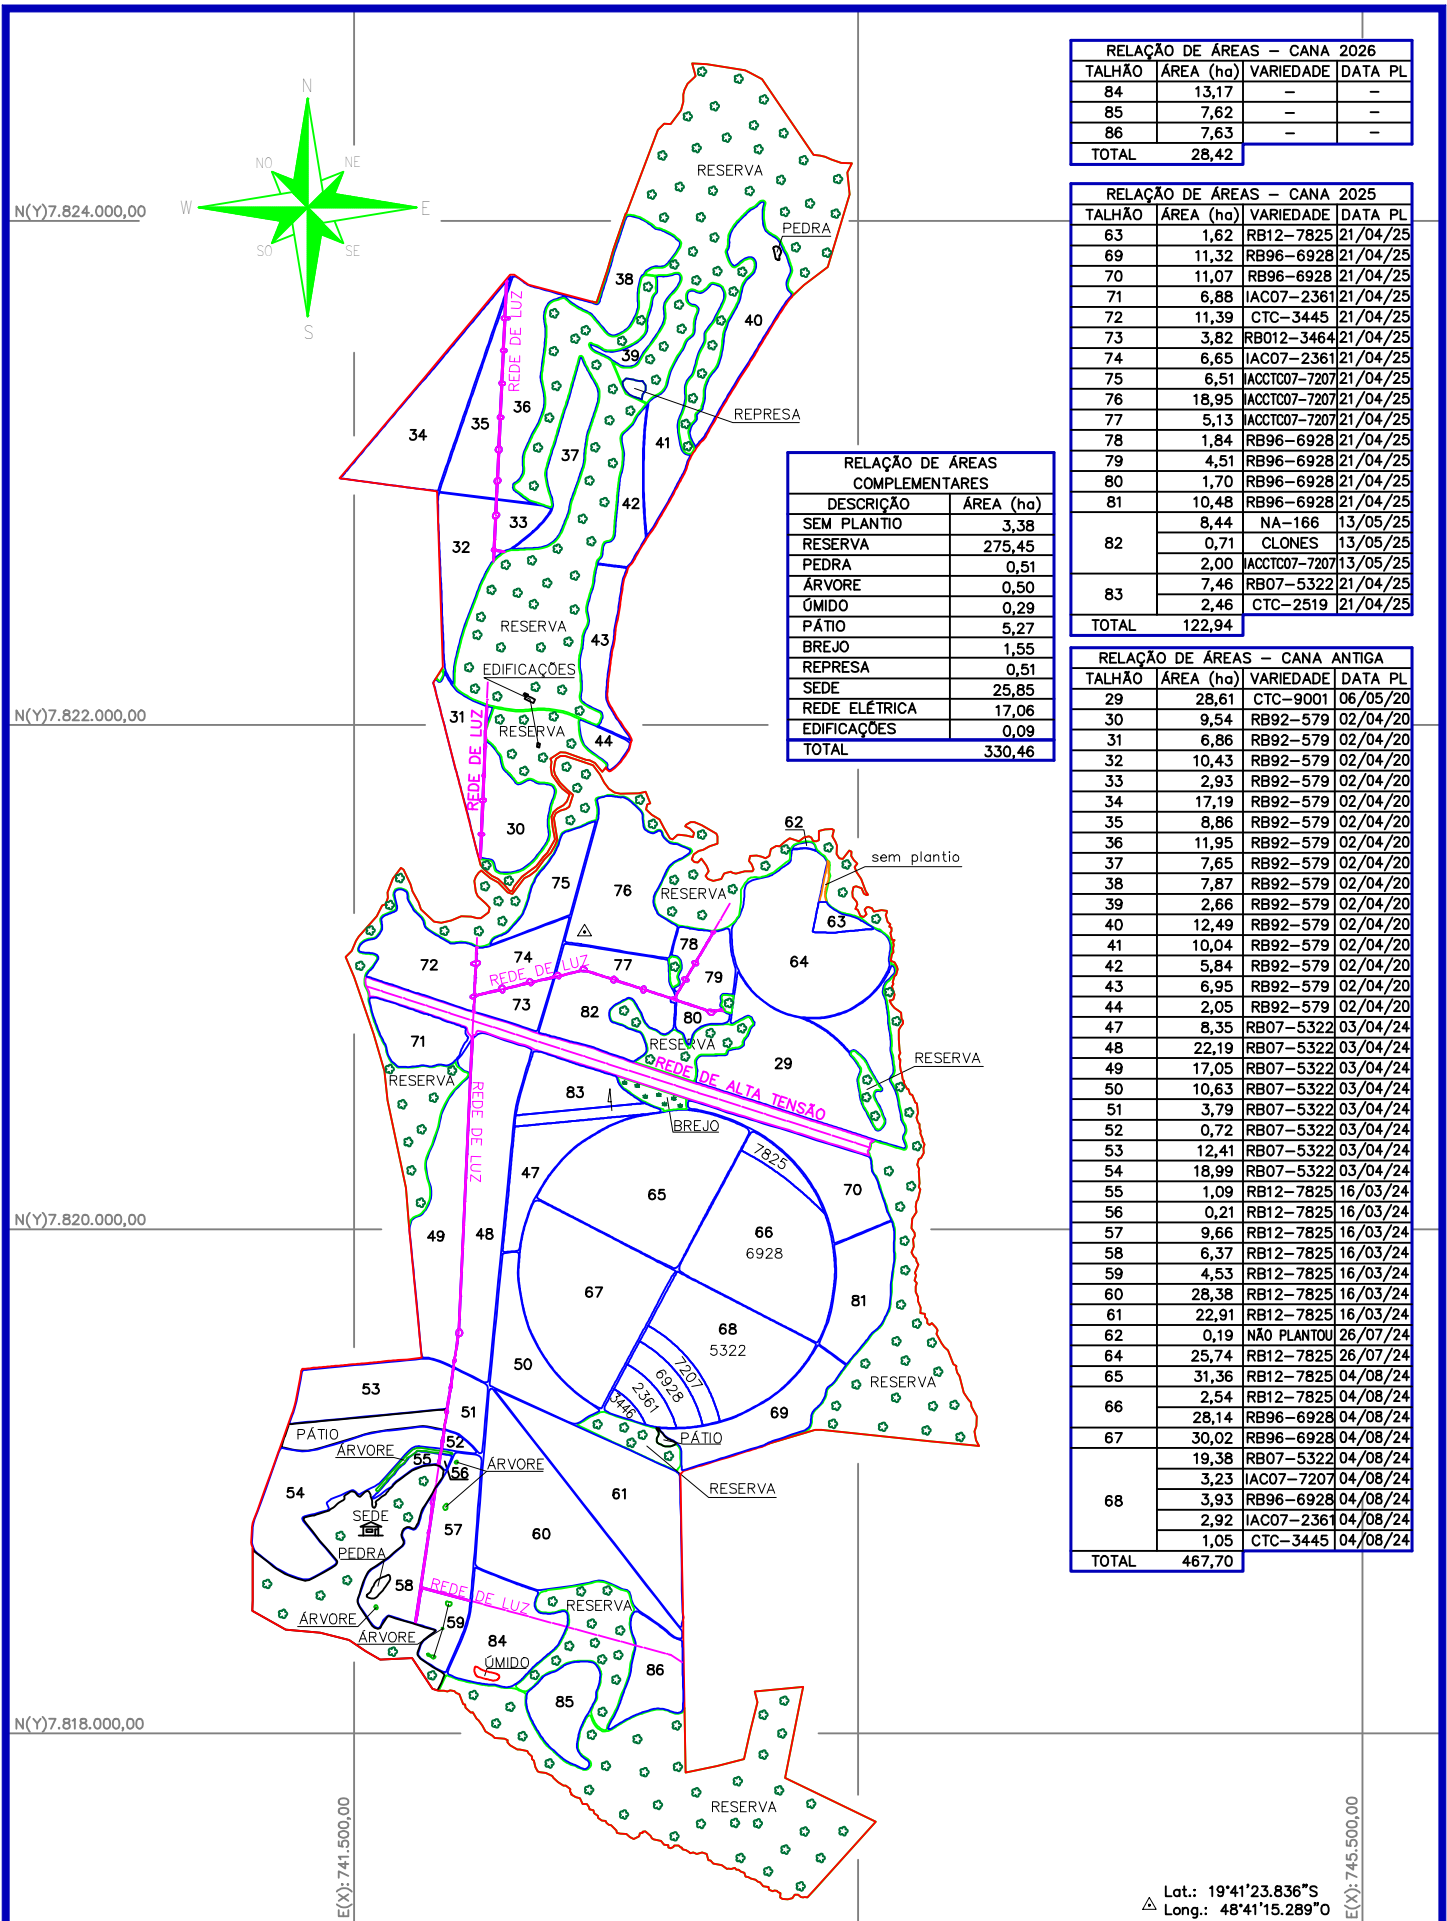

RELAÇÃO DE ÁREAS – CANA 2026			
TALHÃO	ÁREA (ha)	VARIIDADE	DATA PL
84	13,17	–	–
85	7,62	–	–
86	7,63	–	–
TOTAL		28,42	

RELAÇÃO DE ÁREAS – CANA 2025			
TALHÃO	ÁREA (ha)	VARIIDADE	DATA PL
63	1,62	RB12–7825	21/04/25
69	11,32	RB96–6928	21/04/25
70	11,07	RB96–6928	21/04/25
71	6,88	IAC07–2361	21/04/25
72	11,39	CTC–3445	21/04/25
73	3,82	RB012–3464	21/04/25
74	6,65	IAC07–2361	21/04/25
75	6,51	IACCT07–7207	21/04/25
76	18,95	IACCT07–7207	21/04/25
77	5,13	IACCT07–7207	21/04/25
78	1,84	RB96–6928	21/04/25
79	4,51	RB96–6928	21/04/25
80	1,70	RB96–6928	21/04/25
81	10,48	RB96–6928	21/04/25
82	8,44	NA–166	13/05/25
	0,71	CLONES	13/05/25
	2,00	IACCT07–7207	13/05/25
83	7,46	RB07–5322	21/04/25
	2,46	CTC–2519	21/04/25
TOTAL		122,94	

RELAÇÃO DE ÁREAS – CANA ANTIGA			
TALHÃO	ÁREA (ha)	VARIIDADE	DATA PL
29	28,61	CTC–9001	06/05/20
30	9,54	RB92–579	02/04/20
31	6,86	RB92–579	02/04/20
32	10,43	RB92–579	02/04/20
33	2,93	RB92–579	02/04/20
34	17,19	RB92–579	02/04/20
35	8,86	RB92–579	02/04/20
36	11,95	RB92–579	02/04/20
37	7,65	RB92–579	02/04/20
38	7,87	RB92–579	02/04/20
39	2,66	RB92–579	02/04/20
40	12,49	RB92–579	02/04/20
41	10,04	RB92–579	02/04/20
42	5,84	RB92–579	02/04/20
43	6,95	RB92–579	02/04/20
44	2,05	RB92–579	02/04/20
47	8,35	RB07–5322	03/04/24
48	22,19	RB07–5322	03/04/24
49	17,05	RB07–5322	03/04/24
50	10,63	RB07–5322	03/04/24
51	3,79	RB07–5322	03/04/24
52	0,72	RB07–5322	03/04/24
53	12,41	RB07–5322	03/04/24
54	18,99	RB07–5322	03/04/24
55	1,09	RB12–7825	16/03/24
56	0,21	RB12–7825	16/03/24
57	9,66	RB12–7825	16/03/24
58	6,37	RB12–7825	16/03/24
59	4,53	RB12–7825	16/03/24
60	28,38	RB12–7825	16/03/24
61	22,91	RB12–7825	16/03/24
62	0,19	NÃO PLANTOU	26/07/24
64	25,74	RB12–7825	26/07/24
65	31,36	RB12–7825	04/08/24
66	2,54	RB12–7825	04/08/24
	28,14	RB96–6928	04/08/24
	30,02	RB96–6928	04/08/24
	19,38	RB07–5322	04/08/24
	3,23	IAC07–7207	04/08/24
67	3,93	RB96–6928	04/08/24
	2,92	IAC07–2361	04/08/24
	1,05	CTC–3445	04/08/24
TOTAL		467,70	



LEVANTAMENTO TOPOGRÁFICO

PROPRIEDADE:
1148–FAZ BELLA ESPERANÇA VI

PROPRIETÁRIO:
ADEMIR FERREIRA DE MELLO JÚNIOR

FORNECEDOR:
ADEMIR FERREIRA DE MELLO JÚNIOR

ÁREA TOTAL:
974,20 Hectares

QUADRO DE ÁREAS (ha)

CANA 2026:	28,42
CARREADOR 2026:	1,43
CANA ANTIGA:	590,64
CARREADOR ANTIGO:	23,25
COMPLEMENTARES:	330,46

Desenhado por:
MÁRCIO GALASSI

Revisado por:

Engenheiro Agrimensor:
DANIEL CÉSAR DA SILVA

Município:
CAMPO FLORIDO – MG

Escala:
1 : 30.000

Data Levant.:
15/05/2026

Núcleo:
01
USINA

Lat.: 19°41'23.836"S
Long.: 48°41'15.289"O

Datum Sirgas2000 / UTM zona 22S (CM 51W)