


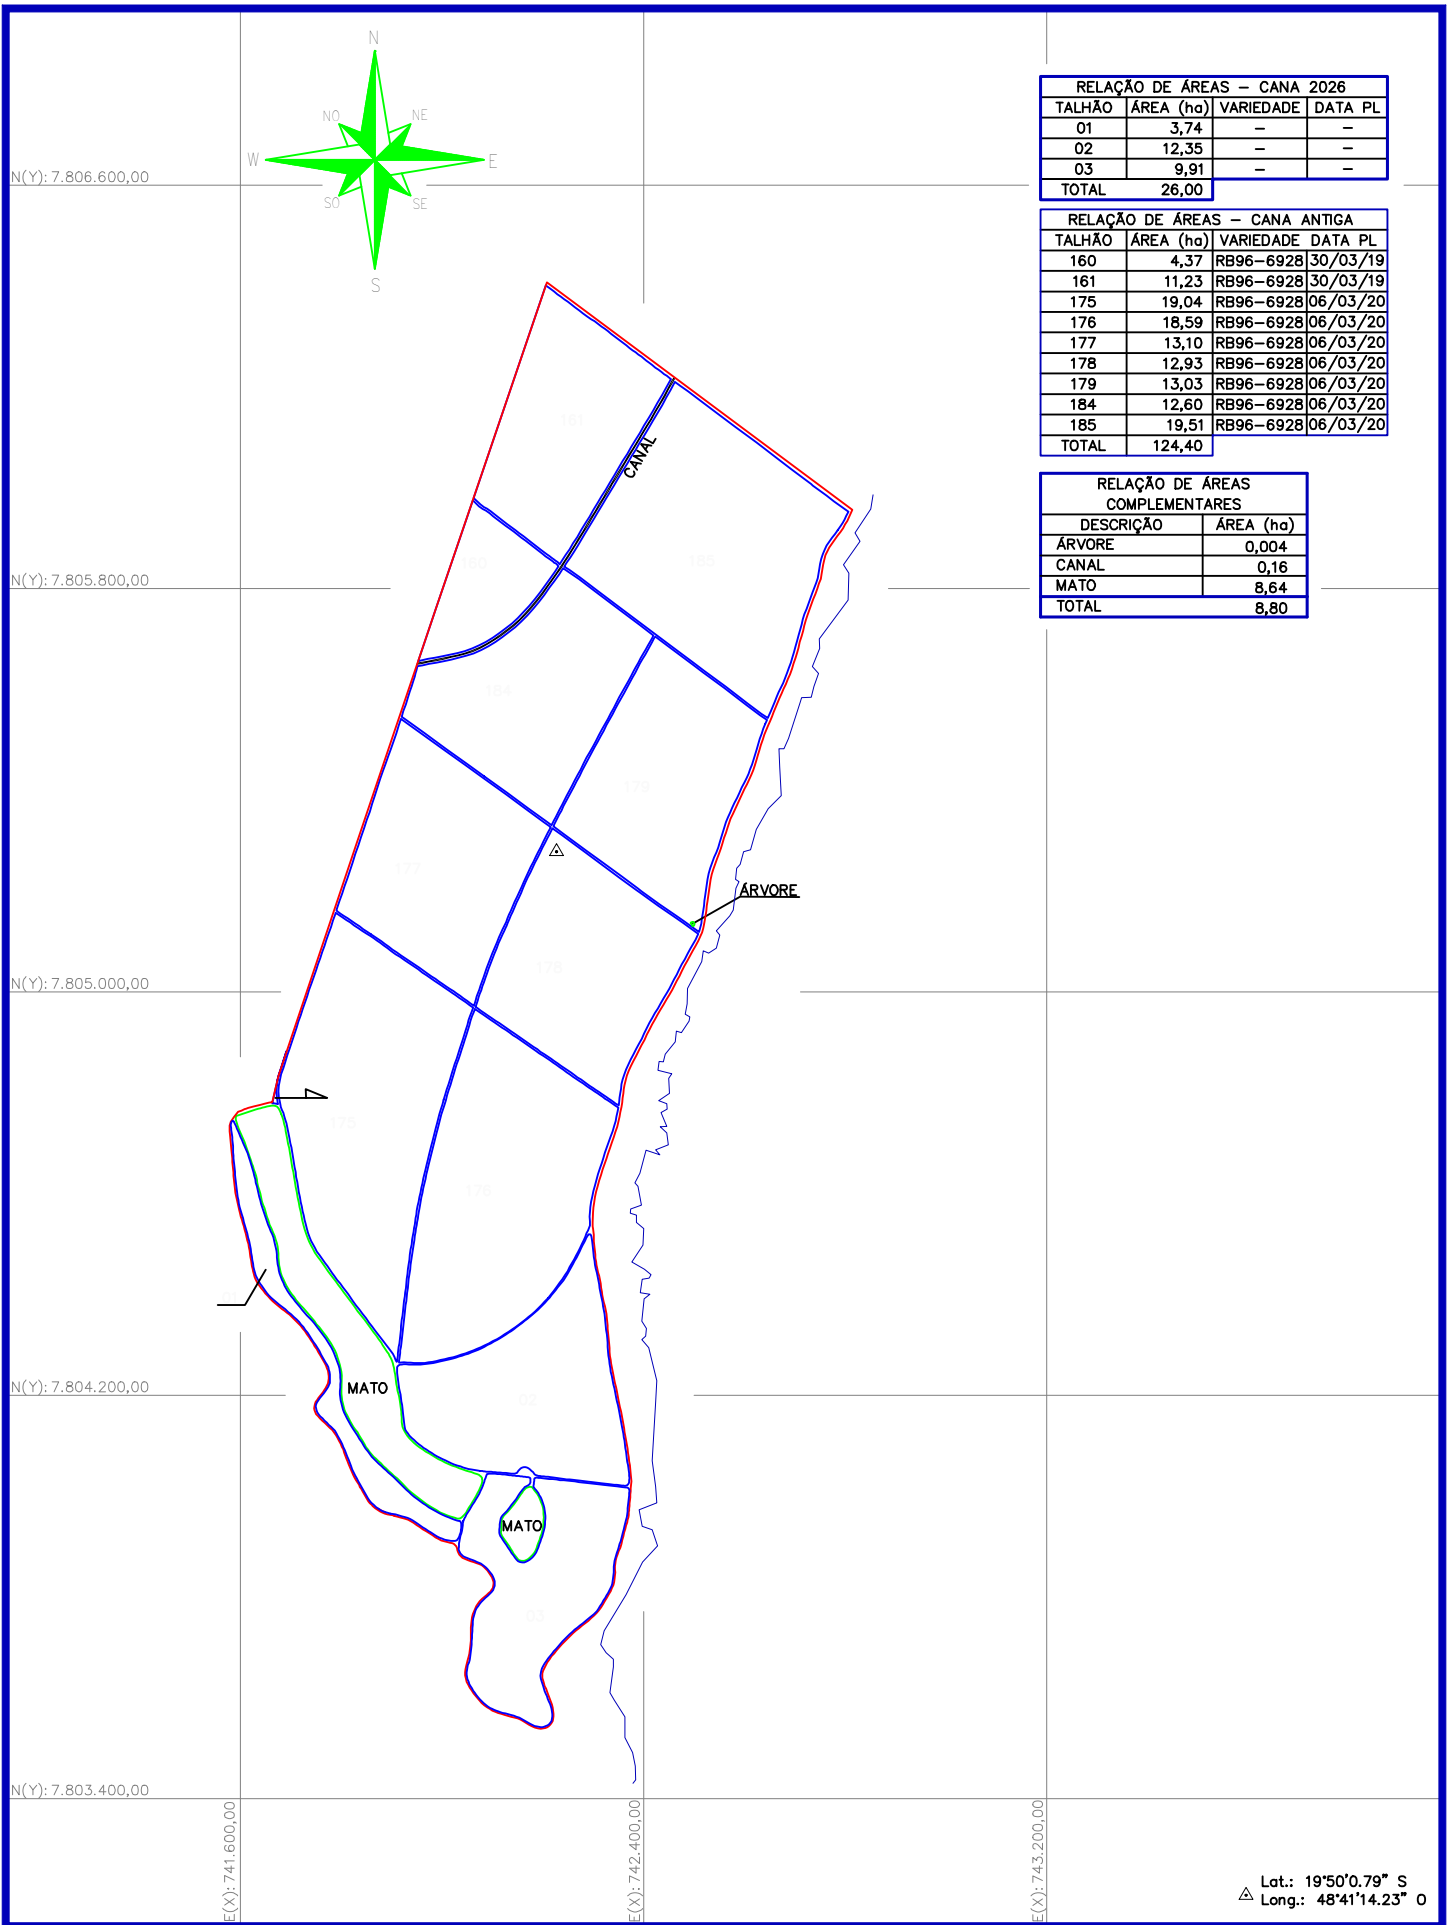

RELAÇÃO DE ÁREAS – CANA 2026			
TALHÃO	ÁREA (ha)	VARIEDADE	DATA PL
01	3,74	–	–
02	12,35	–	–
03	9,91	–	–
TOTAL		26,00	

RELAÇÃO DE ÁREAS – CANA ANTIGA			
TALHÃO	ÁREA (ha)	VARIEDADE	DATA PL
160	4,37	RB96–6928	30/03/19
161	11,23	RB96–6928	30/03/19
175	19,04	RB96–6928	06/03/20
176	18,59	RB96–6928	06/03/20
177	13,10	RB96–6928	06/03/20
178	12,93	RB96–6928	06/03/20
179	13,03	RB96–6928	06/03/20
184	12,60	RB96–6928	06/03/20
185	19,51	RB96–6928	06/03/20
TOTAL		124,40	

RELAÇÃO DE ÁREAS COMPLEMENTARES	
DESCRIÇÃO	ÁREA (ha)
ÁRVORE	0,004
CANAL	0,16
MATO	8,64
TOTAL	8,80

Lat.: 19°50'0.79" S
△ Long.: 48°41'14.23" O

 LEVANTAMENTO TOPOGRÁFICO	PROPRIEDADE: 1248 – SANTA ALBERTINA	QUADRO DE ÁREAS (ha)	CANA 2026:	26,00	Desenhado por: YGOR DOS SANTOS	Data: 25/05/2026	Núcleo: 1 USINA
	PROPRIETÁRIO: MONICA TENORIO WANDERLEY		CARREADOR 2026:	1,96	Atualizado por:	Data:	
	FORNECEDOR: ADEMIR FERREIRA DE MELLO		CANA ANTIGA:	124,40	Engenheiro Agrimensor: DANIEL CÉSAR DA SILVA		
	ÁREA TOTAL: 165,04 Hectares		CARREADOR ANTIGO:	3,88	Município: CAMPO FLORIDO	Escala: 1 : 15.000	Data Levant.: 05/2026
			COMPLEMENTARES:	8,80			