



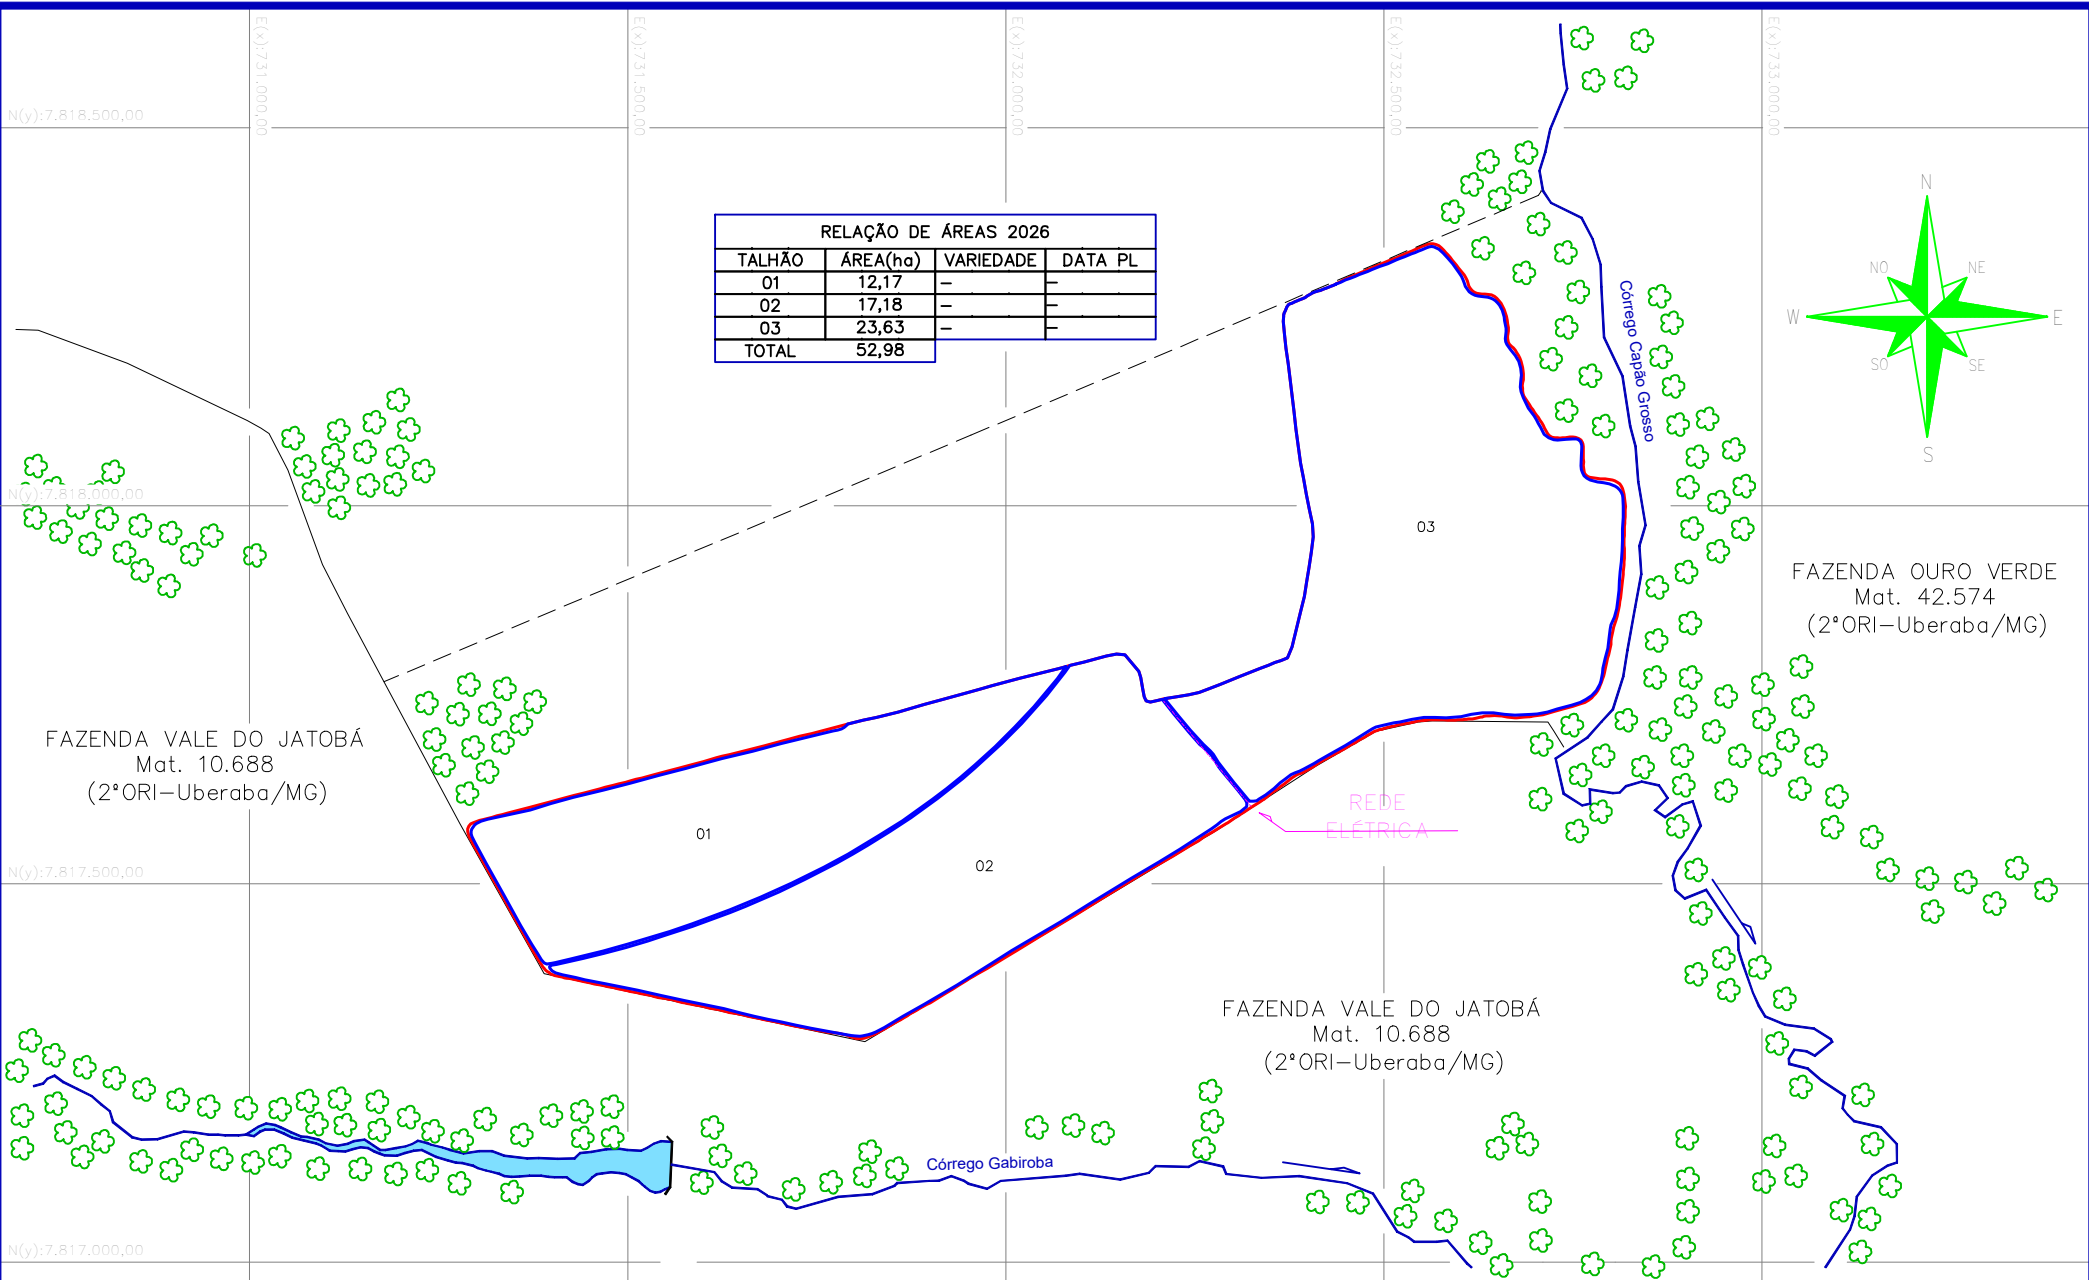

RELAÇÃO DE ÁREAS 2026			
TALHÃO	ÁREA(ha)	VARIEDADE	DATA PL
01	12,17	-	-
02	17,18	-	-
03	23,63	-	-
TOTAL	52,98		

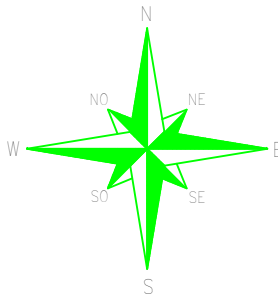

FAZENDA OURO VERDE
Mat. 42.574
(2°ORI-Uberaba/MG)

FAZENDA VALE DO JATOBÁ
Mat. 10.688
(2°ORI-Uberaba/MG)

FAZENDA VALE DO JATOBÁ
Mat. 10.688
(2°ORI-Uberaba/MG)

 LEVANTAMENTO TOPOGRÁFICO	PROPRIEDADE: 1269 — FAZENDA SANTA PAULA-SEBASTIAO BRAZ	CANA 2026:	52,98	Desenhado por: GLAUBER PIMENTEL	Data: 18/05/2026	Núcleo: 4
	PROPRIETÁRIO: ADEMIR FERREIRA DE MELLO	CARREADOR 2026:	1,22	Revisado por:	Data:	SANTA CLARA
	FORNECEDOR: ADEMIR FERREIRA DE MELLO			Engº Agrimensor: DANIEL CESAR DA SILVA		
	ÁREA TOTAL: 54,20 Hectares			Município: CAMPO FLORIDO	Escala: 1 : 10,000	Data Levant.: 15/05/2026