


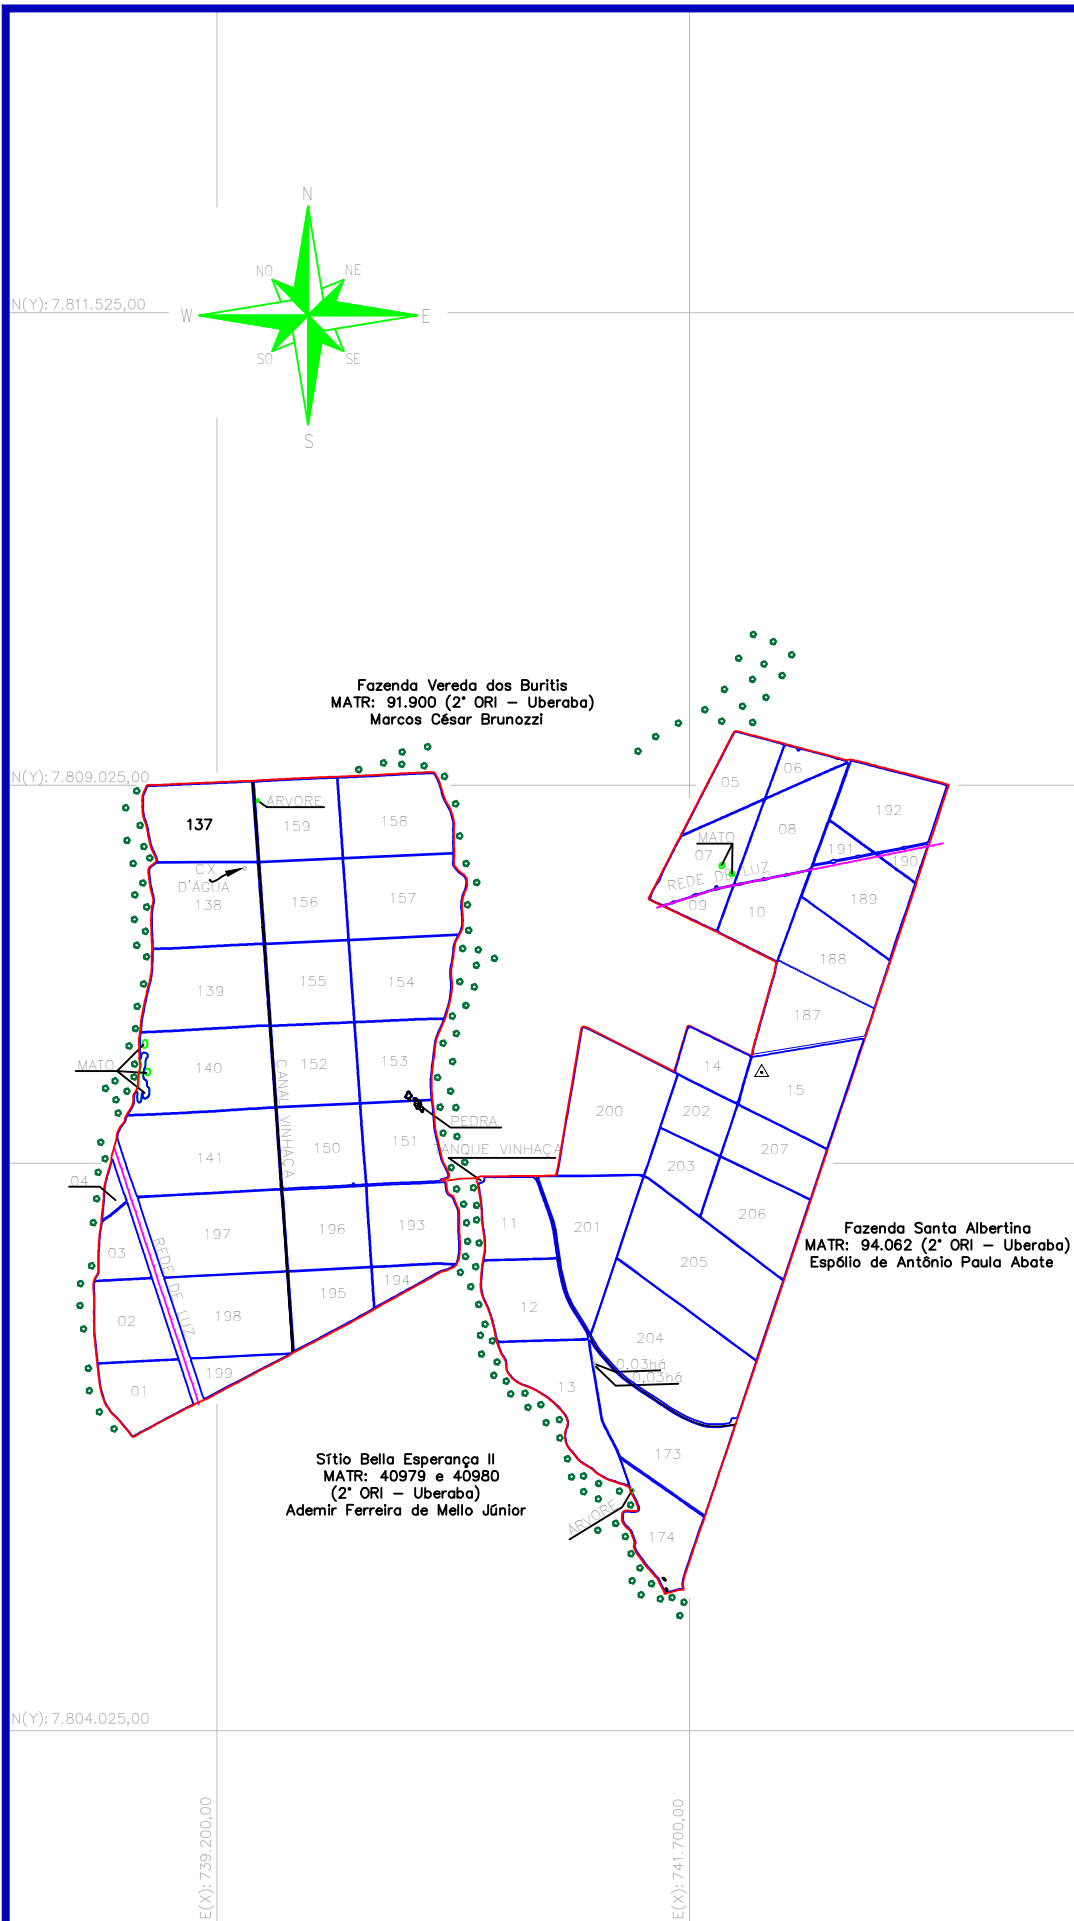

RELAÇÃO DE ÁREAS – CANA 2026			
TALHÃO	ÁREA (ha)	VARIEDADE	DATA PL
14	9,42	–	–
15	23,07	–	–
TOTAL	32,49		

RELAÇÃO DE ÁREAS – CANA 2023			
TALHÃO	ÁREA (ha)	VARIEDADE	DATA PL
01	14,14	RB96–6928	19/05/23
02	16,11	RB96–6928	19/05/23
03	7,86	RB96–6928	19/05/23
04	2,10	RB96–6928	19/05/23
05	13,49	RB96–6928	19/05/23
06	5,22	RB96–6928	19/05/23
07	15,86	RB96–6928	19/05/23
08	19,11	RB96–6928	19/05/23
09	4,08	RB96–6928	19/05/23
10	13,52	RB96–6928	19/05/23
11	15,08	RB96–6928	19/05/23
12	18,72	RB96–6928	19/05/23
13	21,69	RB96–6928	19/05/23
137	23,33	RB96–6928	15/03/2018
138	25,34	RB96–6928	15/03/2018
139	27,08	RB96–6928	15/03/2018
140	29,70	RB96–6928	15/03/2018
141	34,61	RB96–6928	15/03/2018
150	18,85	RB96–6928	11/04/2019
151	15,53	RB96–6928	11/04/2019
152	1,24	RB01–6916	11/04/2019
153	18,74	RB96–6928	11/04/2019
154	17,10	RB96–6928	11/04/2019
155	22,70	RB96–6928	11/04/2019
156	18,92	RB96–6928	11/04/2019
157	18,86	RB96–6928	11/04/2019
158	25,98	RB96–6928	11/04/2019
159	24,07	RB96–6928	11/04/2019
173	18,65	RB96–6928	11/04/2019
174	27,72	RB96–6928	06/03/2020
175	15,58	RB96–6928	06/03/2020
176	18,20	RB96–6928	06/03/2020
177	17,07	RB96–6928	06/03/2021
178	19,50	RB96–6928	06/03/2021
179	2,62	RB96–6928	06/03/2021
180	3,48	RB96–6928	06/03/2021
181	20,29	RB96–6928	06/03/2021
182	1,81	RB01–5985	06/03/2021
183	1,93	RB00–5014	06/03/2021
184	15,86	RB96–6928	06/03/2021
185	0,30	RB01–5985	06/03/2021
186	0,81	RB00–5014	06/03/2021
187	3,60	RB96–6928	06/03/2021
188	14,02	RB96–6928	06/03/2021
189	18,75	RB96–6928	06/03/2021
190	30,47	RB96–6928	05/04/2022
191	25,78	RB96–6928	05/04/2022
192	5,75	RB96–6928	05/04/2022
193	33,86	RB96–6928	05/04/2022
194	25,01	RB96–6928	05/04/2022
195	10,13	RB96–6928	05/04/2022
196	10,38	RB96–6928	05/04/2022
197	40,95	RB96–6928	05/04/2022
198	39,49	RB96–6928	05/04/2022
199	20,43	RB96–6928	05/04/2022
200	14,78	RB96–6928	05/04/2022
TOTAL	946,25		

RELAÇÃO DE ÁREAS COMPLEMENTARES	
DESCRIÇÃO	ÁREA (ha)
CANAL VINHAÇA	0,97
ÁRVORE	0,03
CAIXA D'ÁGUA	0,02
PEDRA	0,26
MATO	1,18
REDE DE LUZ	6,96
TOTAL	9,42

Lat.: 19°48'48.420"S
Long.: 48°41'20.243"O

 USINA CORUPIPE Flora Campo Florido	PROPRIEDADE: 479 – SANTA ALBERTINA	QUADRO DE ÁREAS (ha)	CANA 2026:	32,49	Desenhado por: MÁRCIO GALASSI	Data: 25/05/2026	Núcleo: 1 USINA
	PROPRIETÁRIO: ESPOLIO ANTÔNIO PAULO ABATE		CARREADOR 2026:	0,63	Atualizado por: –	Data: –	
	FORNECEDOR: ADEMIR FERREIRA DE MELLO		CANA ANTIGA:	946,25	Engº Agrimensor: DANIEL CESAR DA SILVA		
	ÁREA TOTAL: 1.017,00 Hectares		CARREADOR ANTIGO:	28,21	Município: CAMPO FLORIDO		
LEVANTAMENTO TOPOGRÁFICO			COMPLEMENTARES:	9,42	Escala: 1 : 40.000	Data Levant.: 20/05/2026	

Datum Sirgas2000 / UTM zona 22S (CM 51W)