


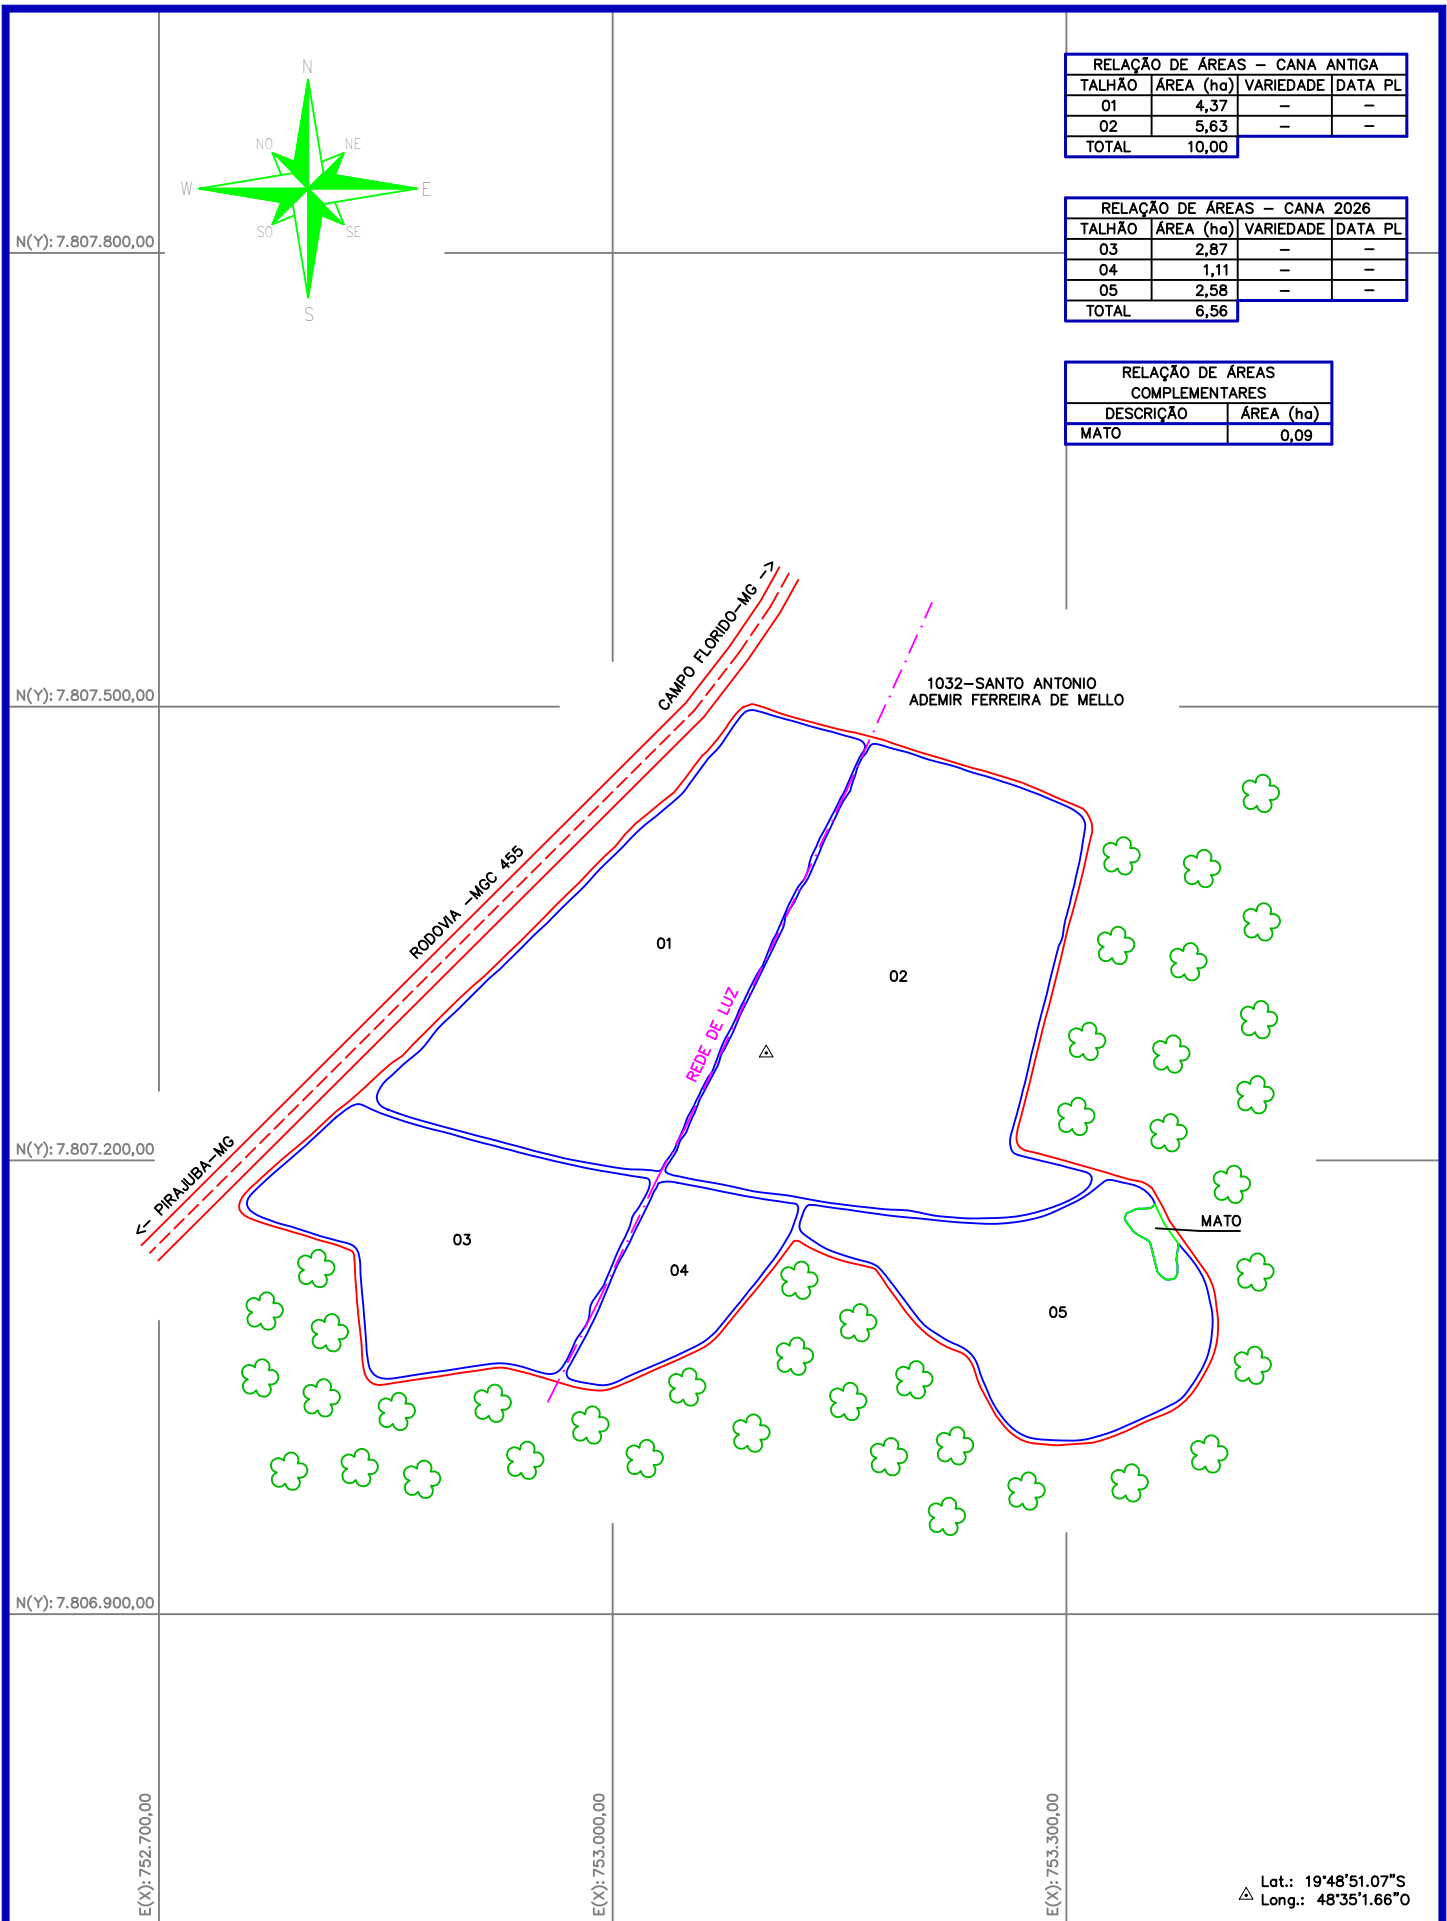

RELAÇÃO DE ÁREAS – CANA ANTIGA			
TALHÃO	ÁREA (ha)	VARIEDADE	DATA PL
01	4,37	–	–
02	5,63	–	–
TOTAL	10,00		

RELAÇÃO DE ÁREAS – CANA 2026			
TALHÃO	ÁREA (ha)	VARIEDADE	DATA PL
03	2,87	–	–
04	1,11	–	–
05	2,58	–	–
TOTAL	6,56		

RELAÇÃO DE ÁREAS COMPLEMENTARES	
DESCRIÇÃO	ÁREA (ha)
MATO	0,09

 LEVANTAMENTO TOPOGRÁFICO	PROPRIEDADE: 699 – FAZENDA BOA ESPERANÇA	QUADRO DE ÁREAS (ha)	CANA 2026:	6,56	Desenhado por: DOUGLAS WISTERSON	Data: 26/05/2026	Núcleo: 02 CAMPO FLORIDO	
	PROPRIETÁRIO: ADEMIR FERREIRA DE MELLO		CARREADOR 2026:	0,64	Atualizado por: —	Data: —		
	FORNECEDOR: ADEMIR FERREIRA DE MELLO		CANA ANTIGA:	10,00	Engenheiro Agrimensor: DANIEL CÉSAR DA SILVA			
	ÁREA TOTAL: 17,69 Hectares		CARREADOR ANTIGO:	0,40	Município: CAMPO FLORIDO—MG	Escala: 1 : 5.000	Data Levant.: 18/05/2026	
			COMPLEMENTARES:	0,09				

Obs.: Conferido perímetro georreferenciado.
Datum Sirgas2000 / UTM zona 22S (CM 51W)