


RELAÇÃO DE ÁREAS – CANA 2026			
TALHÃO	ÁREA (ha)	VARIEDADE	DATA PL
01	2,15	—	—
02	1,70	—	—
03	3,48	—	—
04	4,22	—	—
TOTAL		11,55	

RELAÇÃO DE ÁREAS – CANA ANTIGA			
TALHÃO	ÁREA (ha)	VARIEDADE	DATA PL
32	8,29	CTC-9001	15/03/21
33	8,43	CTC-9001	15/03/21
34	5,27	CTC-9001	15/03/21
35	6,09	RB12-7825	15/03/21
		RB97-5242	15/03/21
37	21,49	CTC-9001	01/03/22
39	0,81	RB97-5033	01/03/22
40	25,50	CTC-9001	01/03/22
41	15,54	CTC-9001	01/03/22
42	0,97	RB96-6928	01/05/25
43	4,51	RB96-6928	01/05/25
44	5,99	RB96-6928	01/05/25
TOTAL		102,89	

RELAÇÃO DE ÁREAS COMPLEMENTARES	
DESCRIÇÃO	ÁREA (ha)
MATO	7,23
REDE DE ALTA TENSÃO	2,76
TOTAL	9,99

N(Y): 7.817.600,00

N(Y): 7.816.900,00

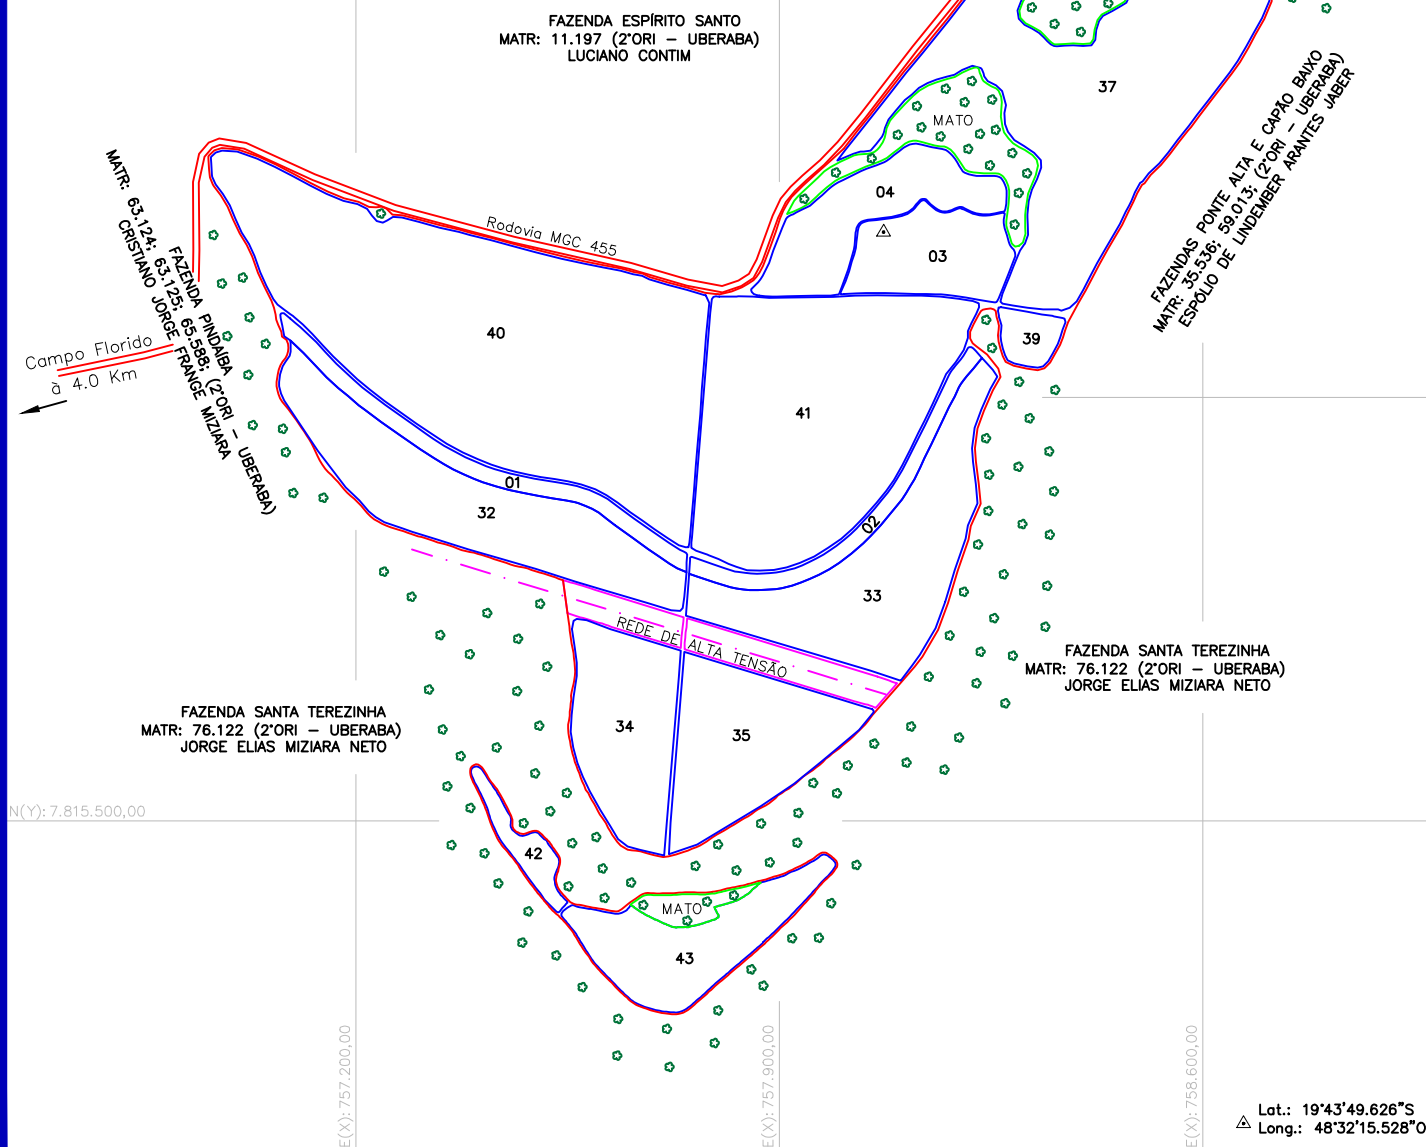

N(Y): 7.815.500,00

Lat.: 19°43'49.626"S
Long.: 48°32'15.528"O

 USINA CORUPIPE Filial Campo Florido	PROPRIEDADE: 211 – ESPÍRITO SANTO – MANOEL VITOR	QUADRO DE ÁREAS (ha)	CANA 2026:	11,55	Desenhado por: MÁRCIO GALASSI	Data: 27/05/2026	Núcleo: 2 CAMPO FLORIDO
	PROPRIETÁRIO: MANOEL VITOR CONTIM		CARREADOR 2026:	0,52	Revisado por: —	Data: —	
	FORNECEDOR: MANOEL VITOR CONTIM		CANA ANTIGA:	102,89	Engenheiro Agrimensor: DANIEL CÉSAR DA SILVA		
	LEVANTAMENTO TOPOGRÁFICO		ÁREA TOTAL: 130,71 Hectares	CARREADOR ANTIGO:	5,76	Município: CAMPO FLORIDO—MG	Escala: 1 : 12.500
COMPLEMENTARES:				9,99			