


| RELAÇÃO DE ÁREAS – CANA 2026 |           |           |         |
|------------------------------|-----------|-----------|---------|
| TALHÃO                       | ÁREA (ha) | VARIEDADE | DATA PL |
| 08                           | 14,23     | —         | —       |
| TOTAL                        |           | 14,23     |         |

| RELAÇÃO DE ÁREAS – CANA ANTIGA |           |                   |          |
|--------------------------------|-----------|-------------------|----------|
| TALHÃO                         | ÁREA (ha) | VARIEDADE         | DATA PL  |
| 02                             | 10,48     | CV 7870           | 10/04/23 |
| 03                             | 18,76     | CV 7870           | 10/04/23 |
| 04                             | 10,94     | CV 7870 e RB 7825 | 15/04/23 |
| 05                             | 10,83     | CV 7870 e RB 7825 | 15/04/23 |
| 06                             | 1,16      | CV 7870 e RB 7825 | 15/04/23 |
| 07                             | 0,27      | CV 7870           | 01/05/25 |
| 10                             | 1,54      | CV 7870 e RB 7825 | 15/04/23 |
| 11                             | 2,54      | CV 7870 e RB 7825 | 15/04/23 |
| 12                             | 3,46      | CV 7870           | 01/05/25 |
| 19                             | 0,42      | RB03–6088         | ---      |
| 20                             | 0,68      | RB03–6088         | ---      |
| TOTAL                          |           | 61,08             |          |

| RELAÇÃO DE ÁREAS COMPLEMENTARES |           |
|---------------------------------|-----------|
| DESCRIÇÃO                       | ÁREA (ha) |
| MATO                            | 0,20      |
| TOTAL                           | 0,20      |

NCY>7.820.700,00

NCY>7.819.700,00

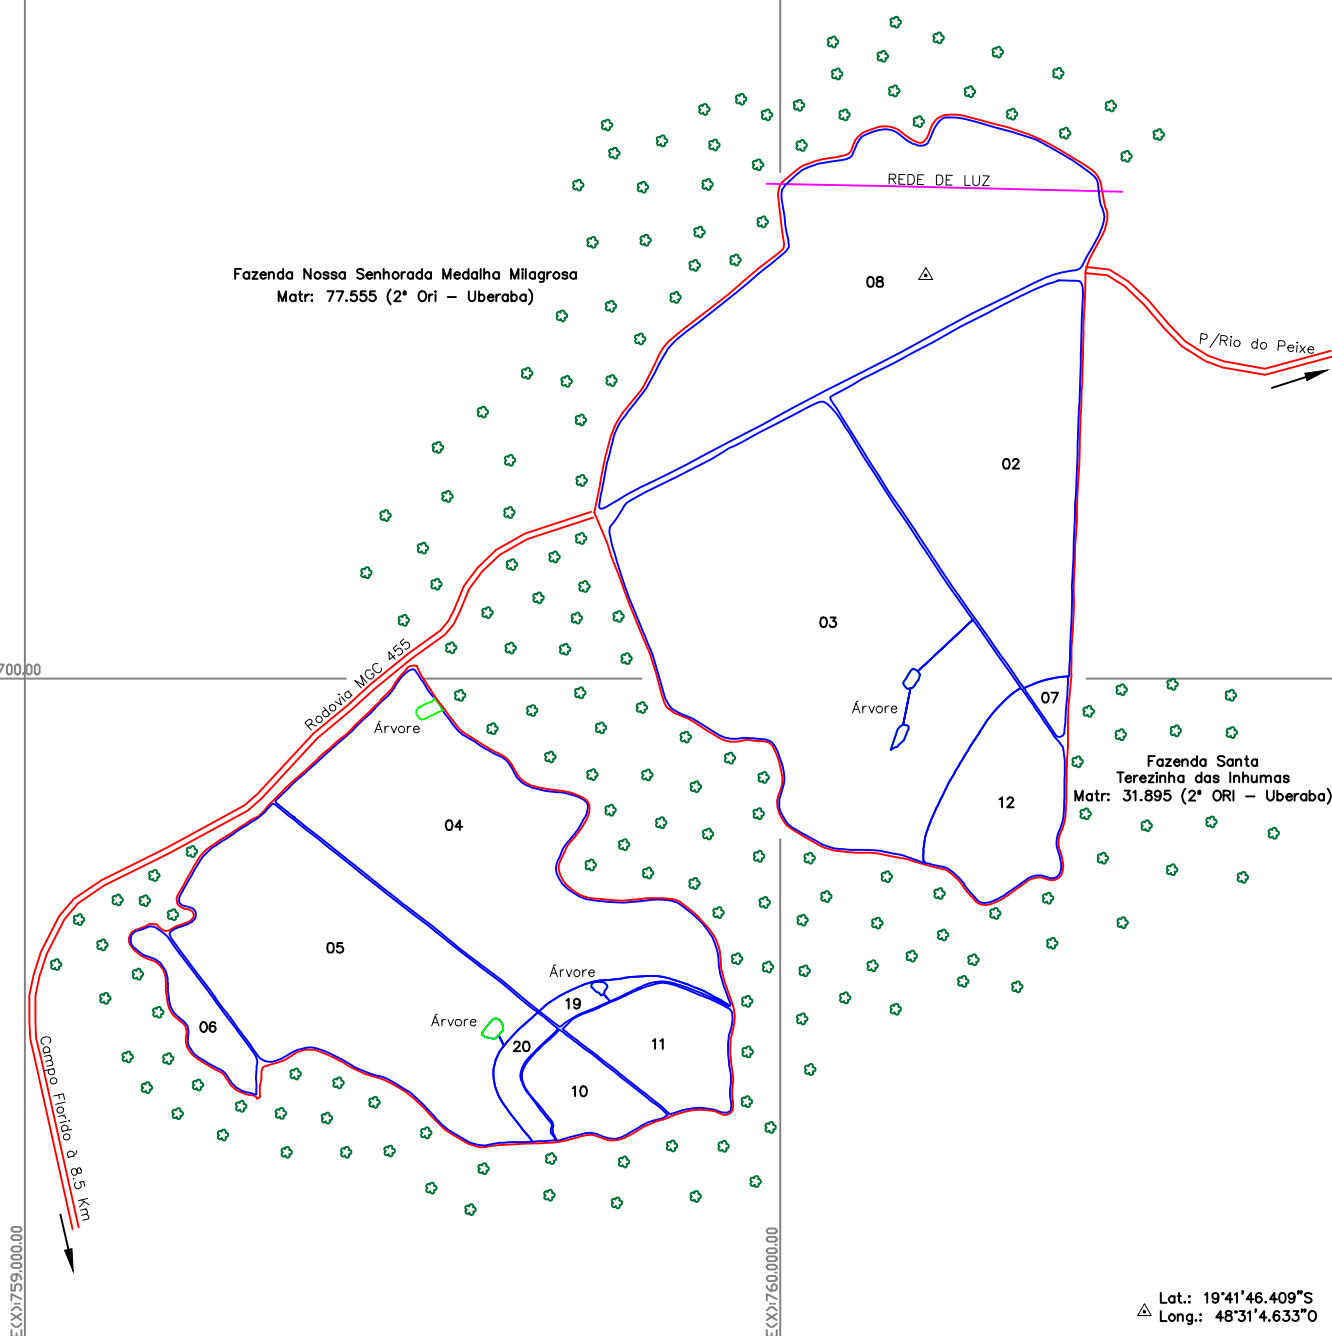

Lat.: 19°41'46.409"S  
△ Long.: 48°31'4.633"O



PROPRIEDADE:  
960 – INHUMAS  
PROPRIETÁRIO:  
LUCIANA ADRIANO FRANCO  
FORNECEDOR:  
MANOEL VITOR CONTIM  
ÁREA TOTAL:  
78,41 Hectares

LEVANTAMENTO TOPOGRÁFICO

QUADRO DE ÁREAS (ha)

|                   |       |
|-------------------|-------|
| CANA 2026:        | 14,23 |
| CARREADOR 2026:   | 0,52  |
| CANA ANTIGA:      | 61,08 |
| CARREADOR ANTIGO: | 2,38  |
| COMPLEMENTARES:   | 0,20  |

Desenhado por:  
MÁRCIO GALASSI  
Revisado por:  
—  
Engº Agrimensor:  
DANIEL CESAR DA SILVA  
Município:  
CAMPO FLORIDO  
Escala:  
1 : 10.000

Núcleo:  
02  
CAMPO FLORIDO  
Data Levant.:  
05/2026

Datum Sirgas2000