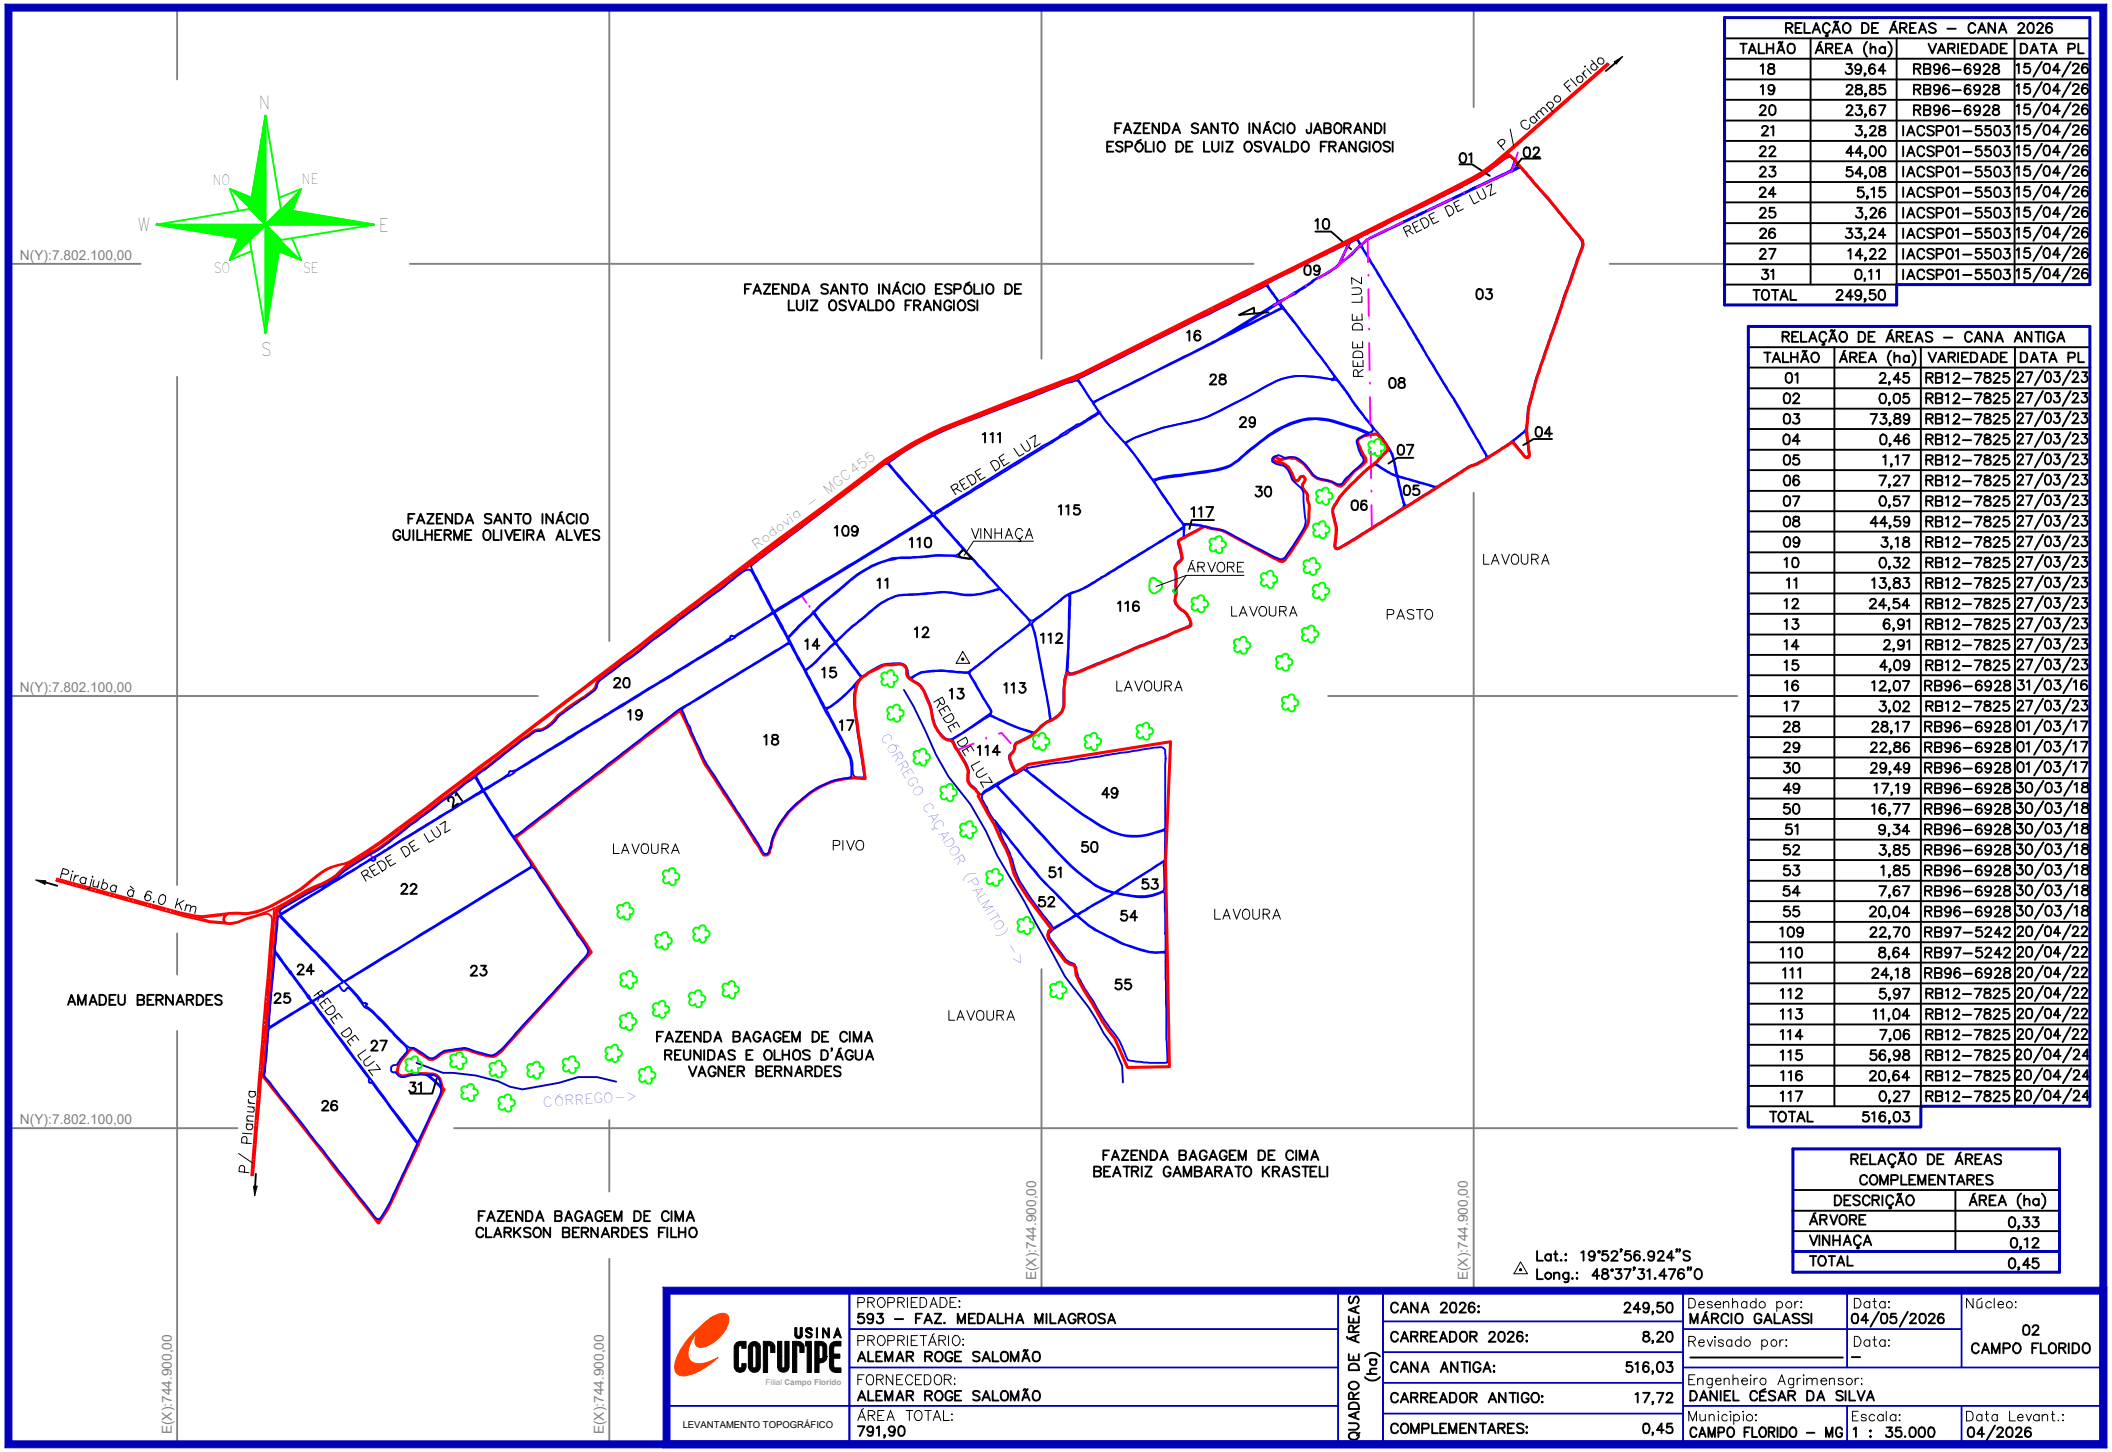


RELAÇÃO DE ÁREAS – CANA 2026			
TALHÃO	ÁREA (ha)	VARIEDADE	DATA PL
18	39,64	RB96-6928	15/04/26
19	28,85	RB96-6928	15/04/26
20	23,67	RB96-6928	15/04/26
21	3,28	IACSP01-5503	15/04/26
22	44,00	IACSP01-5503	15/04/26
23	54,08	IACSP01-5503	15/04/26
24	5,15	IACSP01-5503	15/04/26
25	3,26	IACSP01-5503	15/04/26
26	33,24	IACSP01-5503	15/04/26
27	14,22	IACSP01-5503	15/04/26
31	0,11	IACSP01-5503	15/04/26
TOTAL	249,50		

RELAÇÃO DE ÁREAS – CANA ANTIGA			
TALHÃO	ÁREA (ha)	VARIEDADE	DATA PL
01	2,45	RB12-7825	27/03/23
02	0,05	RB12-7825	27/03/23
03	73,89	RB12-7825	27/03/23
04	0,46	RB12-7825	27/03/23
05	1,17	RB12-7825	27/03/23
06	7,27	RB12-7825	27/03/23
07	0,57	RB12-7825	27/03/23
08	44,59	RB12-7825	27/03/23
09	3,18	RB12-7825	27/03/23
10	0,32	RB12-7825	27/03/23
11	13,83	RB12-7825	27/03/23
12	24,54	RB12-7825	27/03/23
13	6,91	RB12-7825	27/03/23
14	2,91	RB12-7825	27/03/23
15	4,09	RB12-7825	27/03/23
16	12,07	RB96-6928	31/03/16
17	3,02	RB12-7825	27/03/23
28	28,17	RB96-6928	01/03/17
29	22,86	RB96-6928	01/03/17
30	29,49	RB96-6928	01/03/17
49	17,19	RB96-6928	30/03/18
50	16,77	RB96-6928	30/03/18
51	9,34	RB96-6928	30/03/18
52	3,85	RB96-6928	30/03/18
53	1,85	RB96-6928	30/03/18
54	7,67	RB96-6928	30/03/18
55	20,04	RB96-6928	30/03/18
109	22,70	RB97-5242	20/04/22
110	8,64	RB97-5242	20/04/22
111	24,18	RB96-6928	20/04/22
112	5,97	RB12-7825	20/04/22
113	11,04	RB12-7825	20/04/22
114	7,06	RB12-7825	20/04/22
115	56,98	RB12-7825	20/04/24
116	20,64	RB12-7825	20/04/24
117	0,27	RB12-7825	20/04/24
TOTAL	516,03		

RELAÇÃO DE ÁREAS COMPLEMENTARES	
DESCRIÇÃO	ÁREA (ha)
ÁRVORE	0,33
VINHAÇA	0,12
TOTAL	0,45

Lat.: 19°52'56.924"S
Long.: 48°37'31.476"O

USINA CORURIPE
Filial Campo Florido

LEVANTAMENTO TOPOGRÁFICO

PROPRIEDADE: 593 – FAZ. MEDALHA MILAGROSA
PROPRIETÁRIO: ALEMAR ROGE SALOMÃO
FORNECEDOR: ALEMAR ROGE SALOMÃO
ÁREA TOTAL: 791,90

QUADRO DE ÁREAS (ha)

CANA 2026:	249,50
CARREADOR 2026:	8,20
CANA ANTIGA:	516,03
CARREADOR ANTIGO:	17,72
COMPLEMENTARES:	0,45

Desenhado por: MÁRCIO GALASSI | Data: 04/05/2026
Revisado por: ——— | Data: –
Núcleo: 02 CAMPO FLORIDO
Engenheiro Agrimensor: DANIEL CÉSAR DA SILVA
Município: CAMPO FLORIDO – MG | Escala: 1 : 35.000 | Data Levant.: 04/2026

Datum Sirgas2000 / UTM zona 22S (CM 51W)