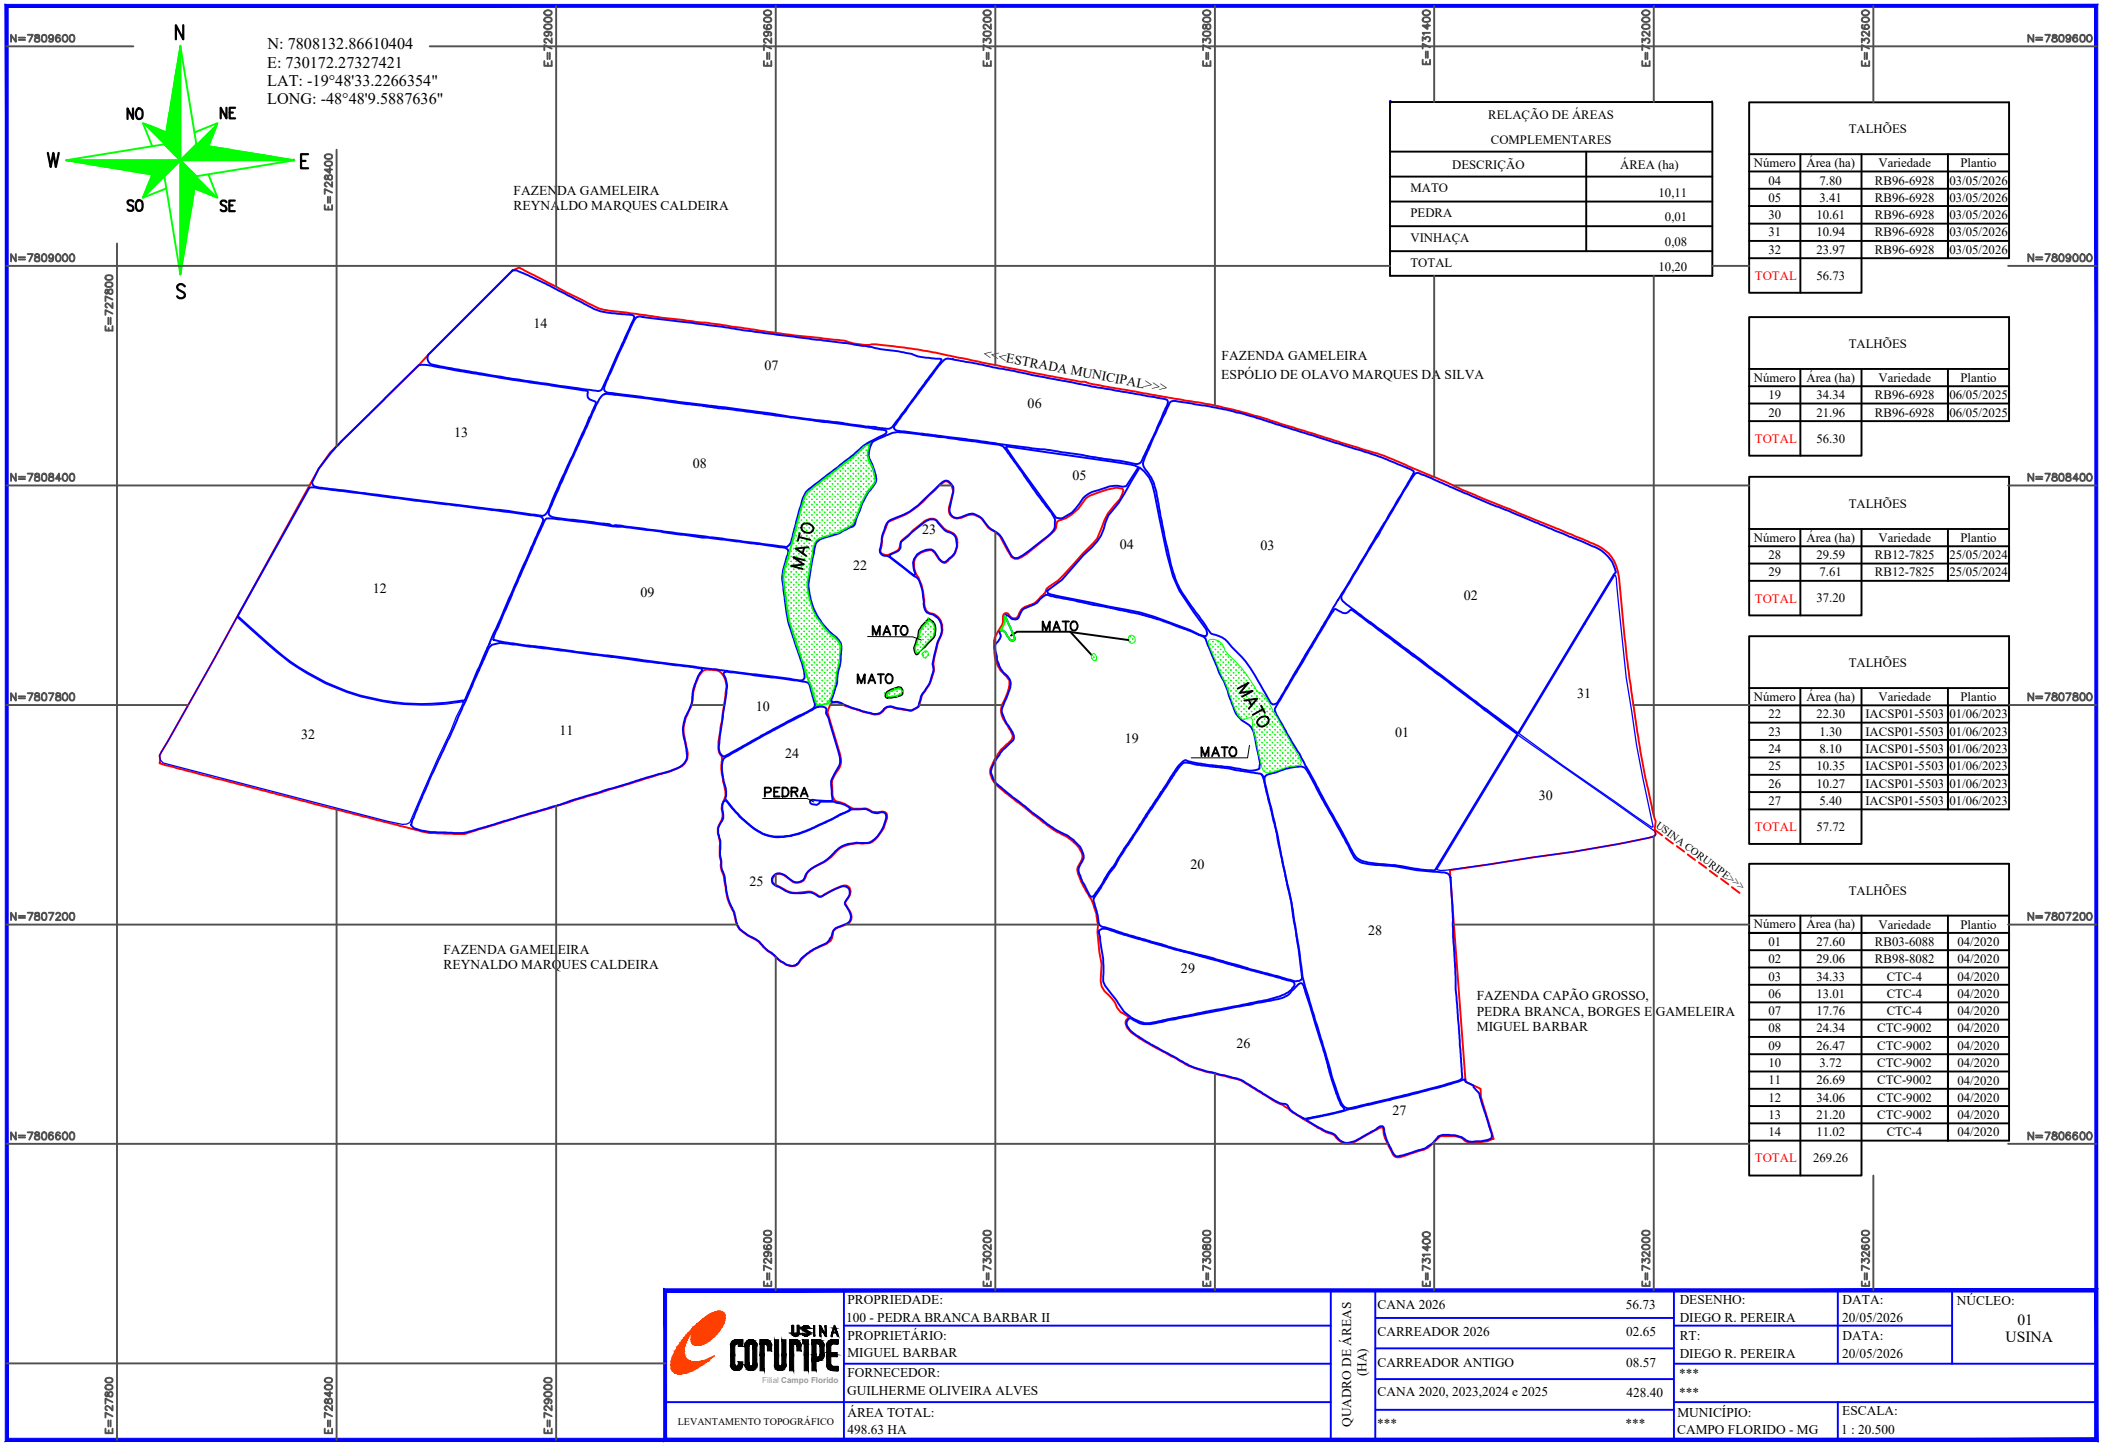

RELAÇÃO DE ÁREAS COMPLEMENTARES	
DESCRIÇÃO	ÁREA (ha)
MATO	10,11
PEDRA	0,01
VINHAÇA	0,08
TOTAL	10,20

TALHÕES

Número	Área (ha)	Variedade	Plantio
04	7.80	RB96-6928	03/05/2026
05	3.41	RB96-6928	03/05/2026
30	10.61	RB96-6928	03/05/2026
31	10.94	RB96-6928	03/05/2026
32	23.97	RB96-6928	03/05/2026
TOTAL	56.73		

TALHÕES

Número	Área (ha)	Variedade	Plantio
19	34.34	RB96-6928	06/05/2025
20	21.96	RB96-6928	06/05/2025
TOTAL	56.30		

TALHÕES

Número	Área (ha)	Variedade	Plantio
28	29.59	RB12-7825	25/05/2024
29	7.61	RB12-7825	25/05/2024
TOTAL	37.20		

TALHÕES

Número	Área (ha)	Variedade	Plantio
22	22.30	IACSP01-5503	01/06/2023
23	1.30	IACSP01-5503	01/06/2023
24	8.10	IACSP01-5503	01/06/2023
25	10.35	IACSP01-5503	01/06/2023
26	10.27	IACSP01-5503	01/06/2023
27	5.40	IACSP01-5503	01/06/2023
TOTAL	57.72		

TALHÕES

Número	Área (ha)	Variedade	Plantio
01	27.60	RB03-6088	04/2020
02	29.06	RB98-8082	04/2020
03	34.33	CTC-4	04/2020
06	13.01	CTC-4	04/2020
07	17.76	CTC-4	04/2020
08	24.34	CTC-9002	04/2020
09	26.47	CTC-9002	04/2020
10	3.72	CTC-9002	04/2020
11	26.69	CTC-9002	04/2020
12	34.06	CTC-9002	04/2020
13	21.20	CTC-9002	04/2020
14	11.02	CTC-4	04/2020
TOTAL	269.26		

USINA CORURIPE
Filial Campo Florido

LEVANTAMENTO TOPOGRÁFICO

PROPRIEDADE:
100 - PEDRA BRANCA BARBAR II

PROPRIETÁRIO:
MIGUEL BARBAR

FORNECEDOR:
GUILHERME OLIVEIRA ALVES

ÁREA TOTAL:
498.63 HA

QUADRO DE ÁREAS (HA)

CANA 2026	56.73
CARREADOR 2026	02.65
CARREADOR ANTIGO	08.57
CANA 2020, 2023,2024 e 2025	428.40
***	***

DESENHO: DIEGO R. PEREIRA
DATA: 20/05/2026
RT: DIEGO R. PEREIRA
DATA: 20/05/2026
***
***
MUNICÍPIO: CAMPO FLORIDO - MG
ESCALA: 1 : 20.500
NÚCLEO: 01 USINA

Datum Sirgas2000