


N(Y): 7.847.650

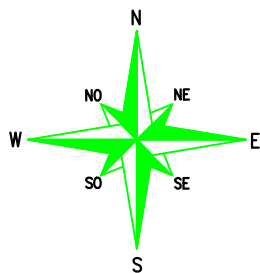


N(Y): 7.846.900

N(Y): 7.846.150

RELAÇÃO DE ÁREAS			
TALHÃO	ÁREA (ha)	VARIEDADE	DATA PL
1	8,94	RB12-7825	04/2026
2	0,80	RB92-579	03/2025
3	28,38	RB92-579	03/2025
4	10,64	RB12-7825	04/2026
5	7,66	RB12-7825	04/2026
6	22,50	RB12-7825	04/2026
7	9,34	RB12-7825	04/2026
8	7,68	RB12-7825	04/2026
9	2,87	RB12-7825	04/2026
10	5,93	RB12-7825	04/2026
11	5,88	RB12-7825	04/2026
12	1,25	RB12-7825	04/2026
13	0,61	RB12-7825	04/2026
14	1,05	RB12-7825	04/2026
15	1,34	RB12-7825	04/2026
16	3,19	RB12-7825	04/2026
17	3,29	RB12-7825	04/2026
TOTAL		121,35	

RELAÇÃO DE ÁREAS			
TALHÃO	ÁREA (ha)	VARIEDADE	DATA PL
21	9,91	RB12-7825	04/2024
22	3,92	RB12-7825	04/2024
23	13,05	RB12-7825	04/2024
24	1,37	RB12-7825	04/2024
25	1,44	RB12-7825	04/2024
26	2,60	RB12-7825	04/2024
27	2,47	RB12-7825	04/2024
TOTAL		34,76	

RELAÇÃO DE ÁREAS COMPLEMENTARES	
DESCRIÇÃO	ÁREA (ha)
BARREIRA	0,04
ÁRVORES	0,04
TOTAL	0,08

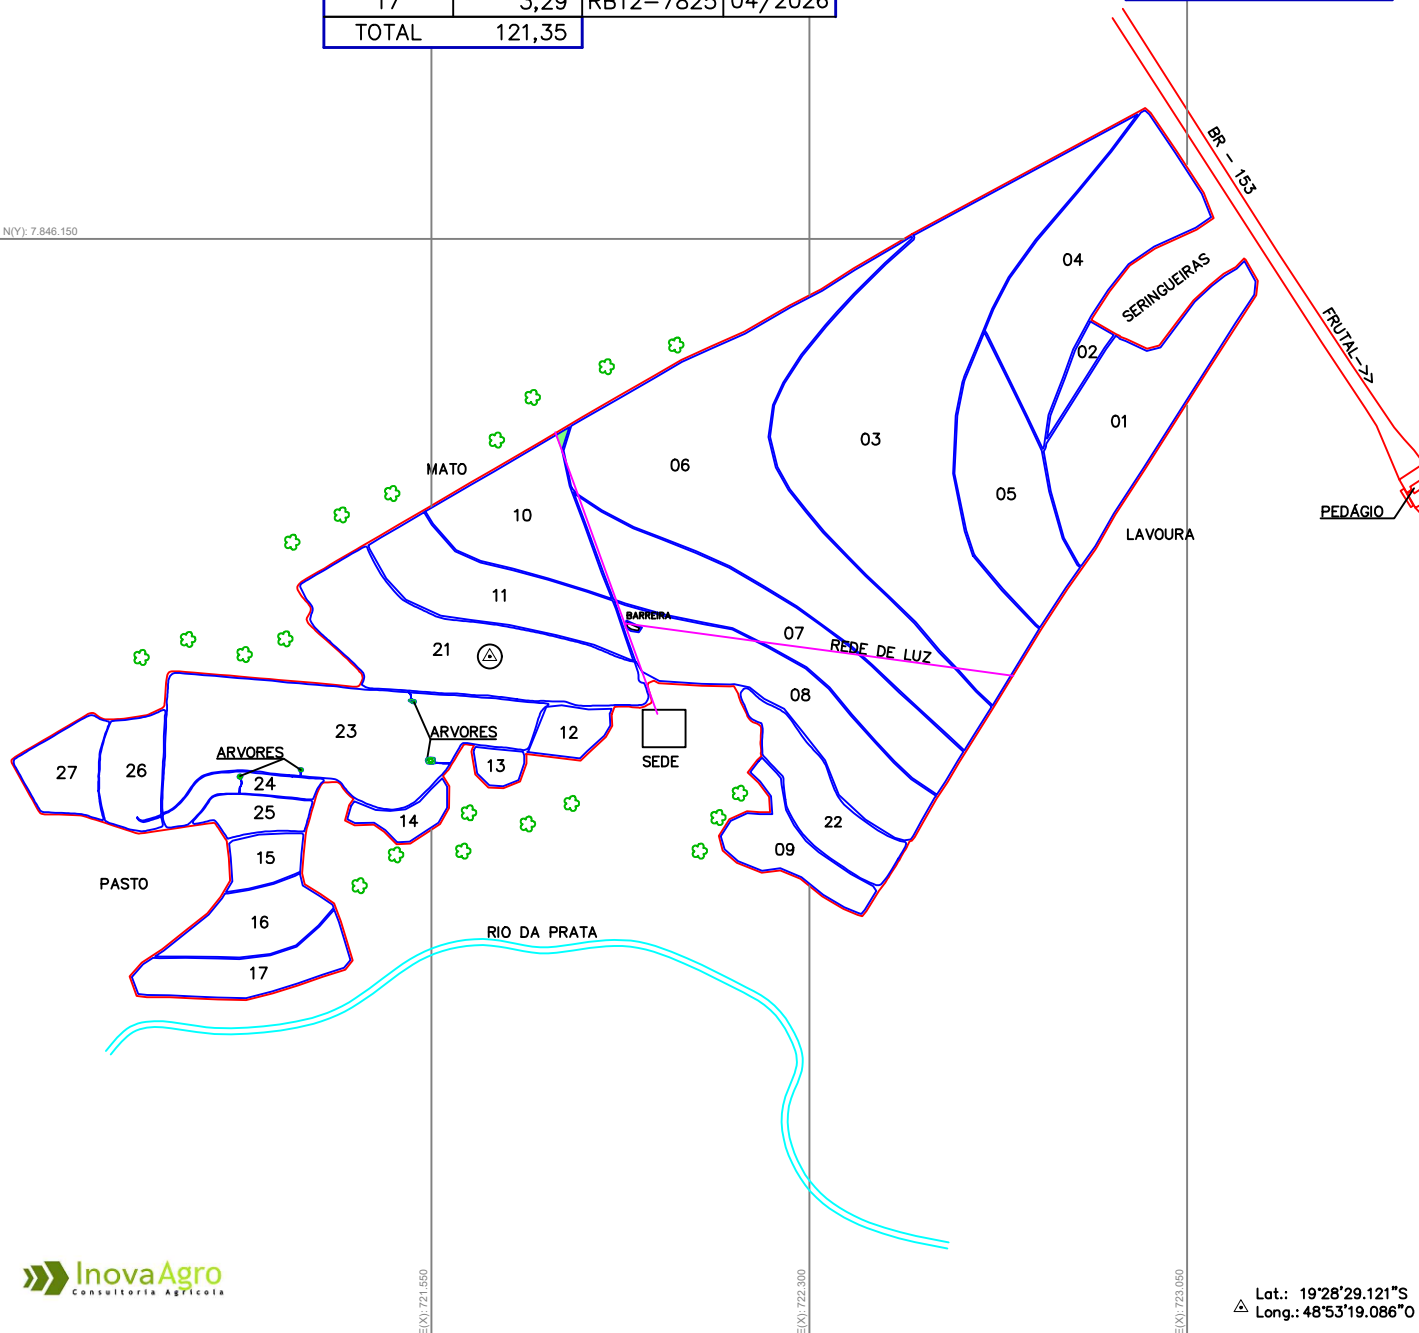

InovaAgro
Consultoria Agrícola

Lat.: 19°28'29.121"S
Long.: 48°53'19.086"E



LEVANTAMENTO TOPOGRÁFICO

PROPRIEDADE:
1124 - SÃO FRANCISCO I
PROPRIETÁRIO:
FRANCISCO ASSIS DE PAULA PRIMO
FORNECEDOR:
FRANCISCO ASSIS DE PAULA PRIMO
ÁREA TOTAL:
163,20 Hectares

QUADRO DE ÁREAS
(ha)

CANA:	156,11
CARREADOR:	7,01
COMPLEMENTARES:	0,08

Desenhado por:	LEANDRO	Data:	19/05/2026
Revisado por:		Data:	
Engenheiro Agrimensor: LEANDRO NASCIMENTO			
Município:	PRATA - MG	Escala:	1 : 15.000

Núcleo:	16 PRATA
Data Levant.:	17/05/2026