


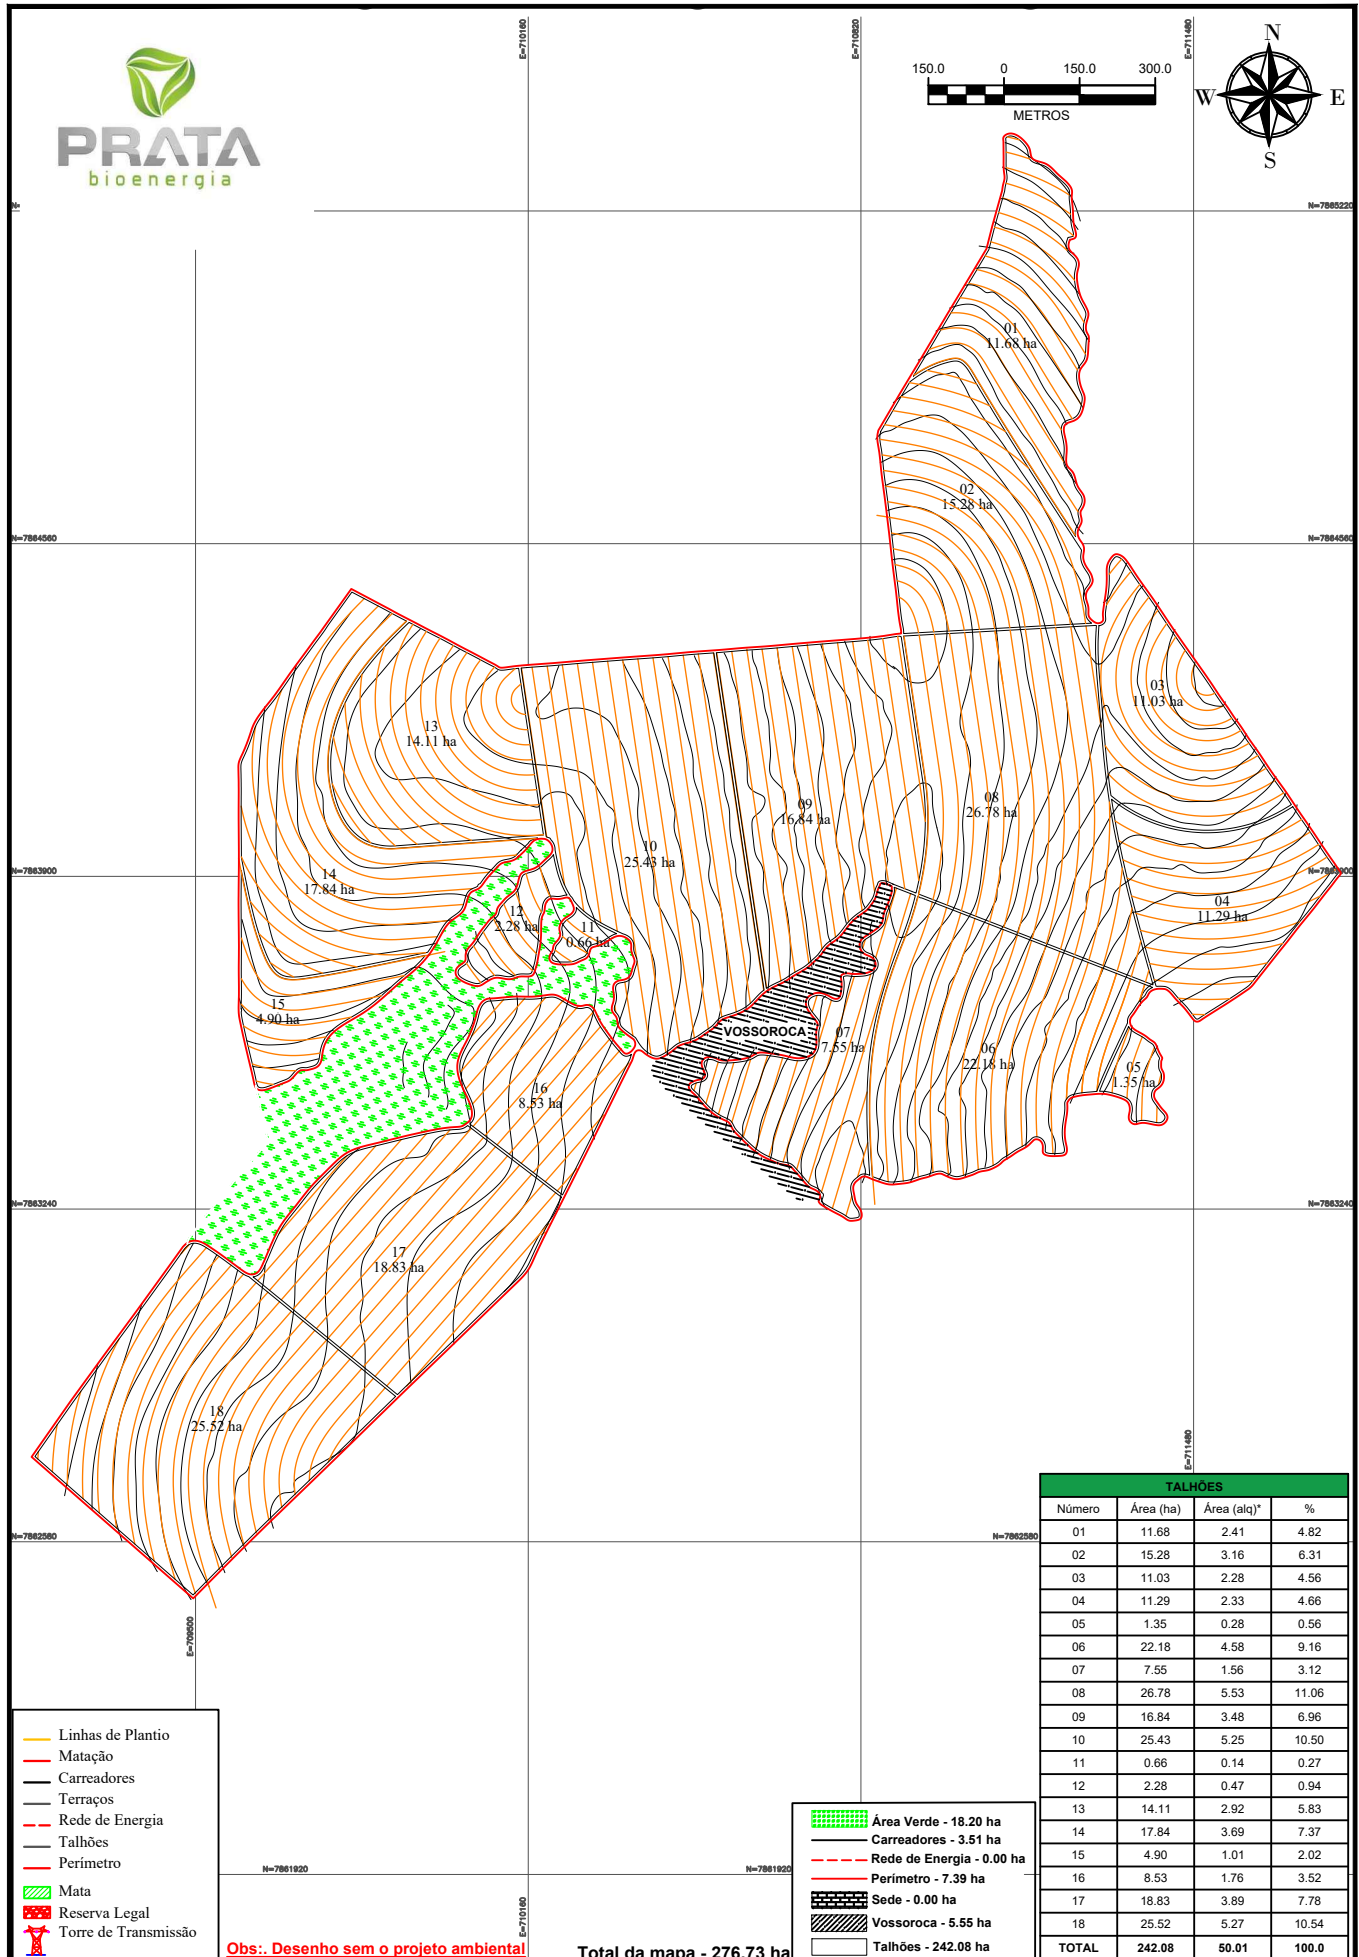

- Linhas de Plantio
- Matação
- Carreadores
- Terraços
- Rede de Energia
- Talhões
- Perímetro
- ▨ Mata
- ▨ Reserva Legal
- ▨ Torre de Transmissão

- ▨ Área Verde - 18.20 ha
- ▨ Carreadores - 3.51 ha
- ▨ Rede de Energia - 0.00 ha
- ▨ Perímetro - 7.39 ha
- ▨ Sede - 0.00 ha
- ▨ Vossoroca - 5.55 ha
- ▨ Talhões - 242.08 ha

TALHÕES			
Número	Área (ha)	Área (alq)*	%
01	11.68	2.41	4.82
02	15.28	3.16	6.31
03	11.03	2.28	4.56
04	11.29	2.33	4.66
05	1.35	0.28	0.56
06	22.18	4.58	9.16
07	7.55	1.56	3.12
08	26.78	5.53	11.06
09	16.84	3.48	6.96
10	25.43	5.25	10.50
11	0.66	0.14	0.27
12	2.28	0.47	0.94
13	14.11	2.92	5.83
14	17.84	3.69	7.37
15	4.90	1.01	2.02
16	8.53	1.76	3.52
17	18.83	3.89	7.78
18	25.52	5.27	10.54
TOTAL	242.08	50.01	100.0

PROJETO		DATA	ESCALA	SISTEMA DE COORDENADAS
Projeto de Curvas de Nível		18-08-2025	1:15000	SIRGAS2000.UTM-22S
DESENHISTA	RESPONSÁVEL		FOLHA	
Fernando Costa	Agro Precisão		1 de 1	
CLIENTE	FAZENDA		TALHÃO	
Prata Bioenergia	Santa Helena		01 ao 18	