


RELAÇÃO DE ÁREAS – CANA 2026			
TALHÃO	ÁREA (ha)	VARIETADE	DATA PL
08	24,32	RB96-6928	05/2026
09	19,38	RB96-6928	05/2026
TOTAL		43,70	

RELAÇÃO DE ÁREAS – CANA 2024			
TALHÃO	ÁREA (ha)	VARIETADE	DATA PL
07	2,72	RB85-5536	01/04/24
TOTAL		2,72	

RELAÇÃO DE ÁREAS – CANA ANTIGA			
TALHÃO	ÁREA (ha)	VARIETADE	DATA PL
03	2,84	RB85-5536	04/2020
04	8,74	RB85-5536	04/2020
05	18,98	RB85-5536	04/2020
06	0,19	RB85-5536	04/2020
TOTAL		30,75	

RELAÇÃO DE ÁREAS COMPLEMENTARES	
DESCRIÇÃO	ÁREA (ha)
MATO	0,22
SEDE	3,04
TOTAL	3,26

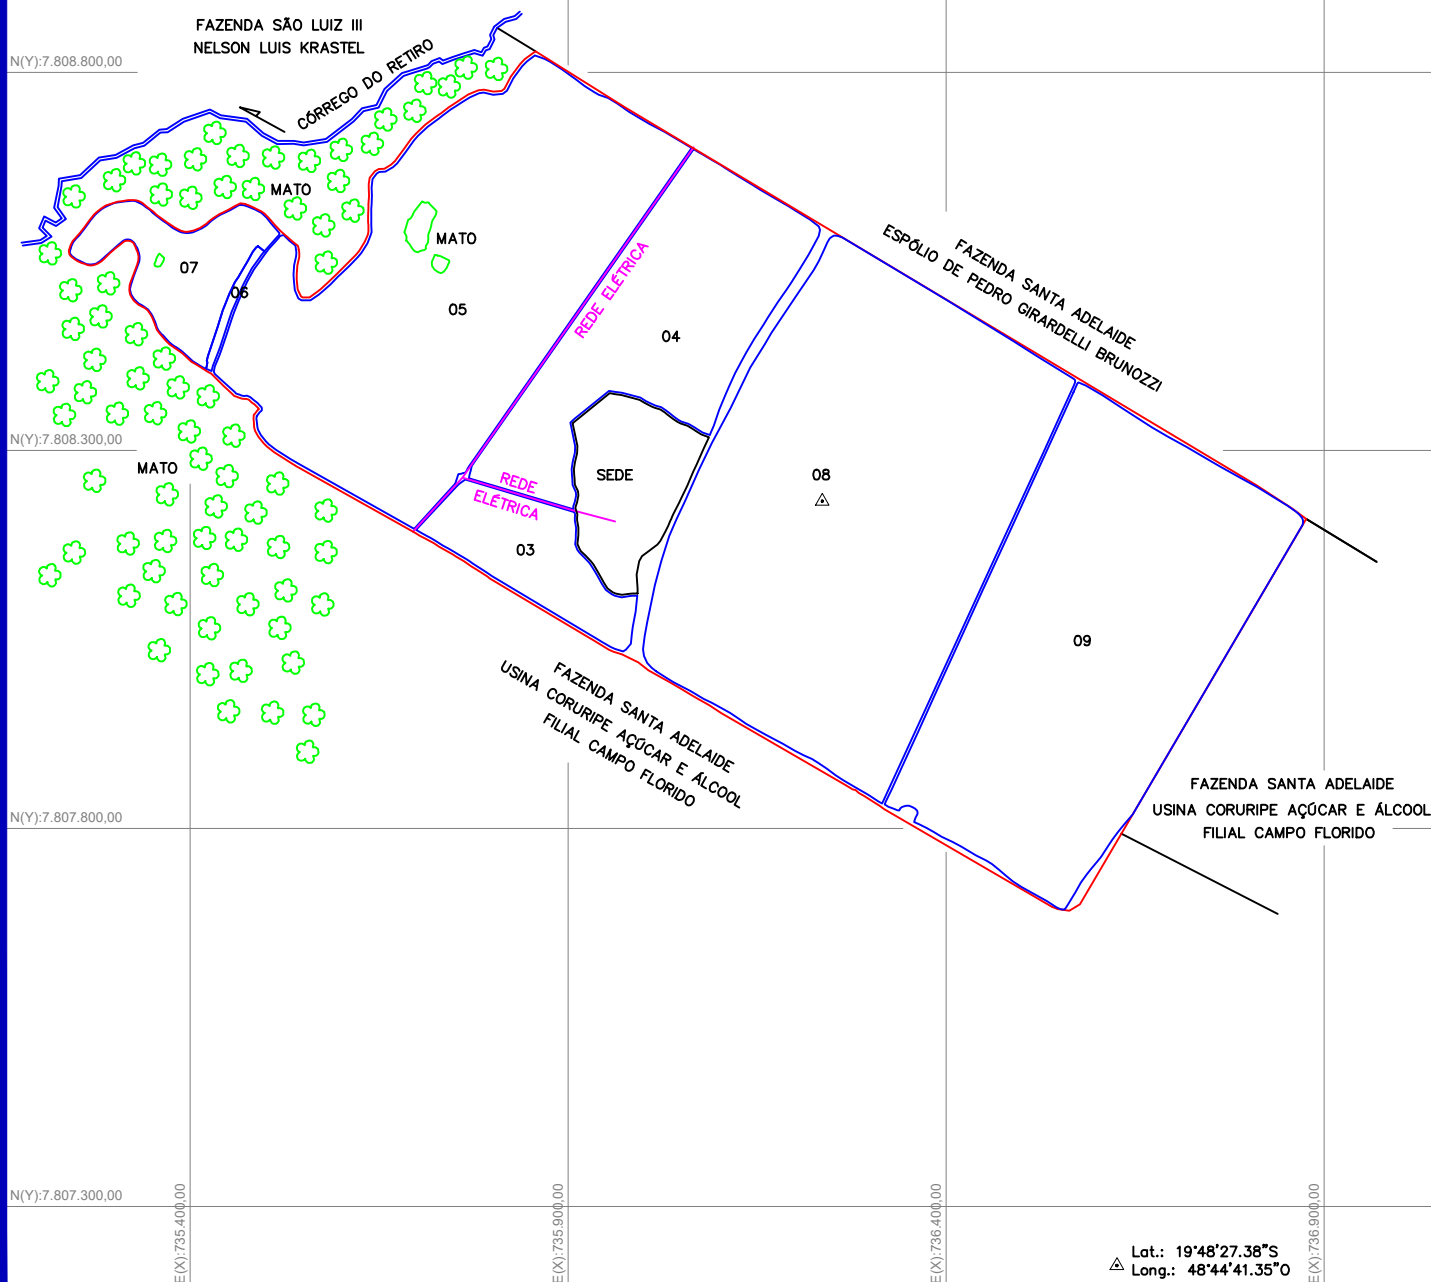

Lat.: 19°48'27.38"S
Long.: 48°44'41.35"E

 USINA CORURIPE Filial Campo Florido	PROPRIEDADE: 524 – FAZENDA SÃO JOSÉ II	QUADRO DE ÁREAS (ha)	CANA 2026:	43,70	Desenhado por: GLAUBER PIMENTEL	Data: 08/05/2026	Núcleo: 1 USINA	
	PROPRIETÁRIO: MARIA JOSÉ GAMBARATO VIEIRA		CARREADOR 2026:	1,73	Atualizado por:	Data:		
	FORNECEDOR: MARIA JOSÉ GAMBARATO VIEIRA		CANA ANTIGA:	33,47	Engº Agrimensor: DANIEL CÉSAR DA SILVA			
	LEVANTAMENTO TOPOGRÁFICO		ÁREA TOTAL: 83,30 Hectares	CARREADOR ANTIGO:	1,14	Município: CAMPO FLORIDO	Escala: 1 : 10.000	Data Levant.: 30/04/2026
				COMPLEMENTARES:	3,26			