


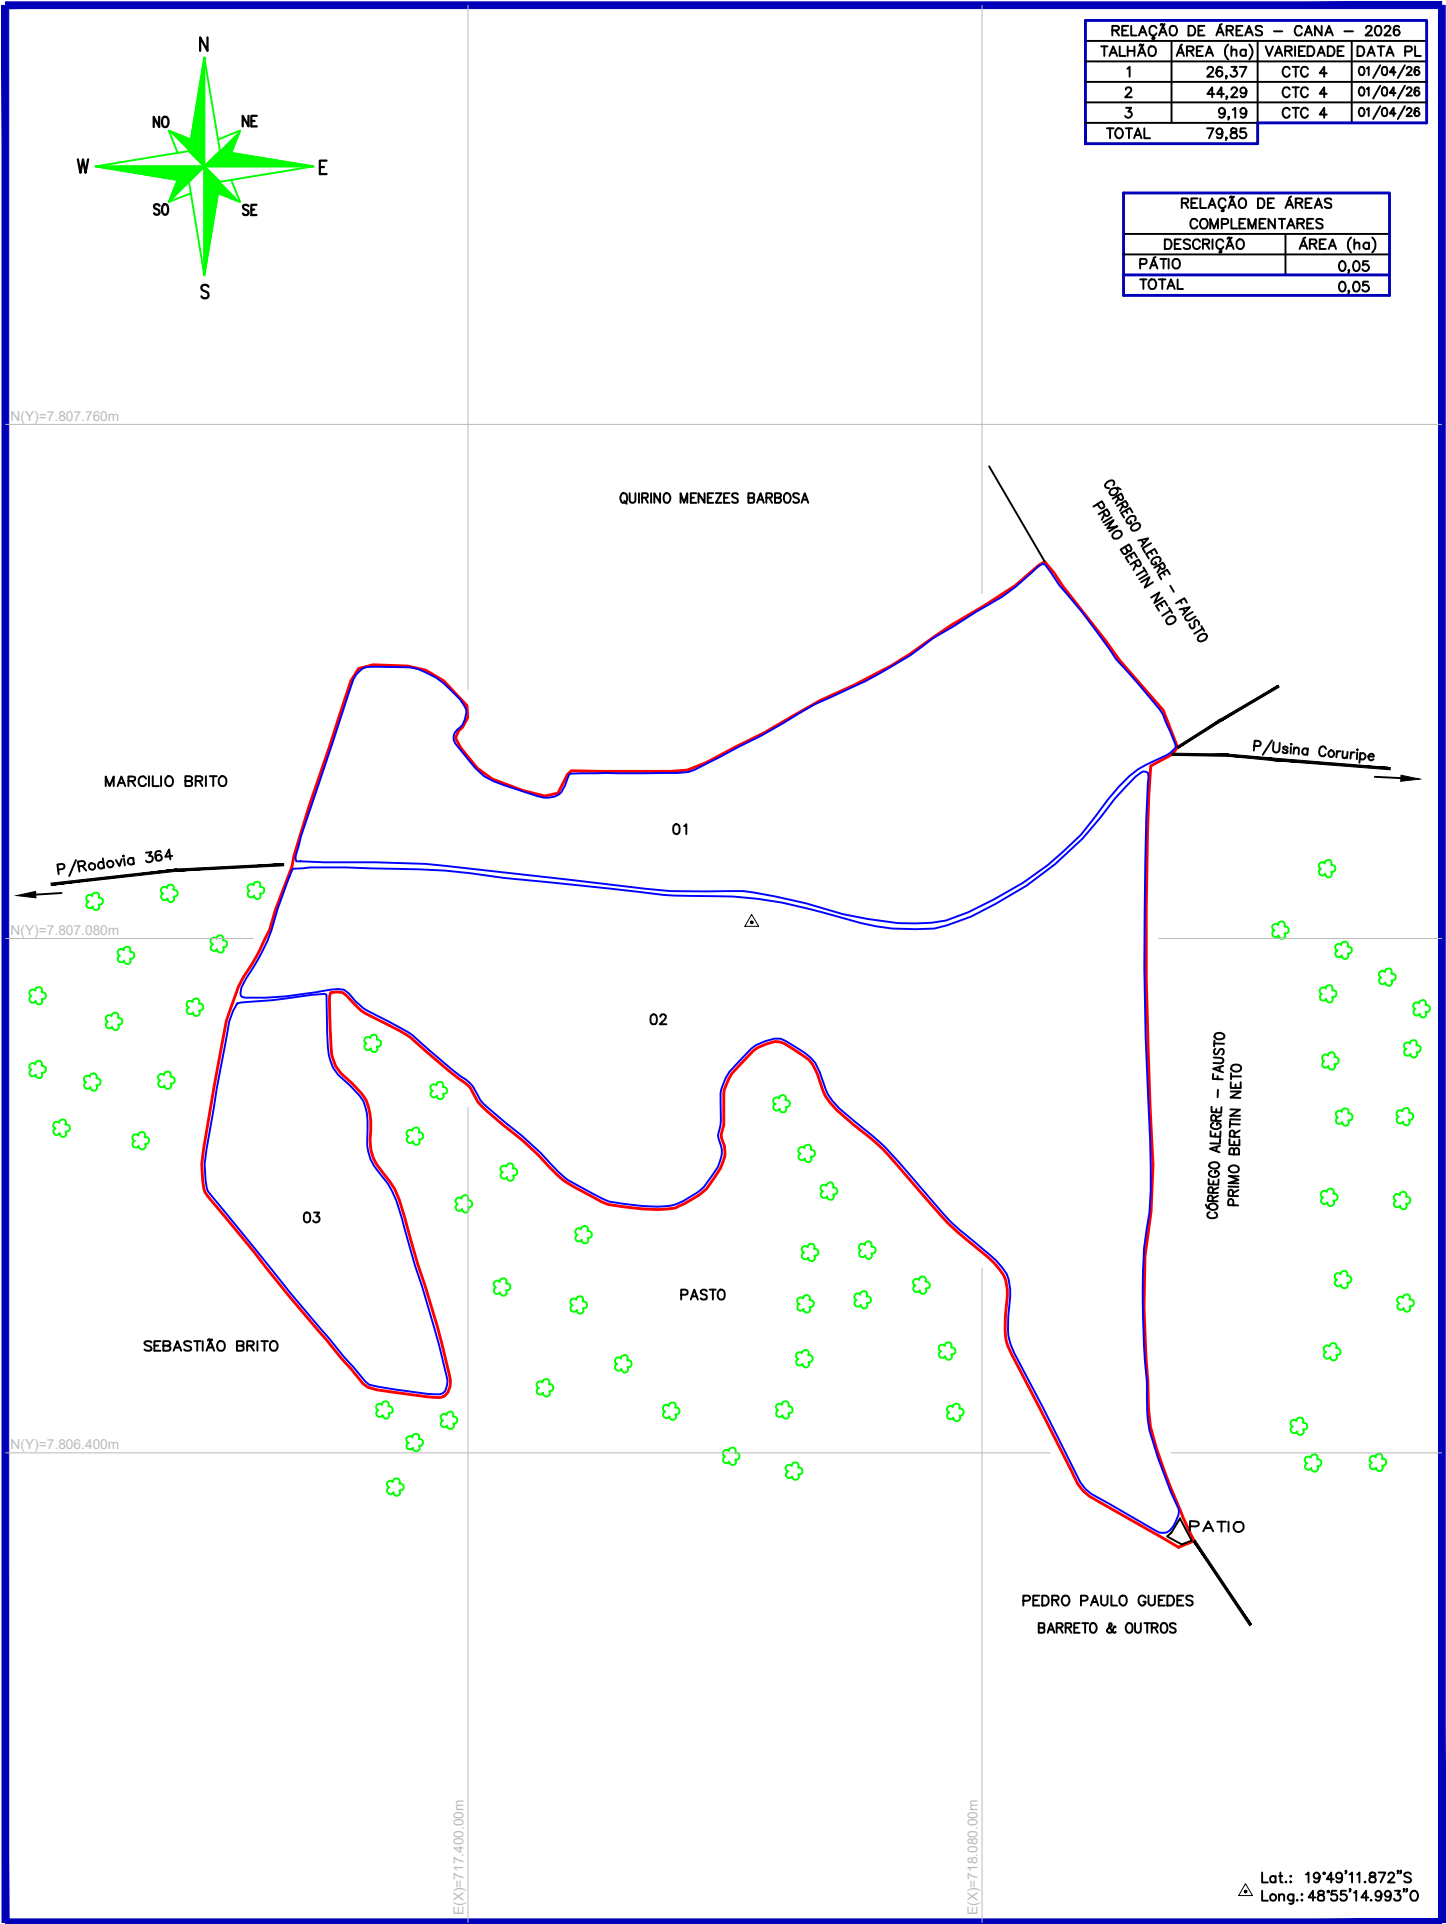

| RELAÇÃO DE ÁREAS - CANA - 2026 |           |           |          |
|--------------------------------|-----------|-----------|----------|
| TALHÃO                         | ÁREA (ha) | VARIEDADE | DATA PL  |
| 1                              | 26,37     | CTC 4     | 01/04/26 |
| 2                              | 44,29     | CTC 4     | 01/04/26 |
| 3                              | 9,19      | CTC 4     | 01/04/26 |
| TOTAL                          |           | 79,85     |          |

| RELAÇÃO DE ÁREAS COMPLEMENTARES |           |
|---------------------------------|-----------|
| DESCRIÇÃO                       | ÁREA (ha) |
| PÁTIO                           | 0,05      |
| TOTAL                           | 0,05      |

Lat.: 19°49'11.872"S  
Long.: 48°55'14.993"O

|   |                                                     |                         |                 |       |                                                 |                       |                               |
|---|-----------------------------------------------------|-------------------------|-----------------|-------|-------------------------------------------------|-----------------------|-------------------------------|
| <br>LEVANTAMENTO TOPOGRÁFICO | PROPRIEDADE:<br>216 – FAZENDA CÓRREGO ALEGRE – IARA | QUADRO DE ÁREAS<br>(ha) | CANA 2026:      | 79,85 | Desenhado por:<br>GLAUBER PIMENTEL              | Data:<br>18/05/2026   | Núcleo:<br><br>05<br>CHAPADÃO |
|   | PROPRIETÁRIO:<br>FAUSTO CUNHA OLIVEIRA JUNIOR       |                         | CARREADOR 2026: | 2,72  | Atualizado por:<br>–                            | Data:<br>–            |                               |
|   | FORNECEDOR:<br>PRIMO BERTIN NETO                    |                         | COMPLEMENTARES: | 0,05  | Engenheiro Agrimensor:<br>DANIEL CÉSAR DA SILVA |                       |                               |
|   | ÁREA TOTAL:<br>82,62 Hectares                       |                         |                 |       | Município:<br>FRUTAL–MG                         | Escala:<br>1 : 10.000 | Data Levant.:<br>15/06/2026   |

Obs.: Conferido perímetro georreferenciado.  
Datum Sirgas2000 / UTM zona 22S (CM 51W)