

RELAÇÃO DE ÁREAS – CANA ANTIGA			
TALHÃO	ÁREA (ha)	VARIETADE	DATA PL
01	12,19	IACSP01-5503	10/04/25
17	12,86	RB85-5156	10/04/25
20	16,57	CTC-04	04/2021
21	24,87	CTC-04	04/2021
22	30,86	CTC-04	04/2021
23	47,16	CTC-04	04/2021
24	15,61	CTC-04	04/2021
25	19,97	CTC-04	04/2021
26	1,21	CTC-04	04/2021
27	4,40	CTC-04	04/2021
28	4,84	CTC-04	04/2021
29	0,58	CTC-04	04/2021
30	5,62	CTC-04	04/2021
31	11,23	CTC-04	04/2022
TOTAL		207,97	

RELAÇÃO DE ÁREAS – CANA 2026			
TALHÃO	ÁREA (ha)	VARIETADE	DATA PL
32	4,84	CTC-4	01/04/26
33	22,65	CTC-4	01/04/26
34	5,03	CTC-4	01/04/26
35	19,91	CTC-4	01/04/26
36	14,49	CTC-4	01/04/26
37	7,50	CTC-4	01/04/26
38	25,07	CTC-4	01/04/26
39	5,45	CTC-4	01/04/26
40	8,20	CTC-4	01/04/26
41	4,09	CTC-4	01/04/26
42	4,92	CTC-4	01/04/26
43	36,67	CTC-4	01/04/26
44	28,79	CTC-4	01/04/26
45	15,23	CTC-4	01/04/26
TOTAL		202,84	

RELAÇÃO DE ÁREAS COMPLEMENTARES	
DESCRIÇÃO	ÁREA (ha)
MATO	0,61
BOLSÃO	0,11
PÁTIO	0,21
TOTAL	0,93


N(y):7.808.500,00

N(y):7.806.500,00

N(y):7.804.500,00

E(x):718.400,00

E(x):720.400,00

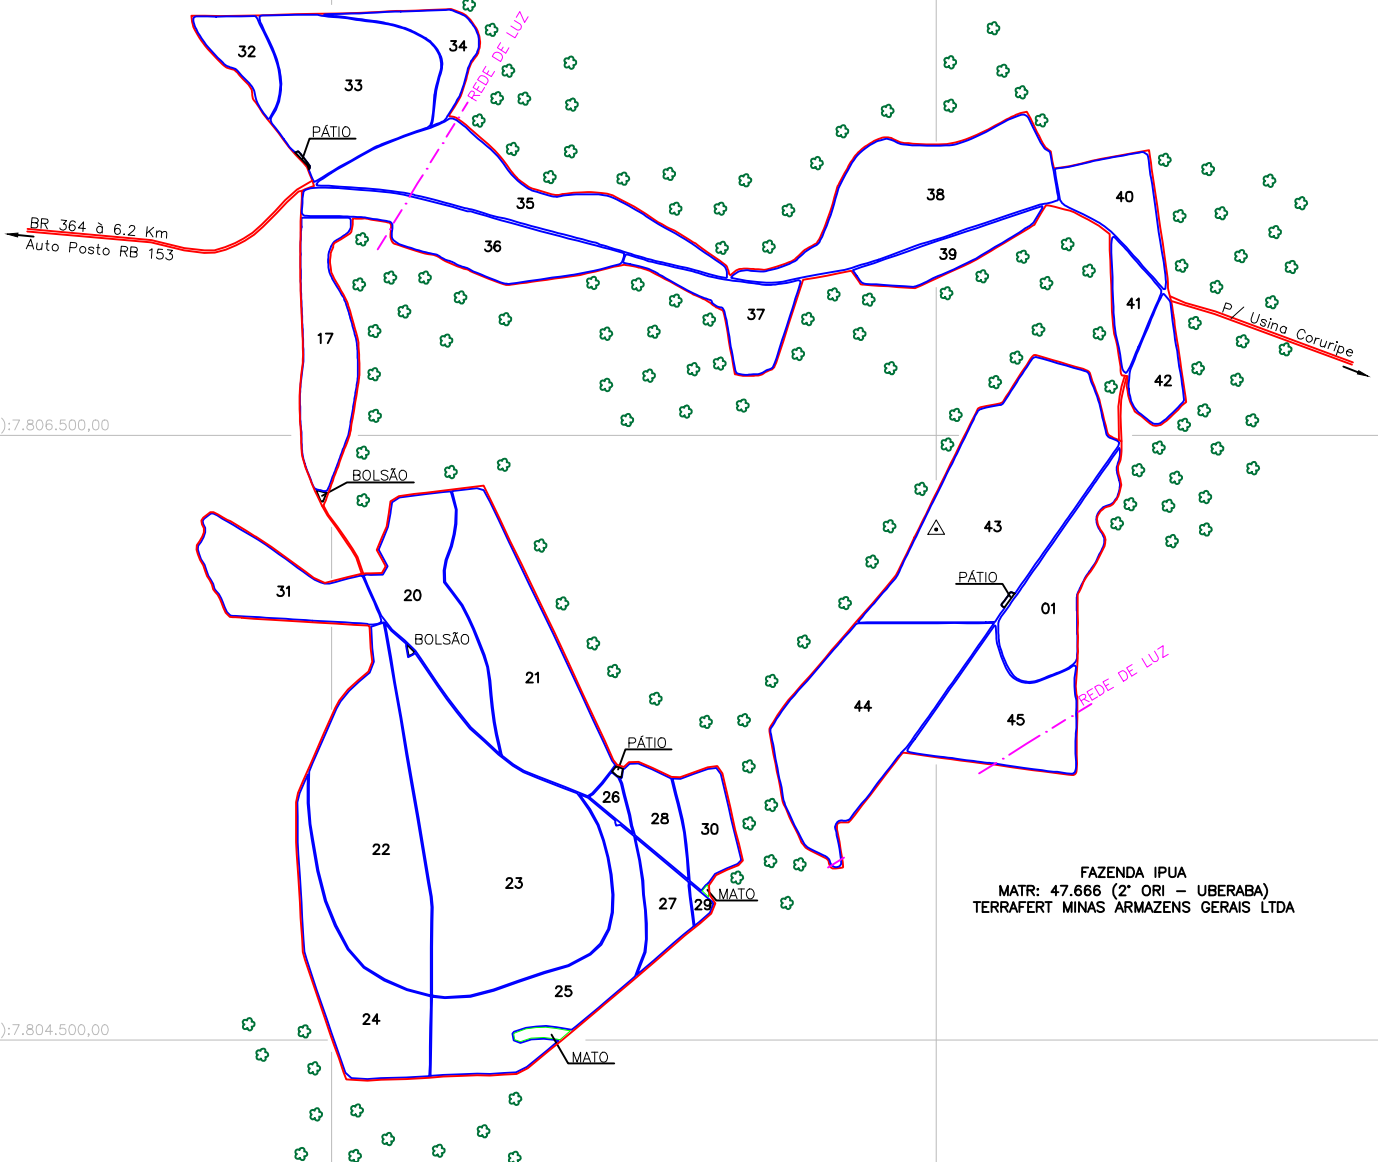

FAZENDA IPUÁ
MATR: 47.666 (2º ORI – UBERABA)
TERRAFERT MINAS ARMAZENS GERAIS LTDA

Lat.: 19°49'40,47"S
Long.: 48°53'44,44"O



LEVANTAMENTO TOPOGRÁFICO

PROPRIEDADE:
441 – FAZENDA Córrego Alegre – Fausto
PROPRIETÁRIO:
FAUSTO CUNHA OLIVEIRA JUNIOR
FORNECEDOR:
PRIMO BERTIN NETO
ÁREA TOTAL:
429,74 Hectares

QUADRO DE ÁREAS
(ha)

CANA 2026: 202,84
CARREADOR 2026: 9,25
CANA ANTIGA: 207,97
CARREADOR ANTIGO: 8,75
COMPLEMENTARES: 0,93

Desenhado por:
MÁRCIO GALASSI
Revisado por:
—
Engº Agrimensor:
DANIEL CESAR DA SILVA
Município:
FRUTAL – MG

Data:
18/05/2026
Data:
—
Escala:
1 : 25.000

Núcleo:
5
CHAPADÃO
Data Levant.:
05/2026

Datum Sirgas2000